

# Дизайн квартиры в ЖК Черняховского

1. Стилистическое решение спальни №1
2. Стилистическое решение санузла №3
3. Стилистическое решение ванной №4
4. Стилистическое решение кабинета №5
5. Стилистическое решение детской №6
6. Стилистическое решение прихожей №8
7. Стилистическое решение гостиной №9
8. Стилистическое решение кухни №10
  
9. Обмерный план
10. План возводимых перегородок
11. План расстановки мебели
12. План расстановки светильников
13. План привязки светильников
14. План привязки розеток
15. План полов
16. План раскладки плинтуса
17. План отделки стен
18. План потолков
19. План расстановки сантехнических приборов
20. План расстановки радиаторов и кондиционеров
21. План и спецификация заполнения дверных проемов
  
22. Развертки спальни №1
23. Развертки гардеробной №2
24. Развертки санузла №3
25. Развертки ванной №4
26. Развертки кабинета №5
27. Развертки детской №6
28. Развертки коридора №7
29. Развертки прихожей №8
30. Развертки гостиной №9
31. Развертки кухни №10
32. Развертки балкона №11
  
33. Спецификация отделочных материалов. Полы
34. Спецификация отделочных материалов. Стены. Лепнина
  
35. Спецификация светильников. Лист 1
36. Спецификация светильников. Лист 2
37. Спецификация светильников. Лист 3





















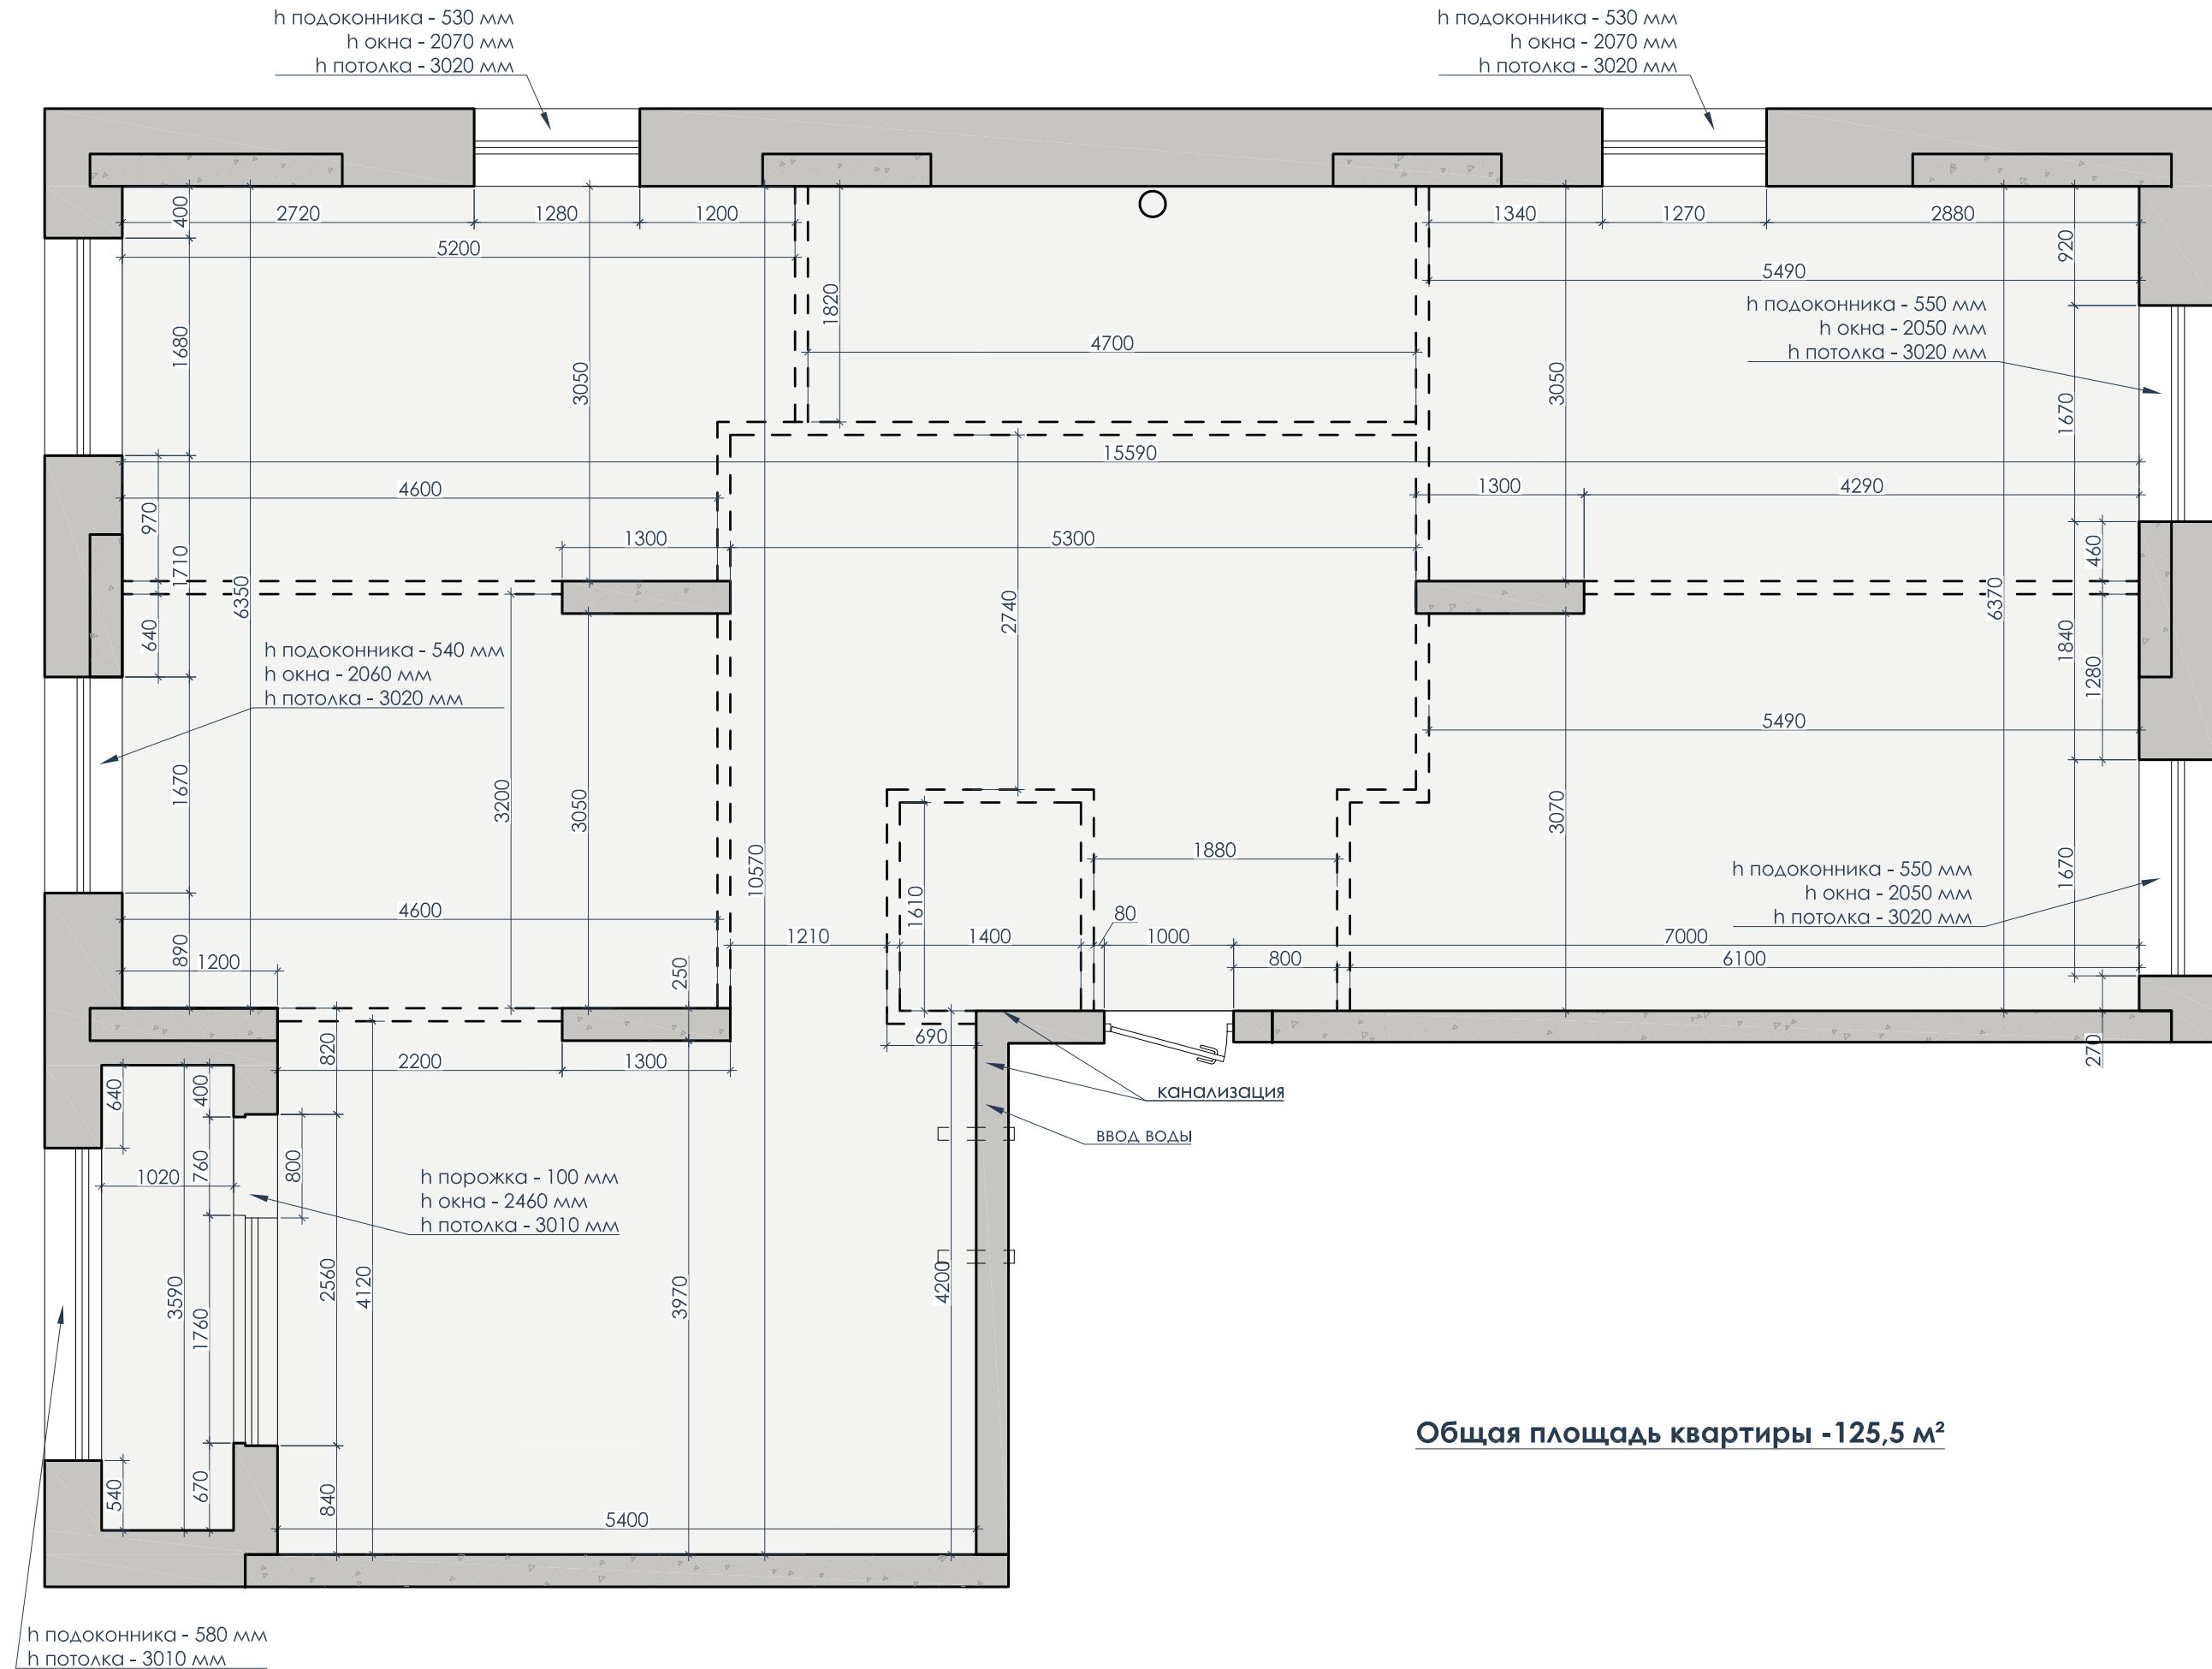

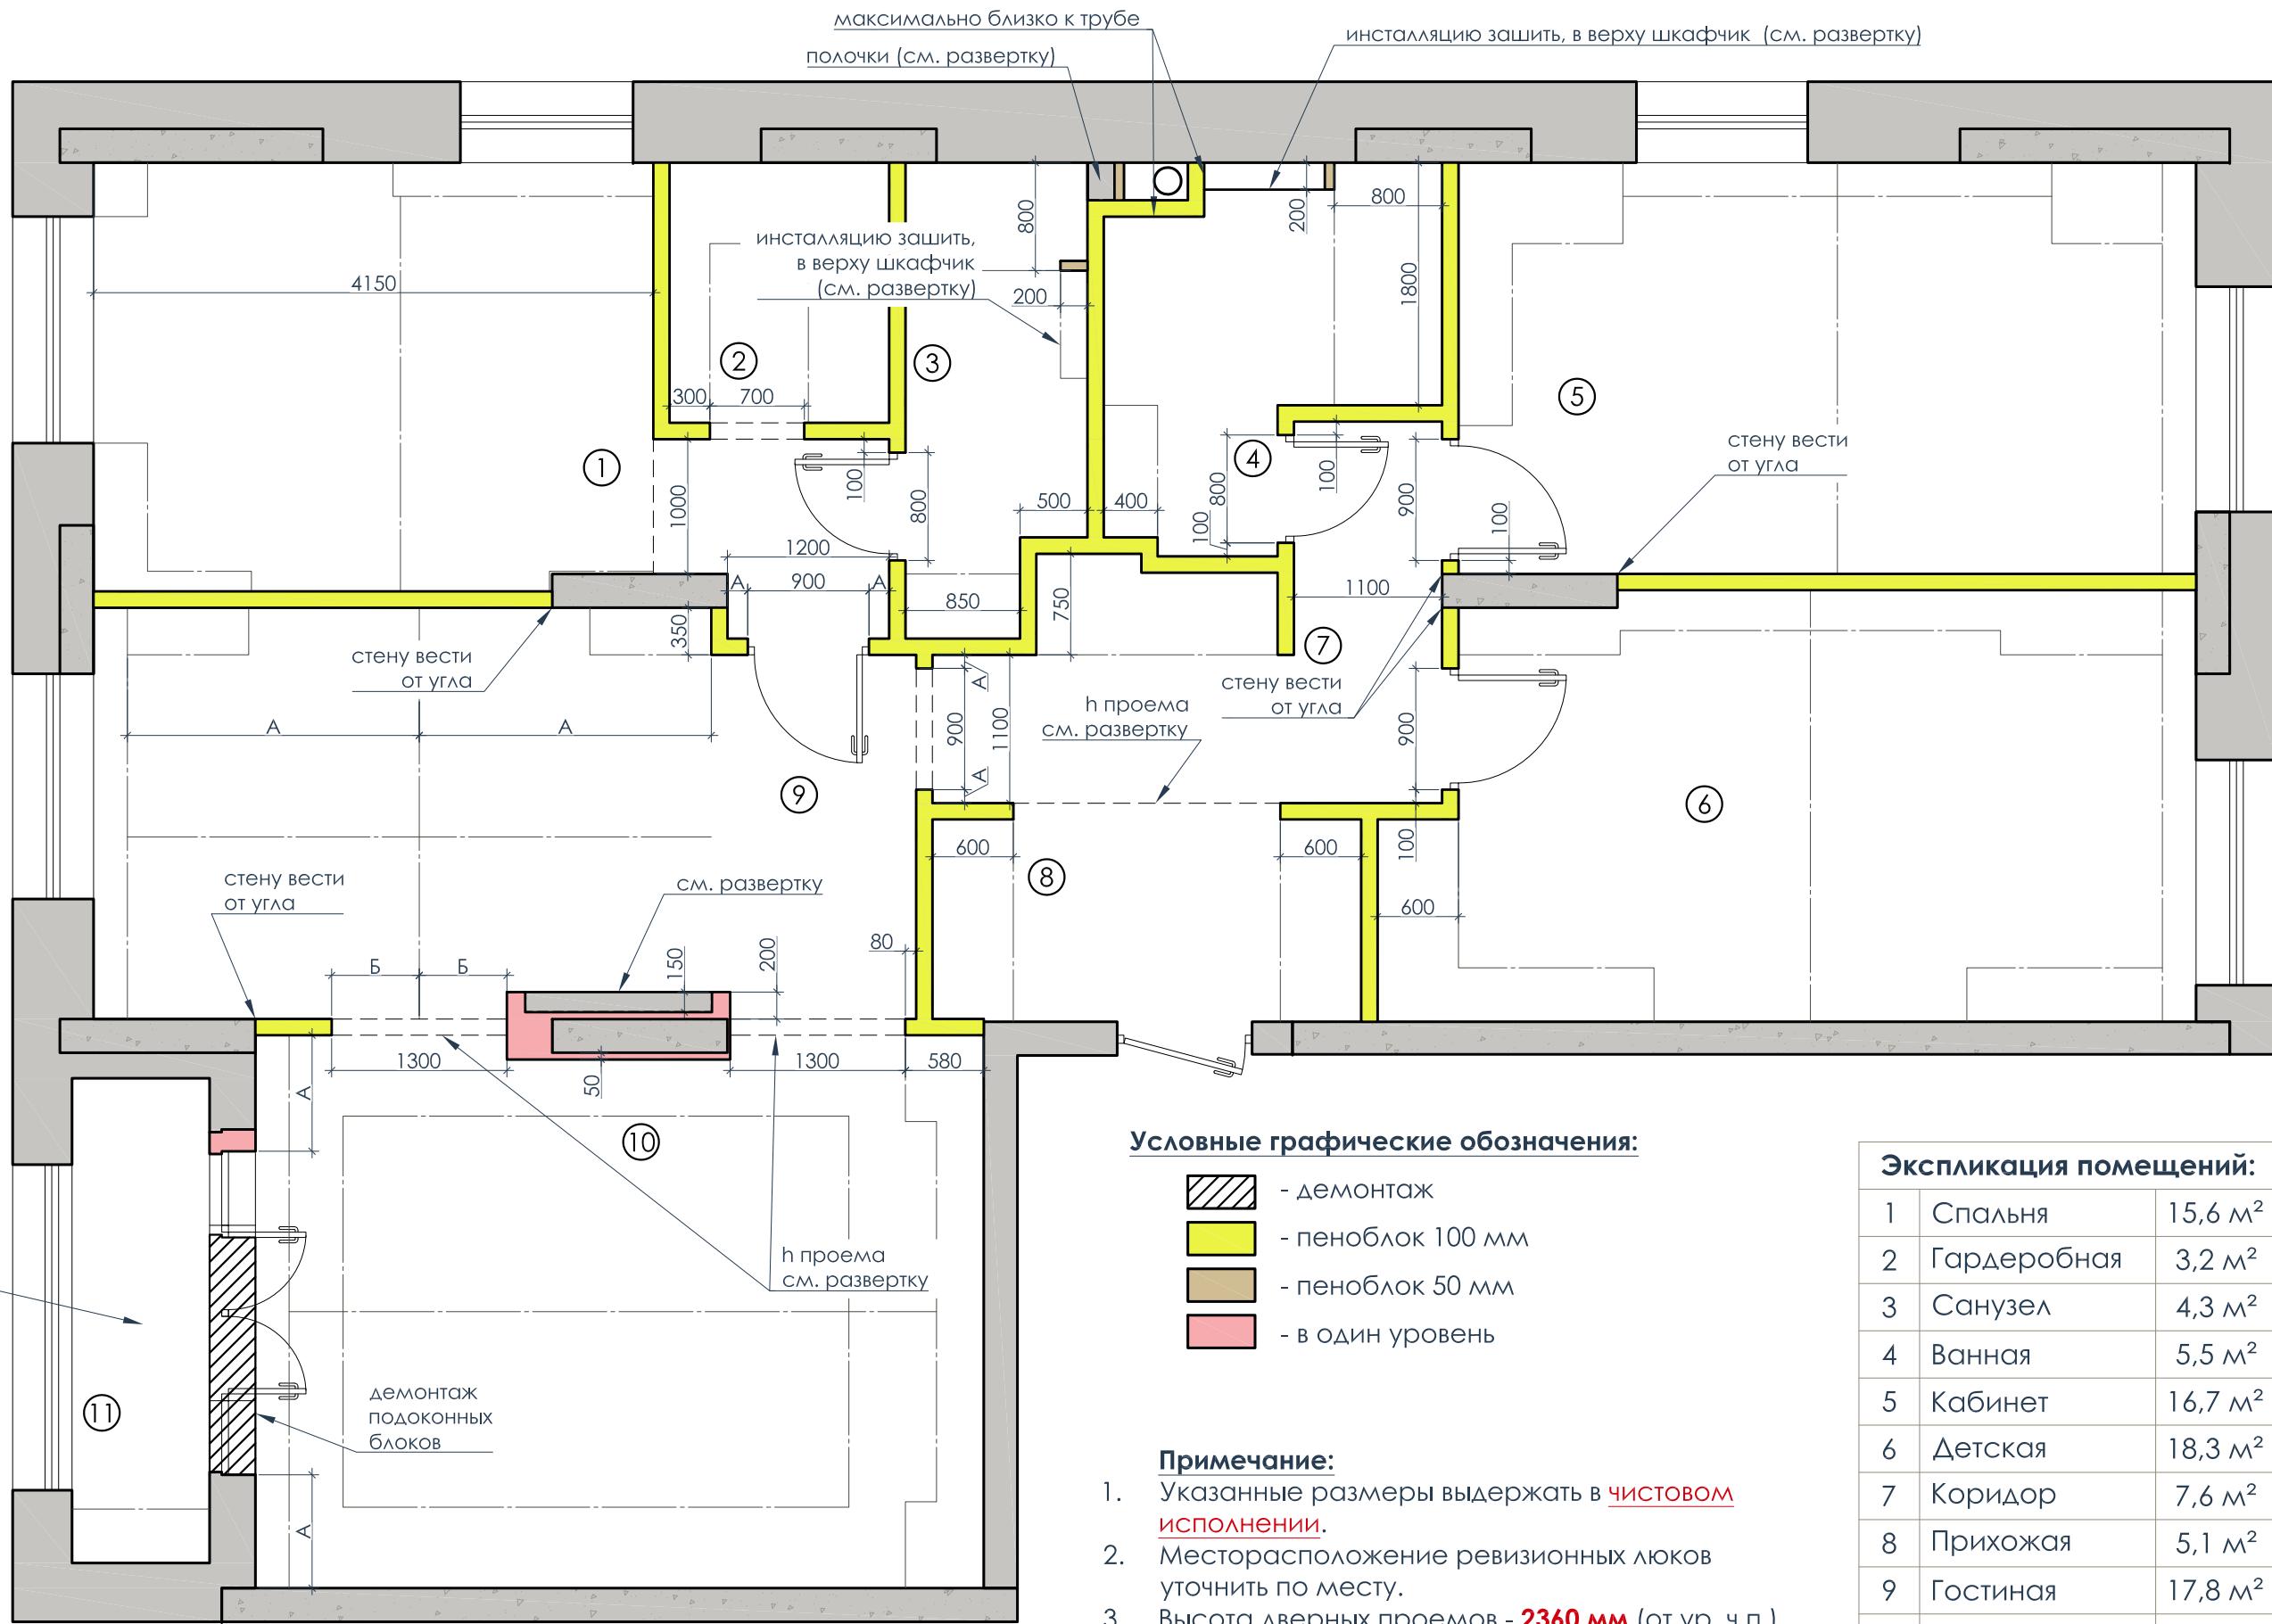

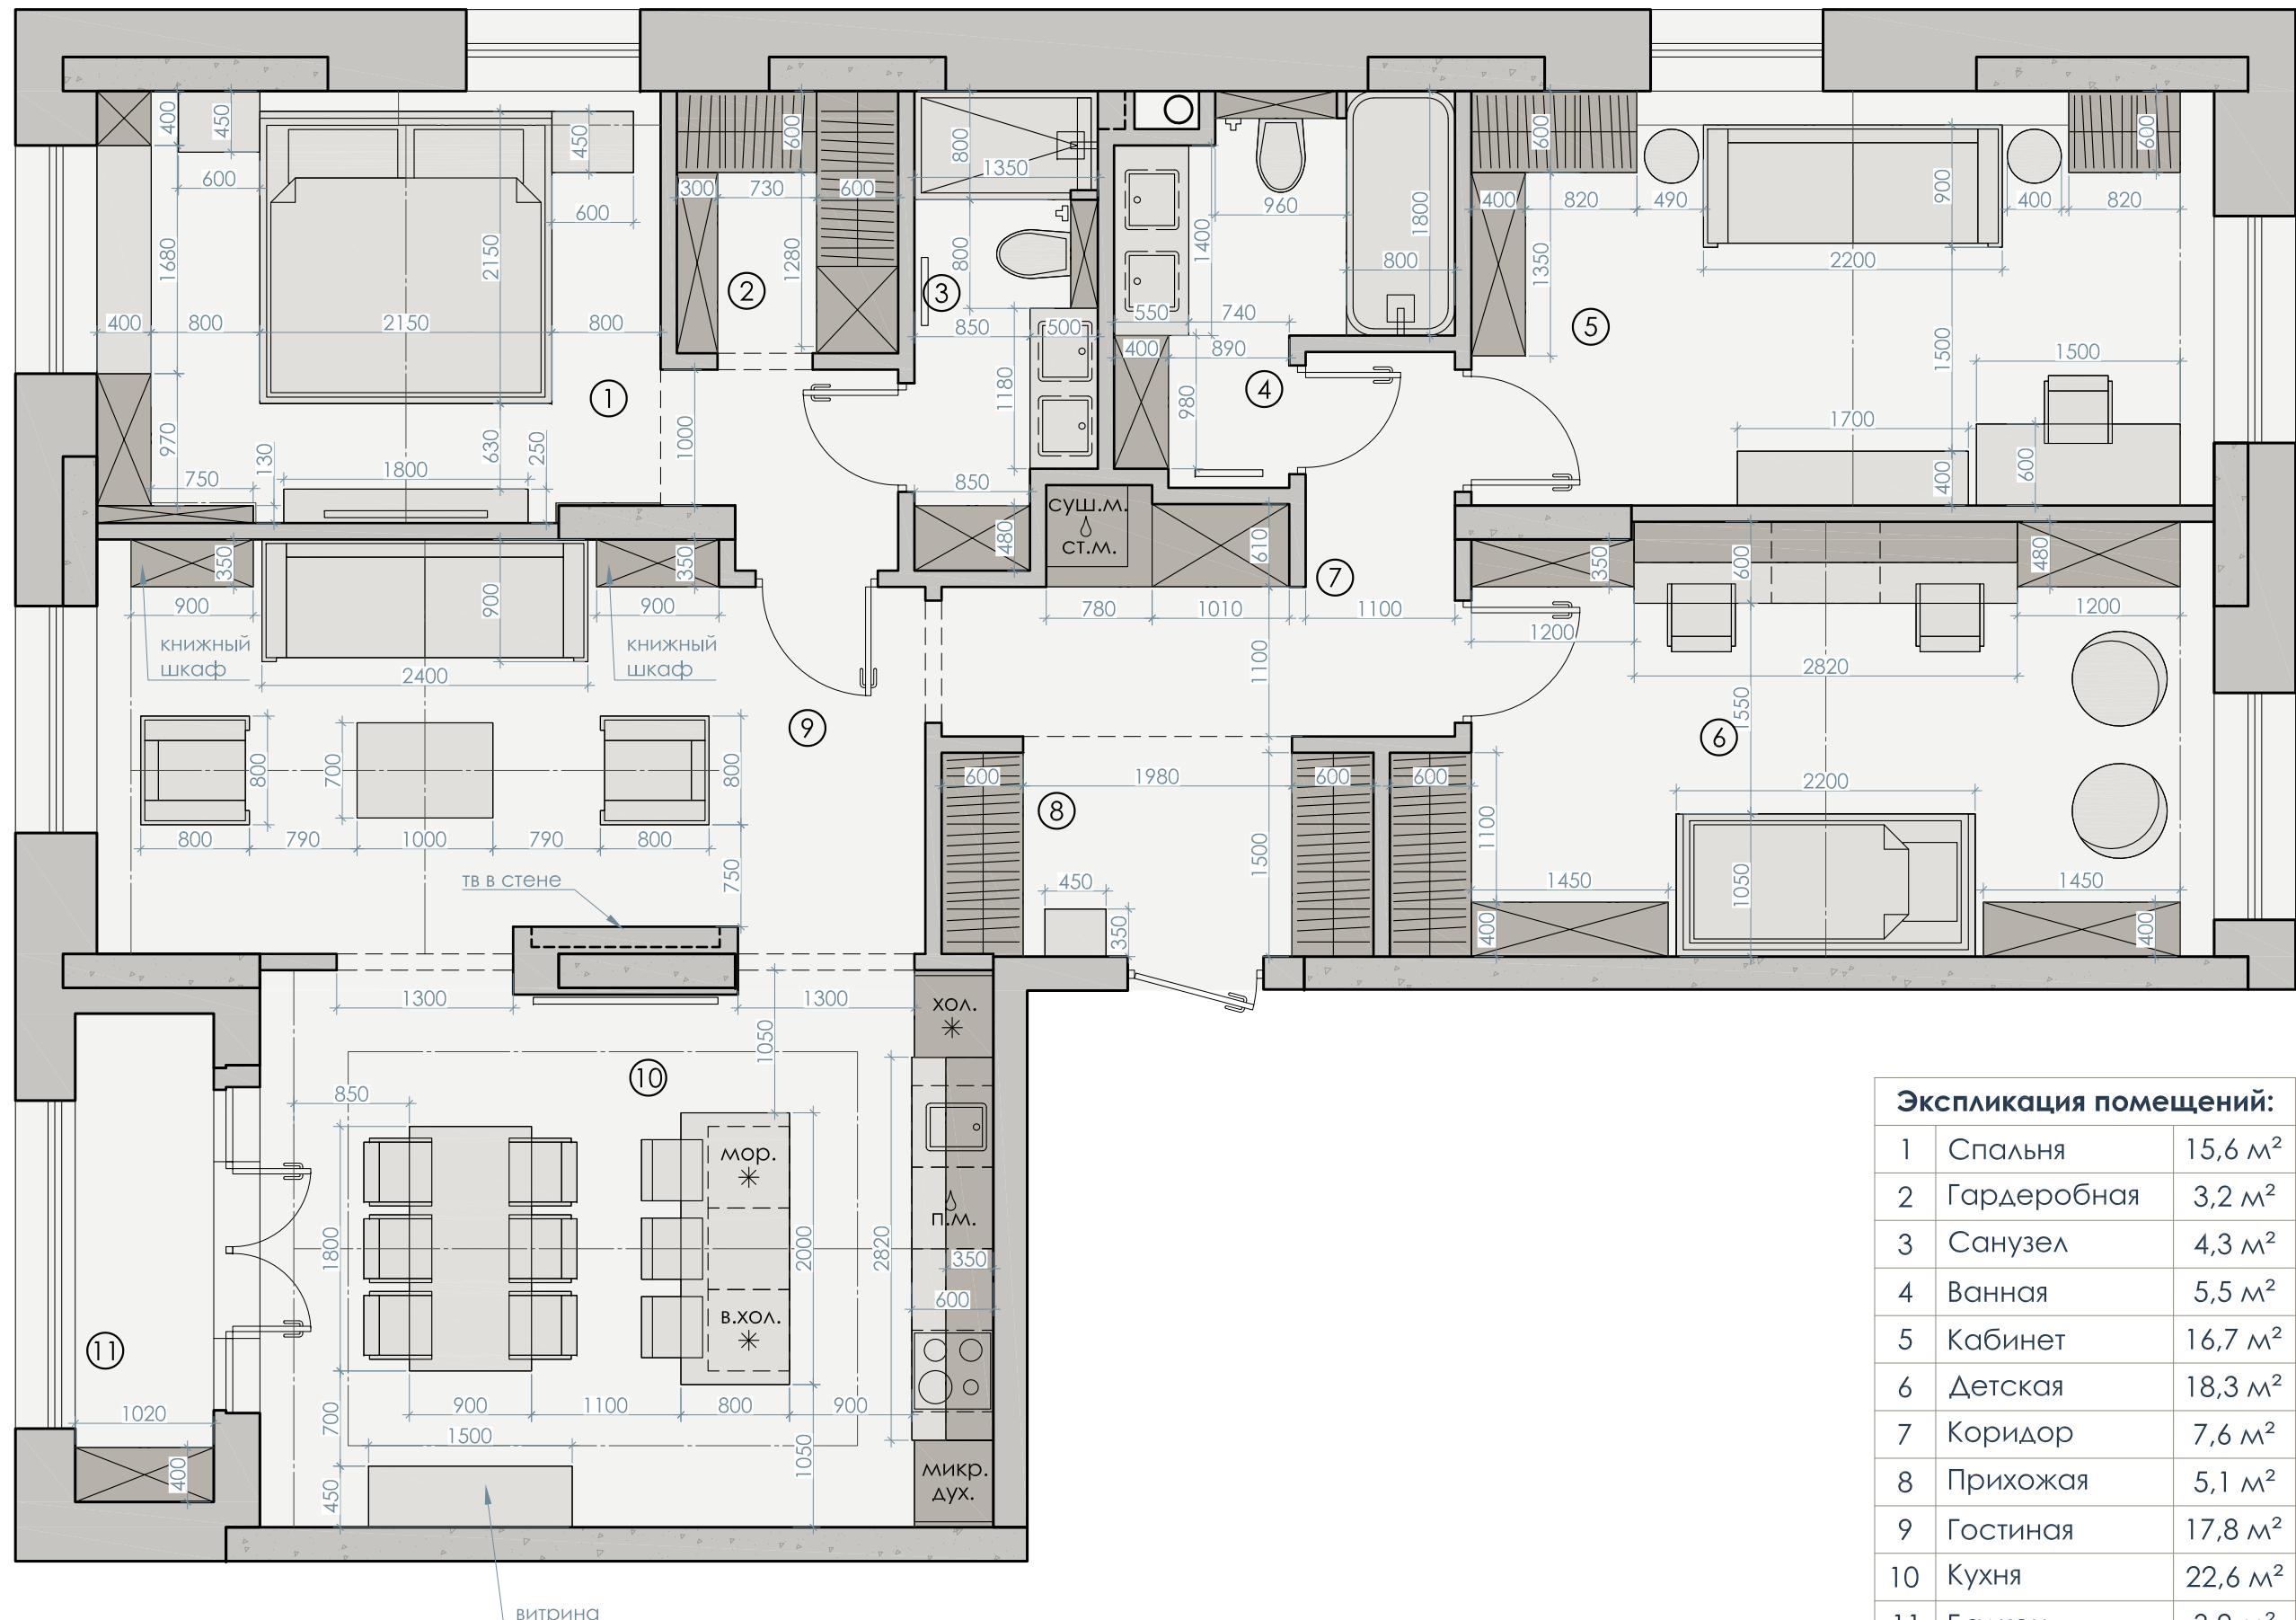

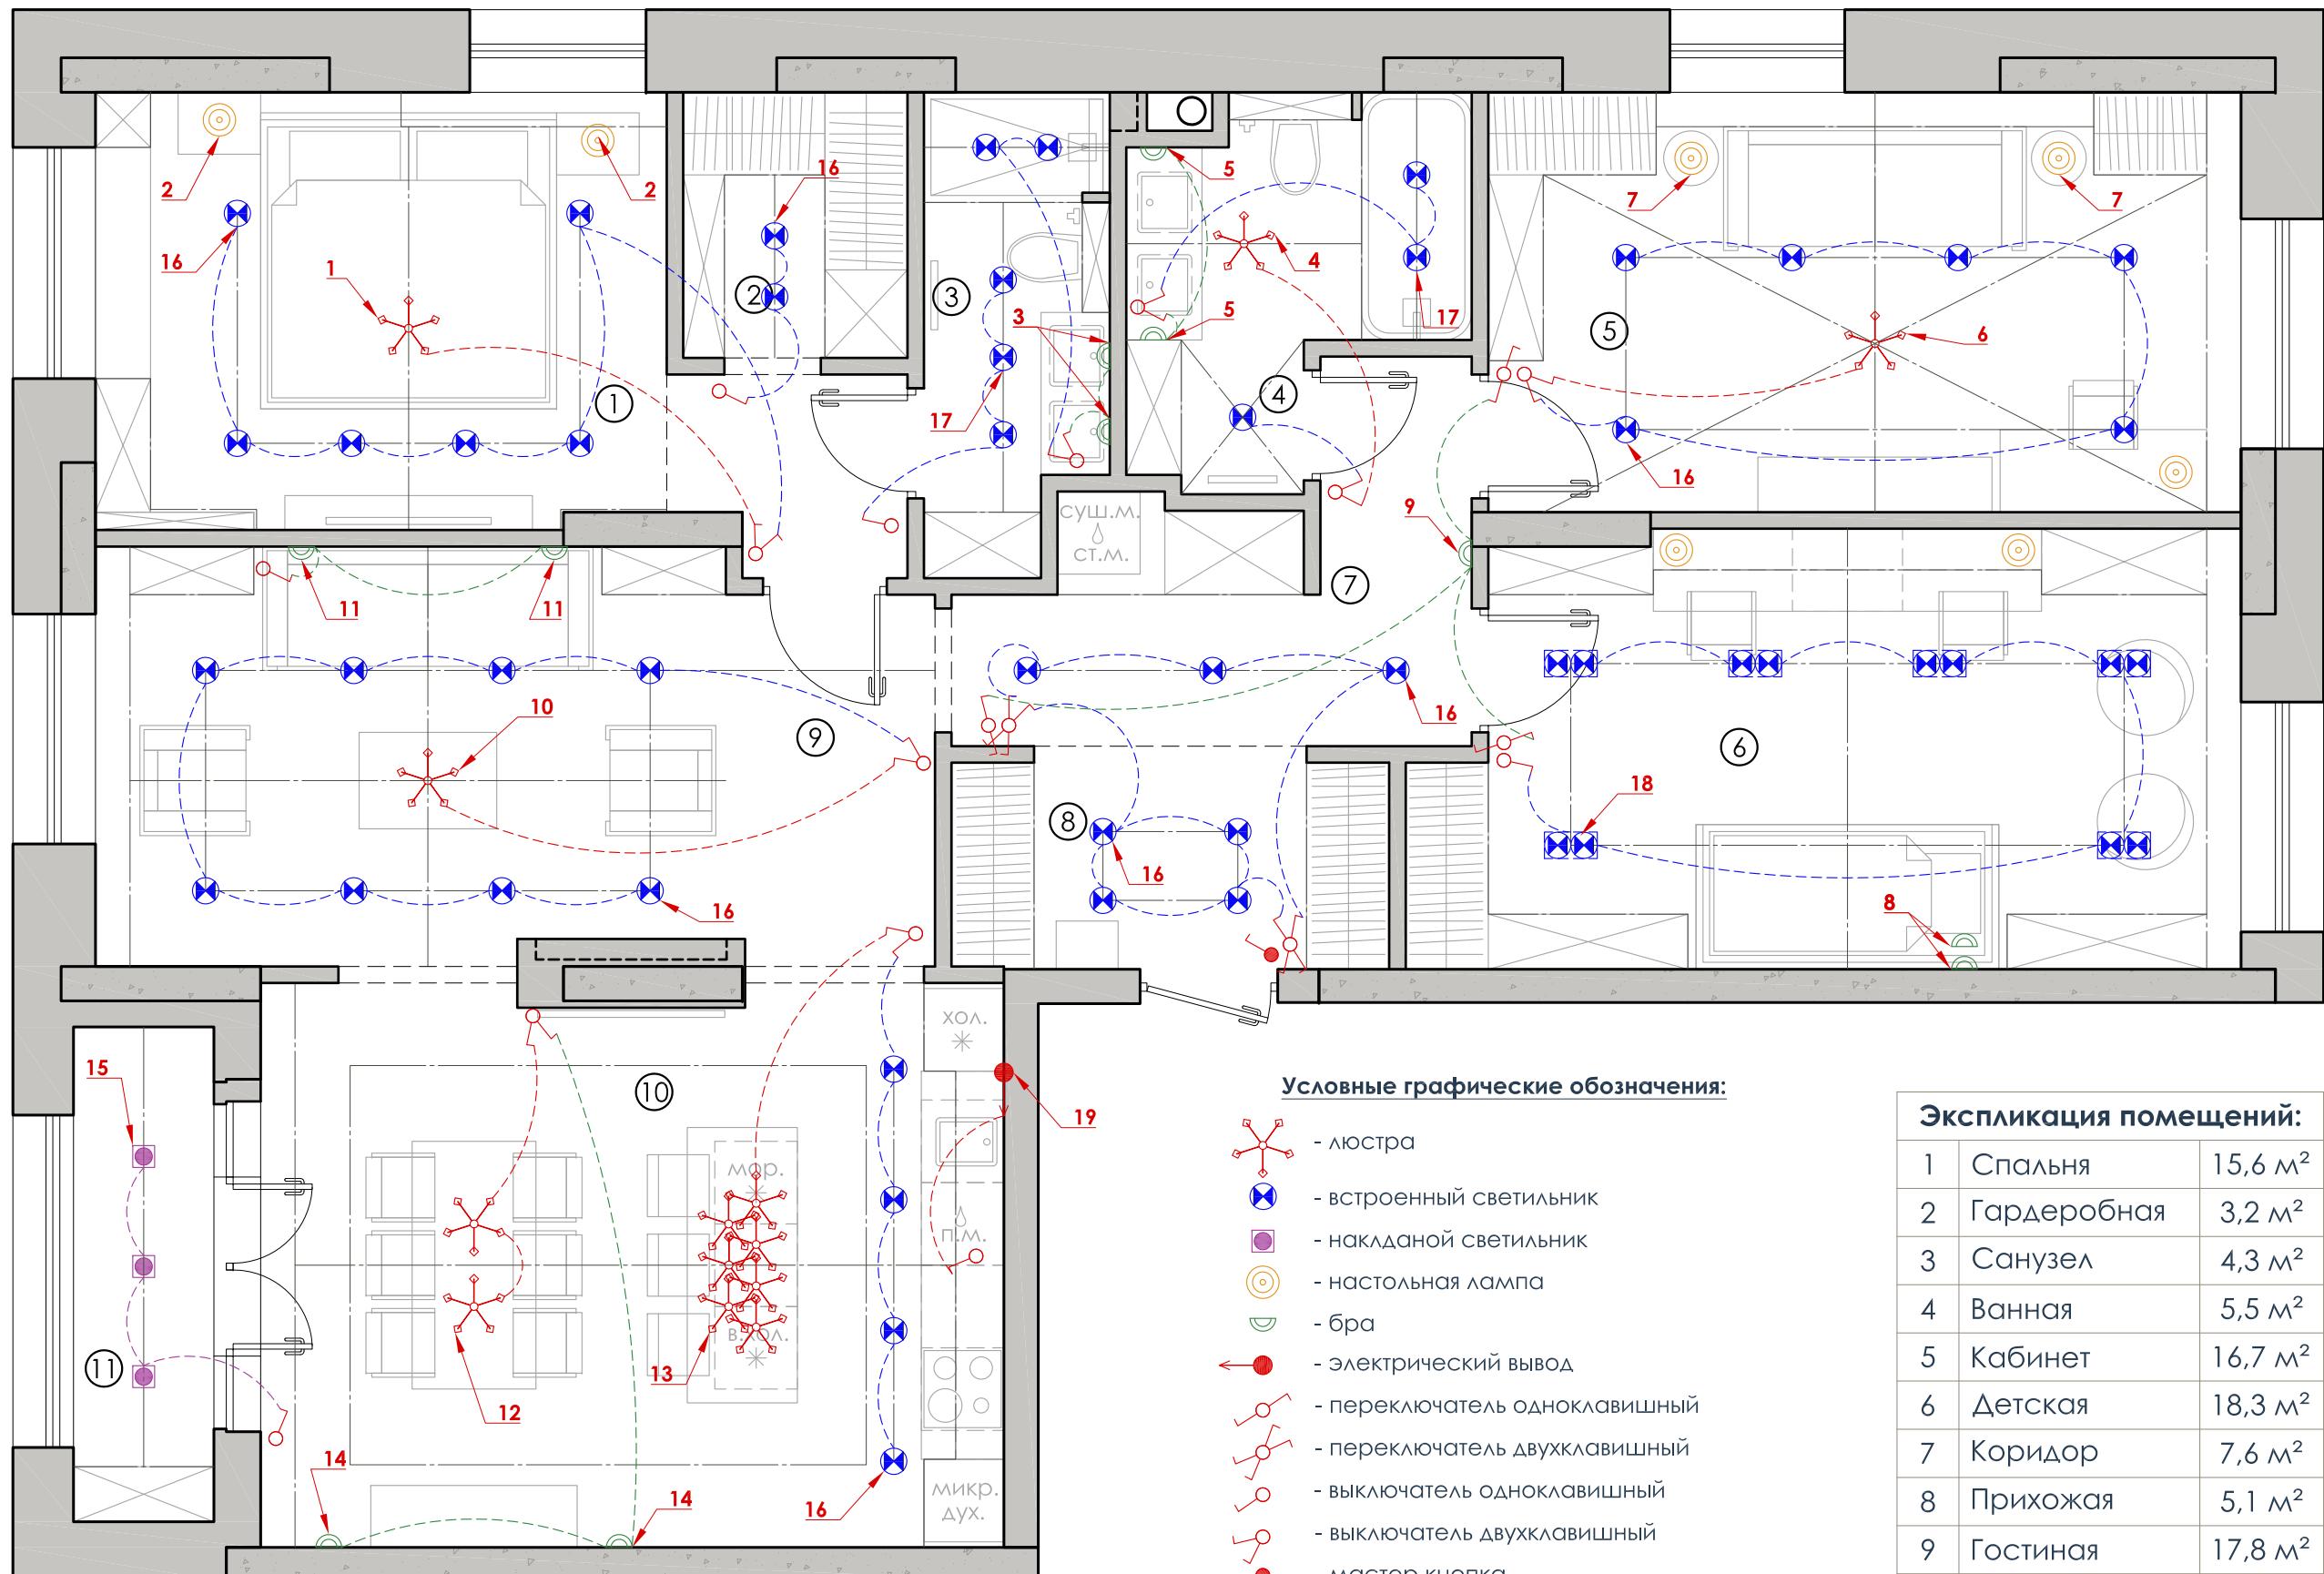

**Условные графические обозначения:**


- ❖ - люстра
- - встроенный светильник
- - накладной светильник
- - настольная лампа
- - бра
- ← - электрический вывод
- ↔ - переключатель одноклавишный
- ↔ - переключатель двухклавишный
- - выключатель одноклавишный
- - выключатель двухклавишный
- - мастер кнопка


**Примечание:**

1. Привязку выключателей см. развертки.
2. Местоположение бра уточнить с дизайнером.
3. Местоположение электрических выводов уточнить по месту с дизайнером.

<b>Экспликация помещений:</b>		
1	Спальня	15,6 м <sup>2</sup>
2	Гардеробная	3,2 м <sup>2</sup>
3	Санузел	4,3 м <sup>2</sup>
4	Ванная	5,5 м <sup>2</sup>
5	Кабинет	16,7 м <sup>2</sup>
6	Детская	18,3 м <sup>2</sup>
7	Коридор	7,6 м <sup>2</sup>
8	Прихожая	5,1 м <sup>2</sup>
9	Гостиная	17,8 м <sup>2</sup>
10	Кухня	22,6 м <sup>2</sup>
11	Балкон	3,9 м <sup>2</sup>

**Общая площадь: 120,6 м<sup>2</sup>**

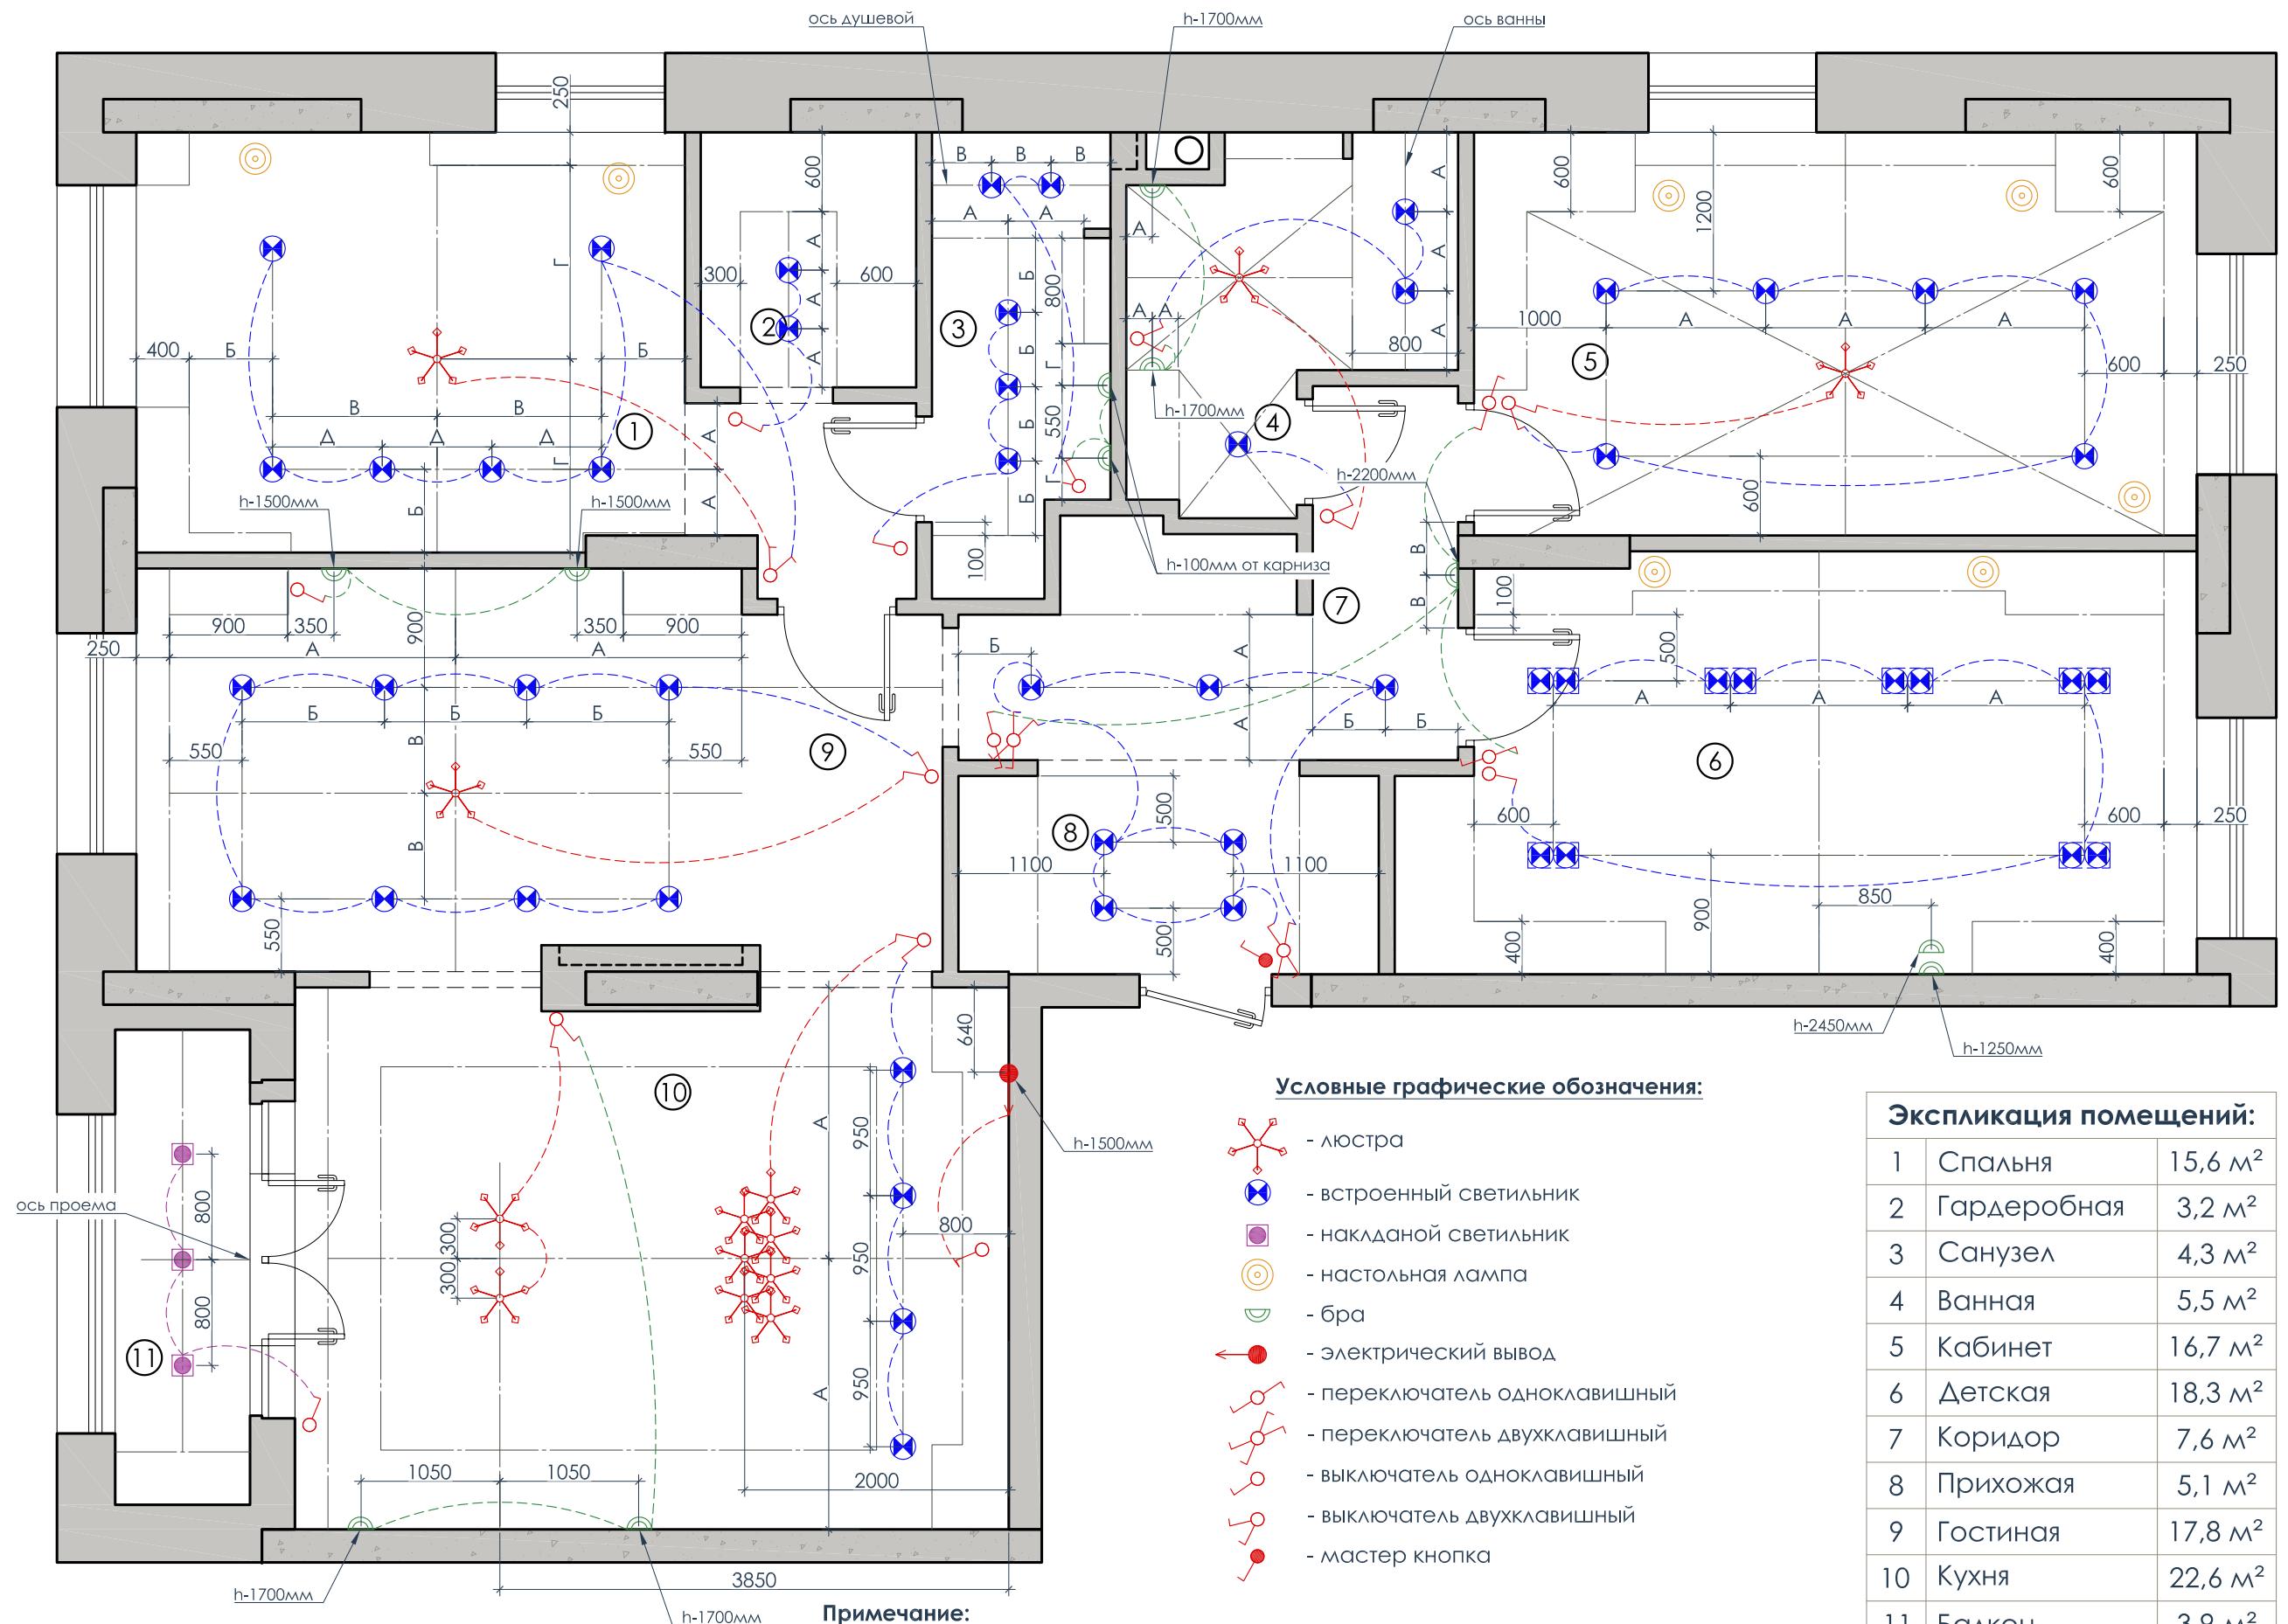

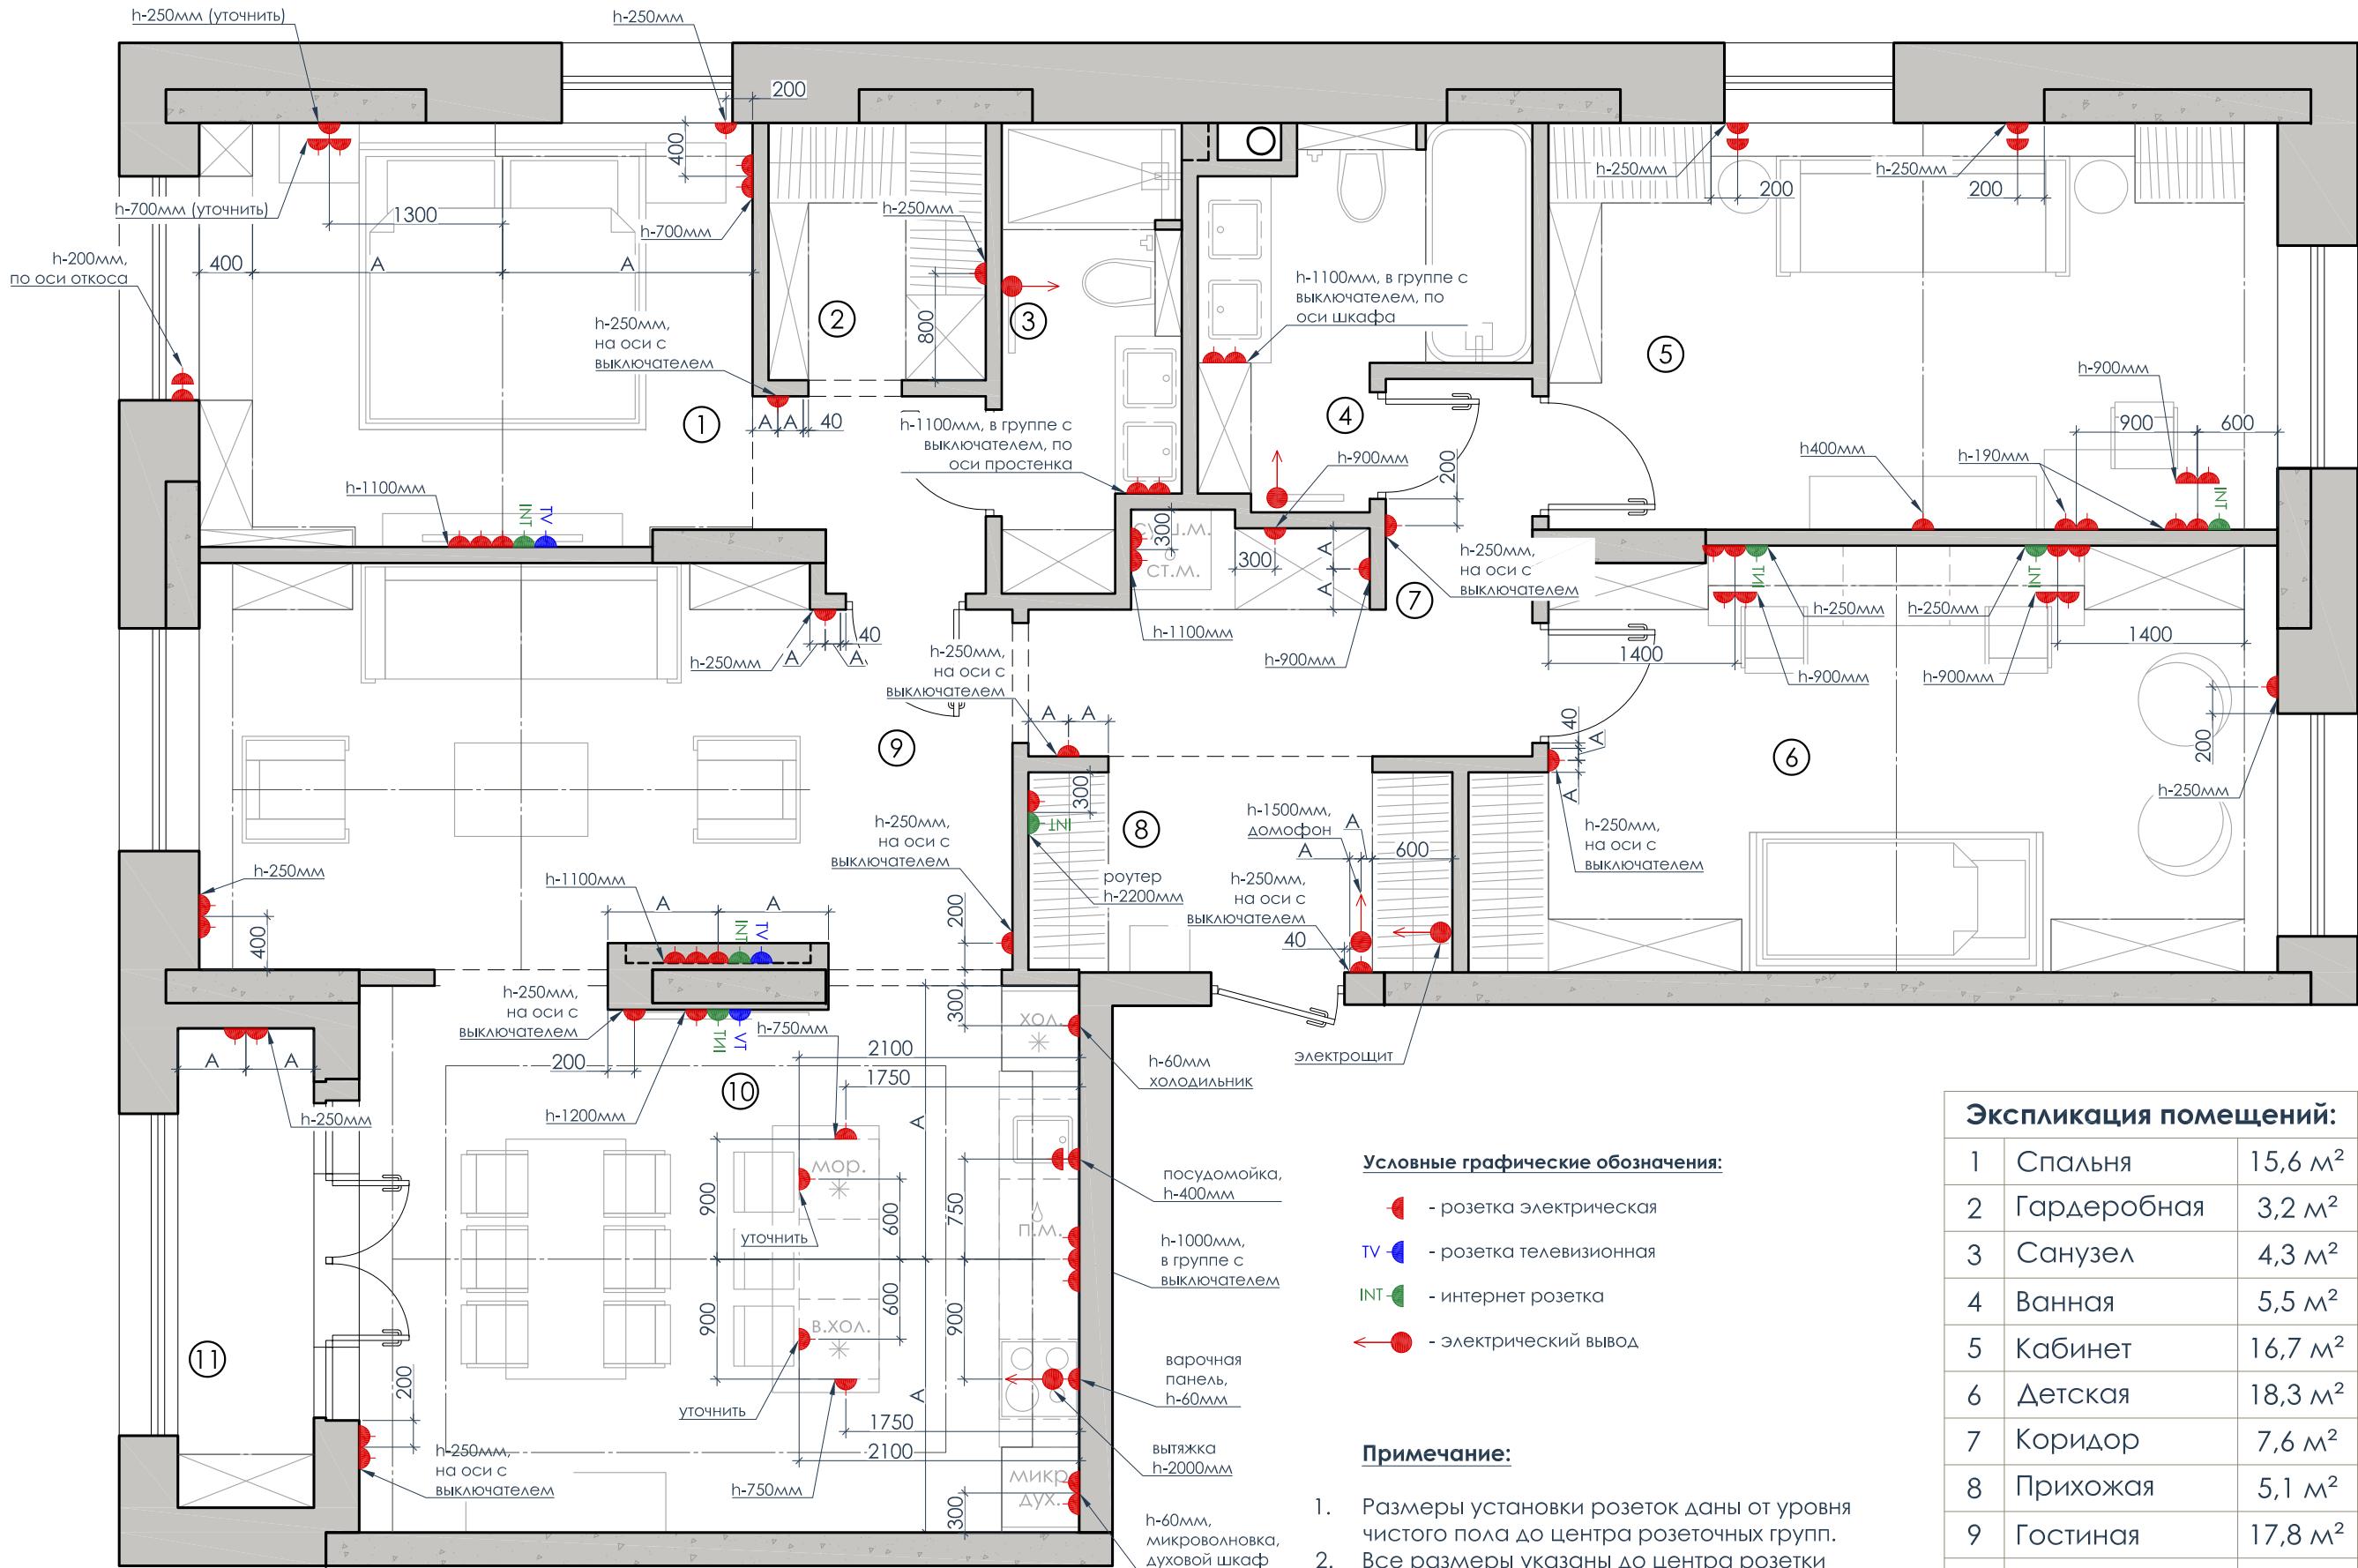

## Экспликация помещений:

1	Спальня	15,6 м <sup>2</sup>
2	Гардеробная	3,2 м <sup>2</sup>
3	Санузел	4,3 м <sup>2</sup>
4	Ванная	5,5 м <sup>2</sup>
5	Кабинет	16,7 м <sup>2</sup>
6	Детская	18,3 м <sup>2</sup>
7	Коридор	7,6 м <sup>2</sup>
8	Прихожая	5,1 м <sup>2</sup>
9	Гостиная	17,8 м <sup>2</sup>
10	Кухня	22,6 м <sup>2</sup>
11	Балкон	3,9 м <sup>2</sup>


Общая площадь: 120,6 м<sup>2</sup>


## Условные графические обозначения

- розетка электрическая
  - TV - розетка телевизионная
  - INT - интернет розетка
  - ← - электрический вывод

## Примечани


1. Размеры установки розеток даны от уровня чистого пола до центра розеточных групп.
  2. Все размеры указаны до центра розетки или розеточной группы.
  3. Все розетки располагать в единой группе с выключателями (где это необходимо).

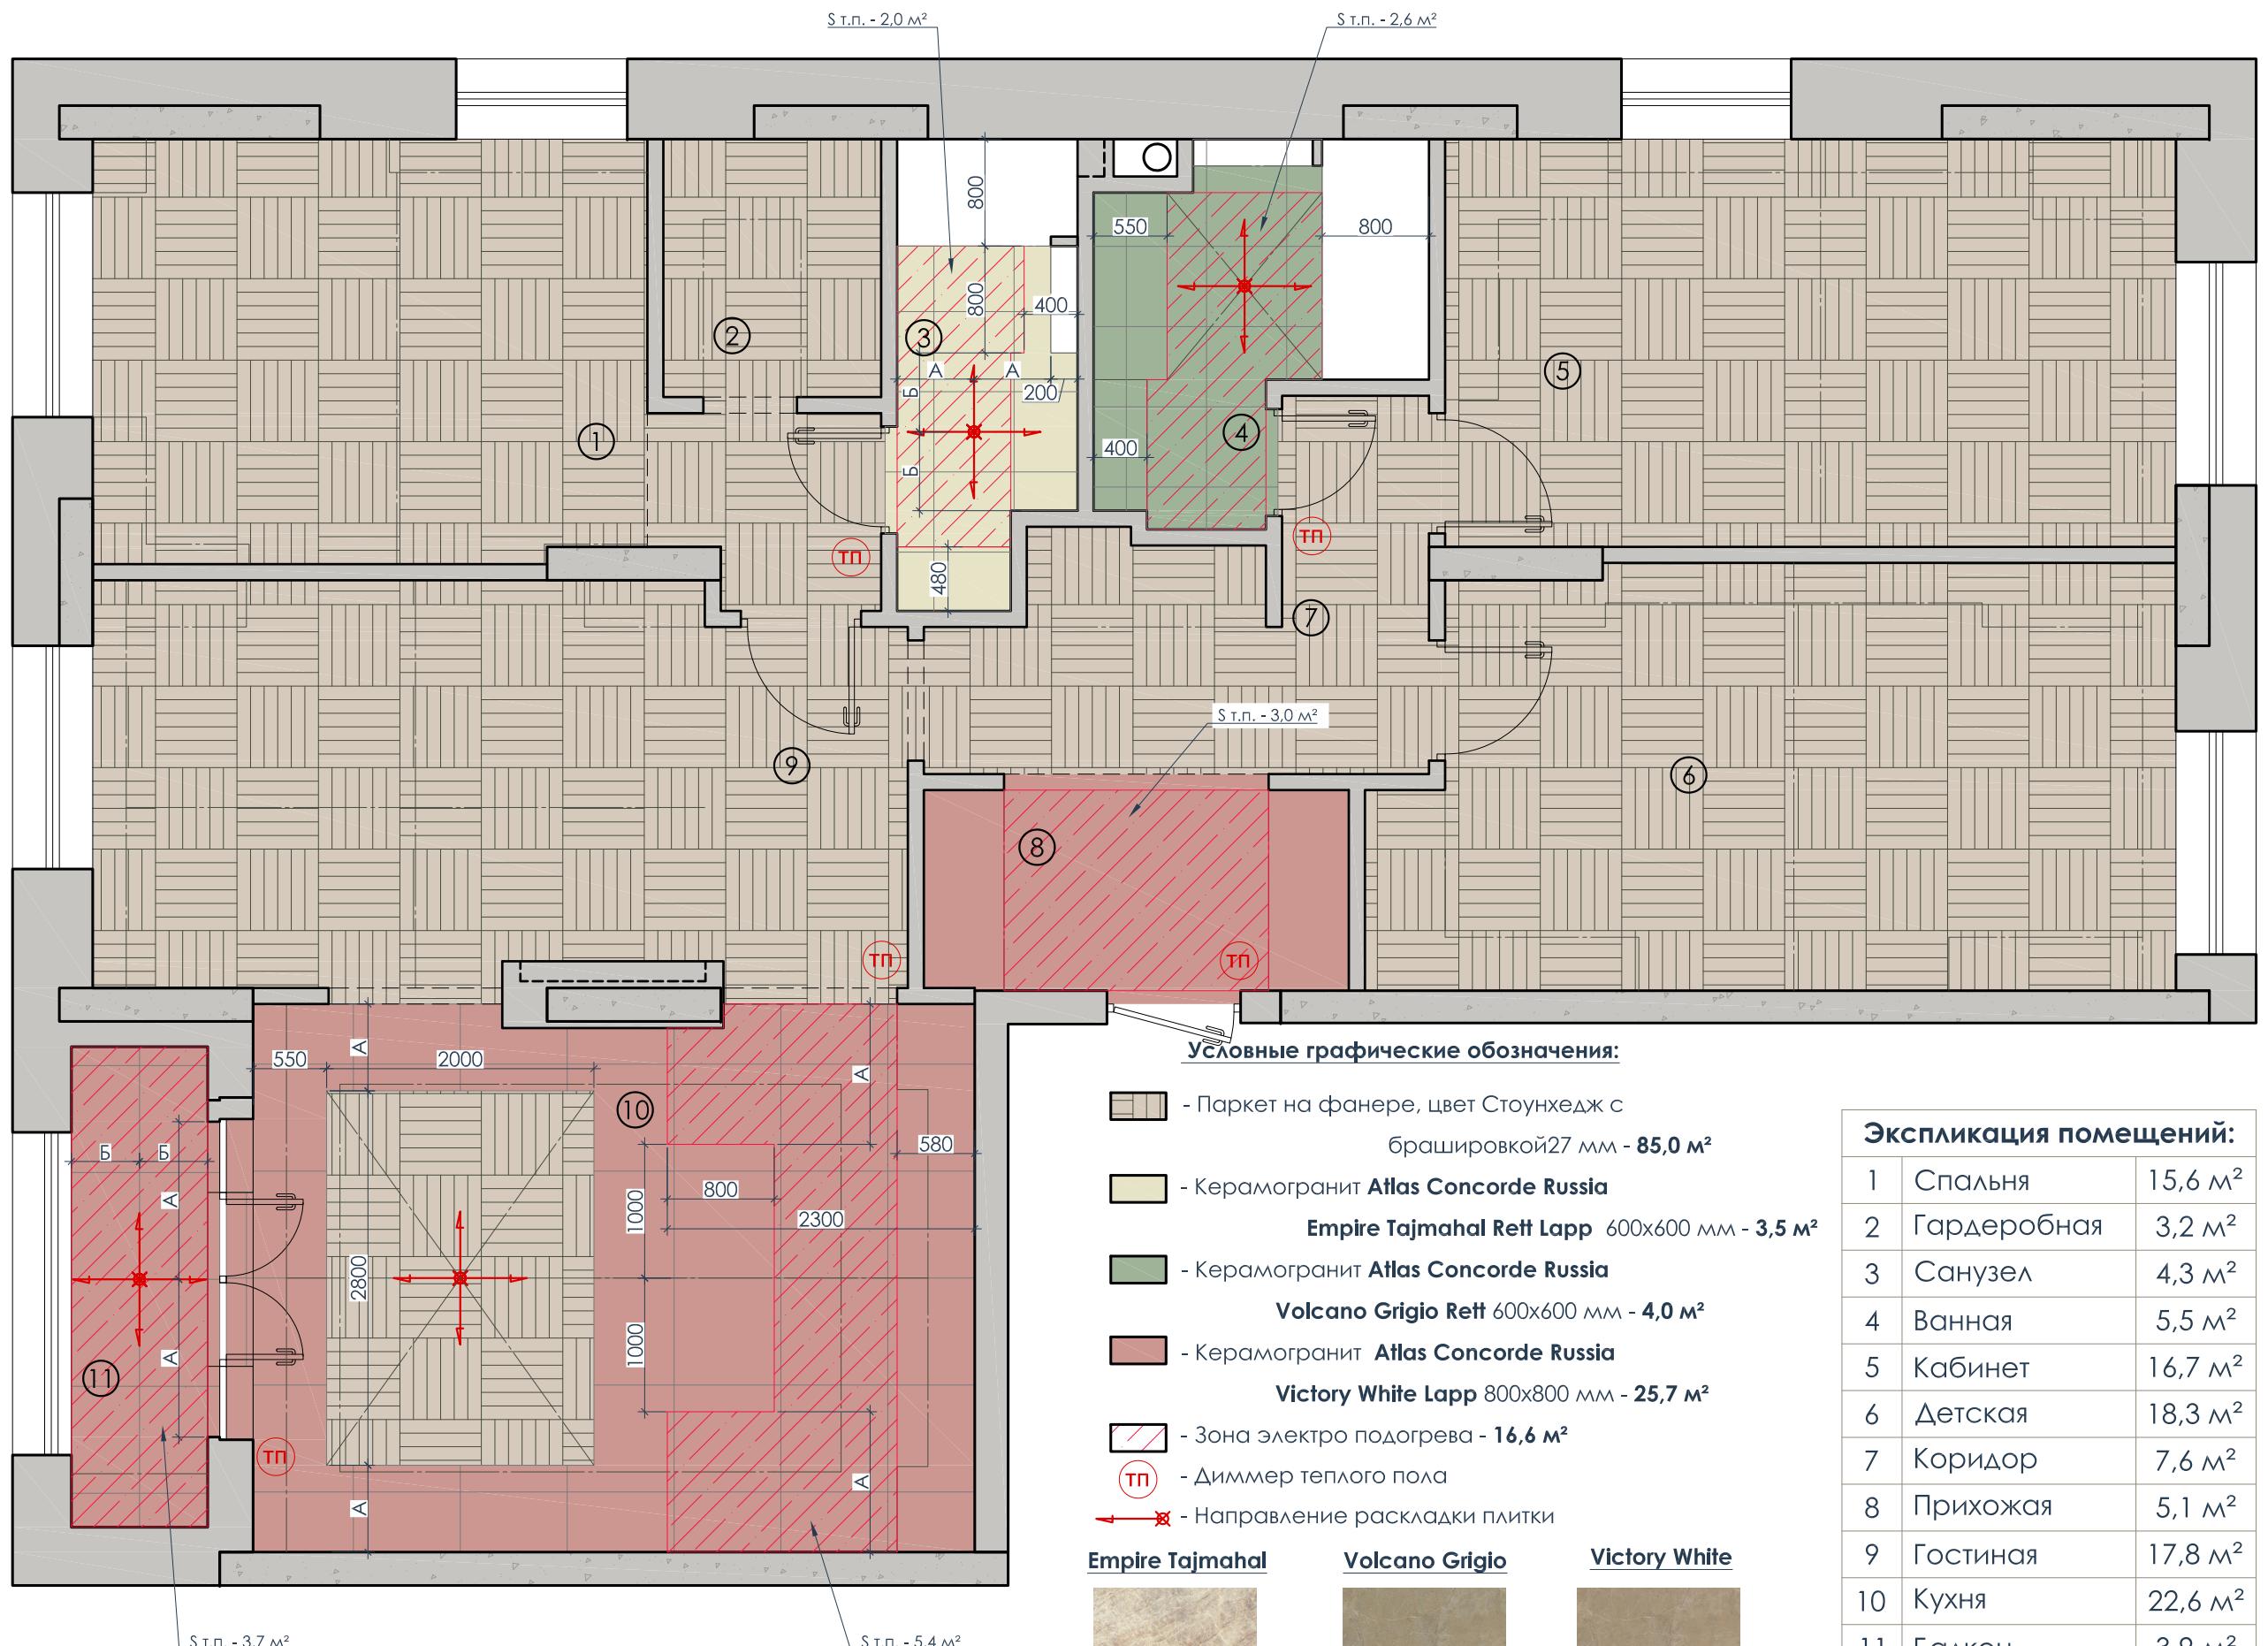

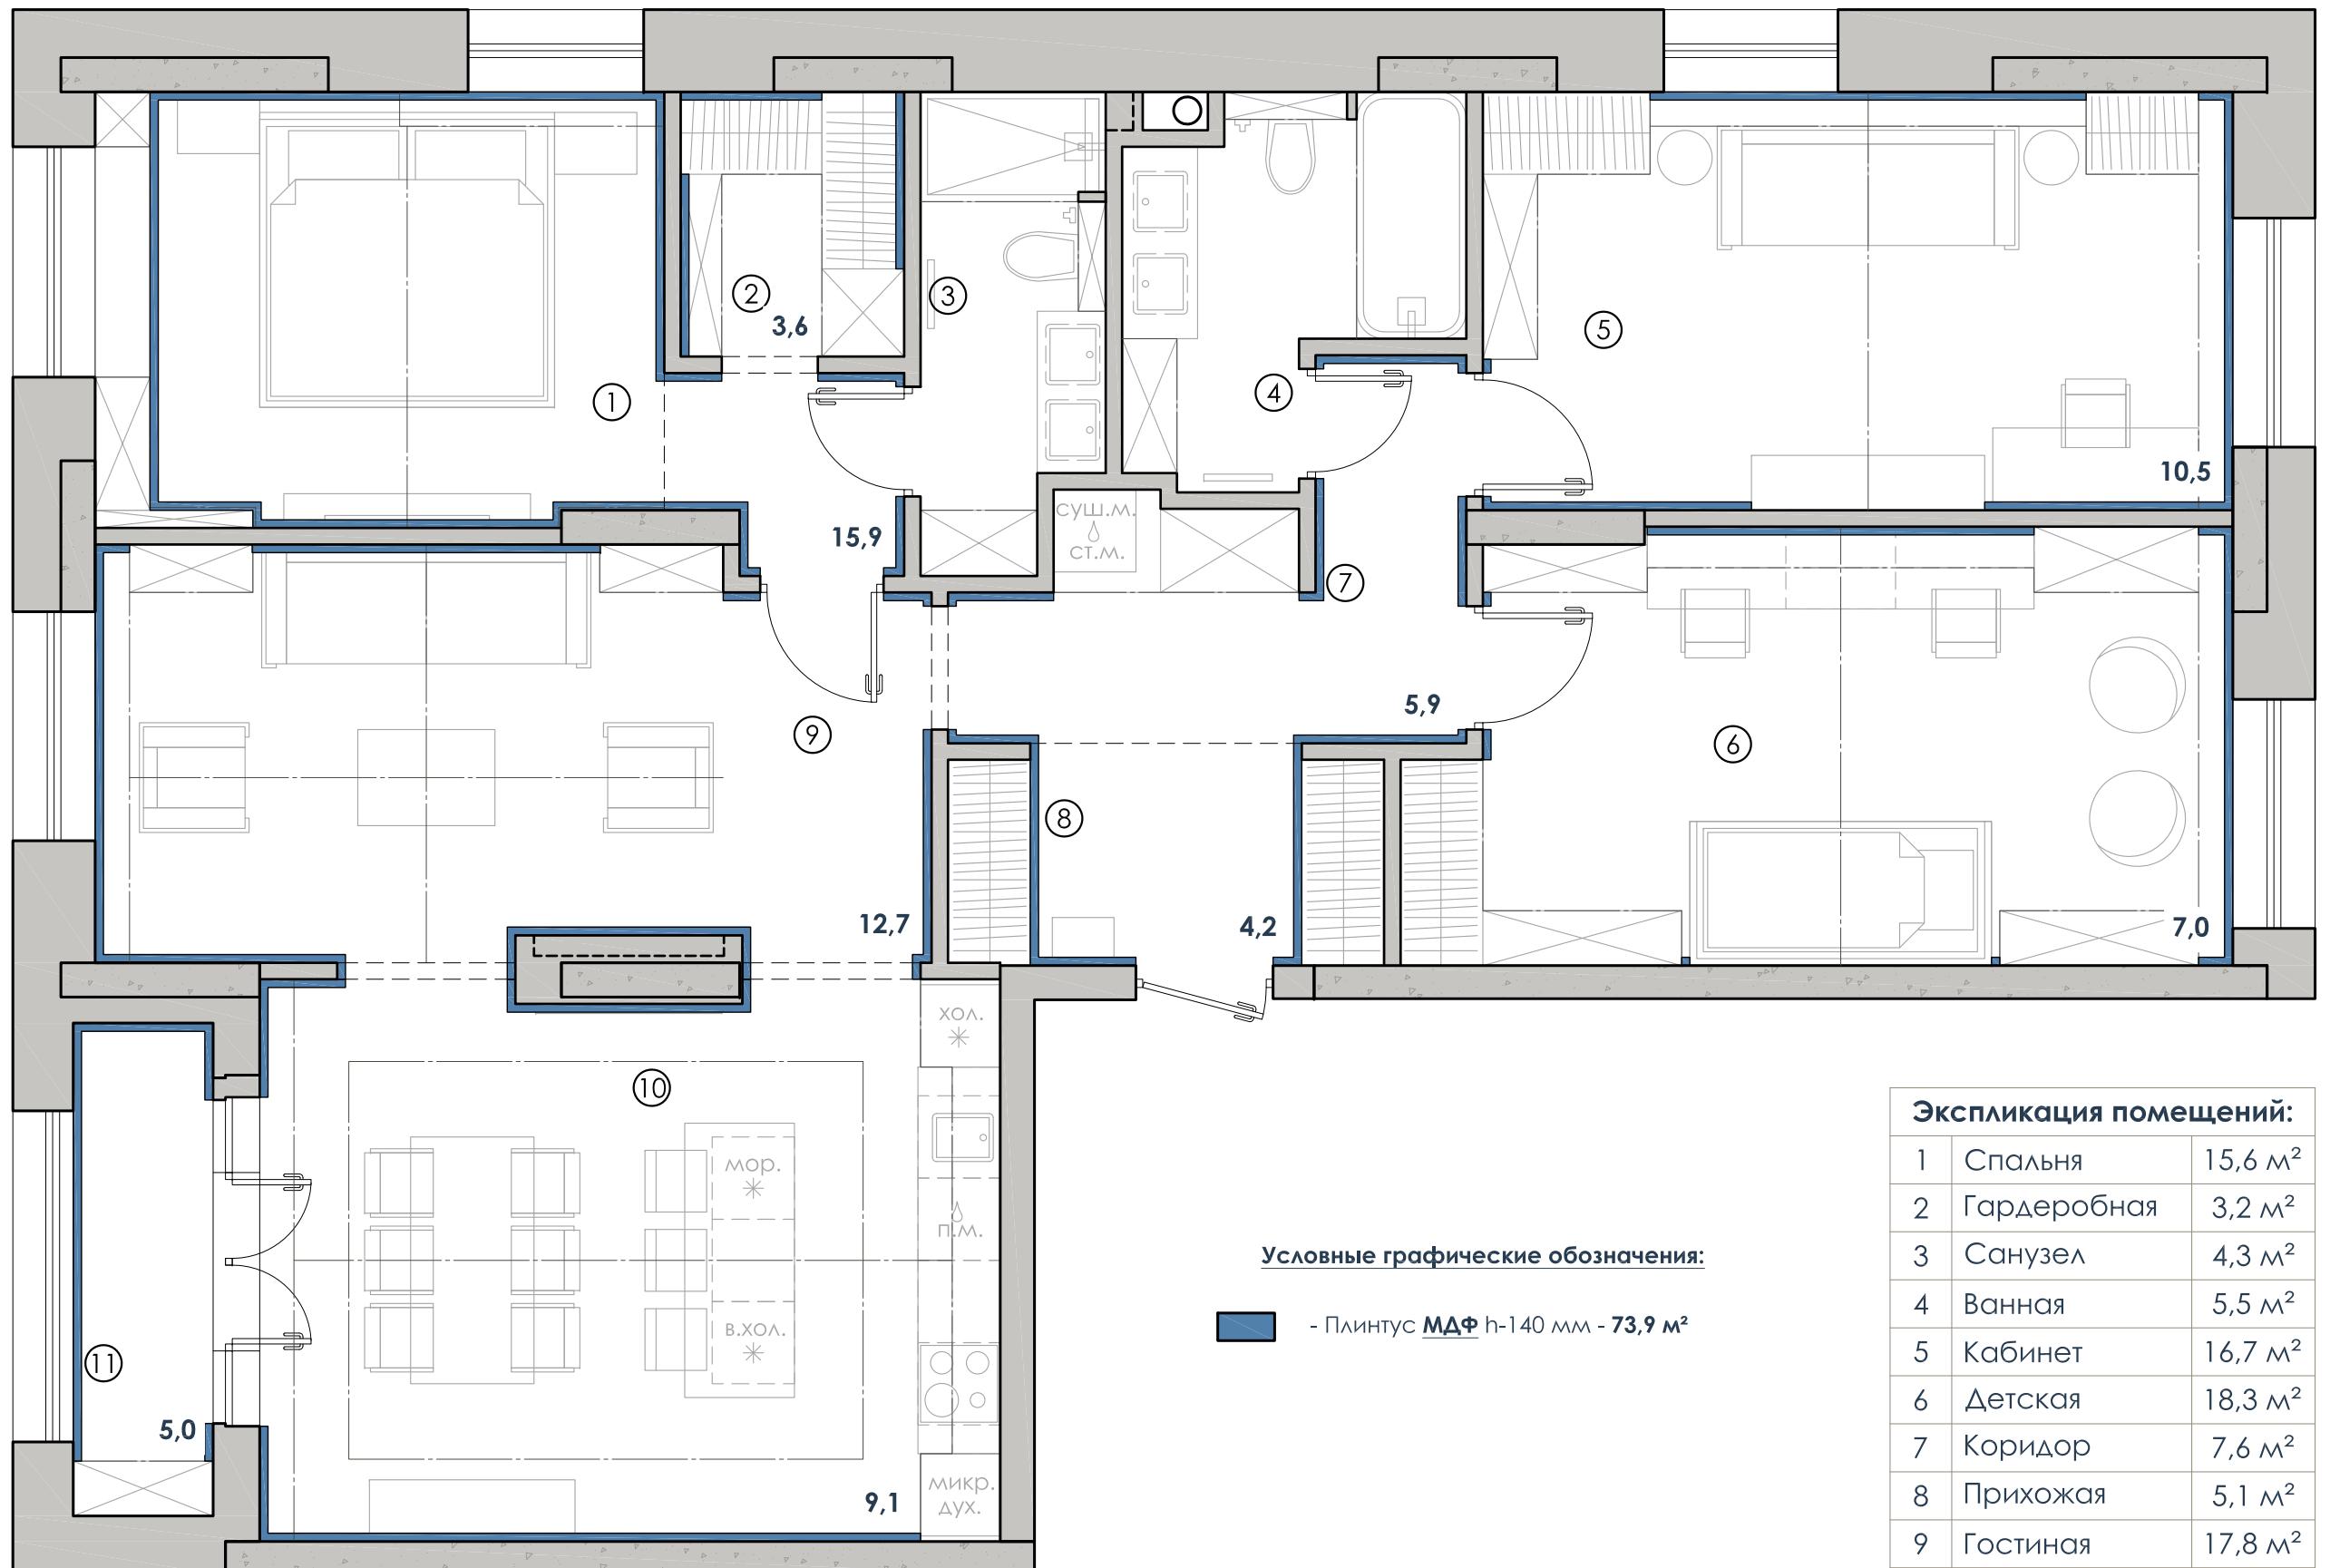

Экспликация помещений:		
1	Спальня	15,6 м <sup>2</sup>
2	Гардеробная	3,2 м <sup>2</sup>
3	Санузел	4,3 м <sup>2</sup>
4	Ванная	5,5 м <sup>2</sup>
5	Кабинет	16,7 м <sup>2</sup>
6	Детская	18,3 м <sup>2</sup>
7	Коридор	7,6 м <sup>2</sup>
8	Прихожая	5,1 м <sup>2</sup>
9	Гостиная	17,8 м <sup>2</sup>
10	Кухня	22,6 м <sup>2</sup>
11	Балкон	3,9 м <sup>2</sup>
Общая площадь: 120,6 м <sup>2</sup>		

### План раскладки плинтуса.

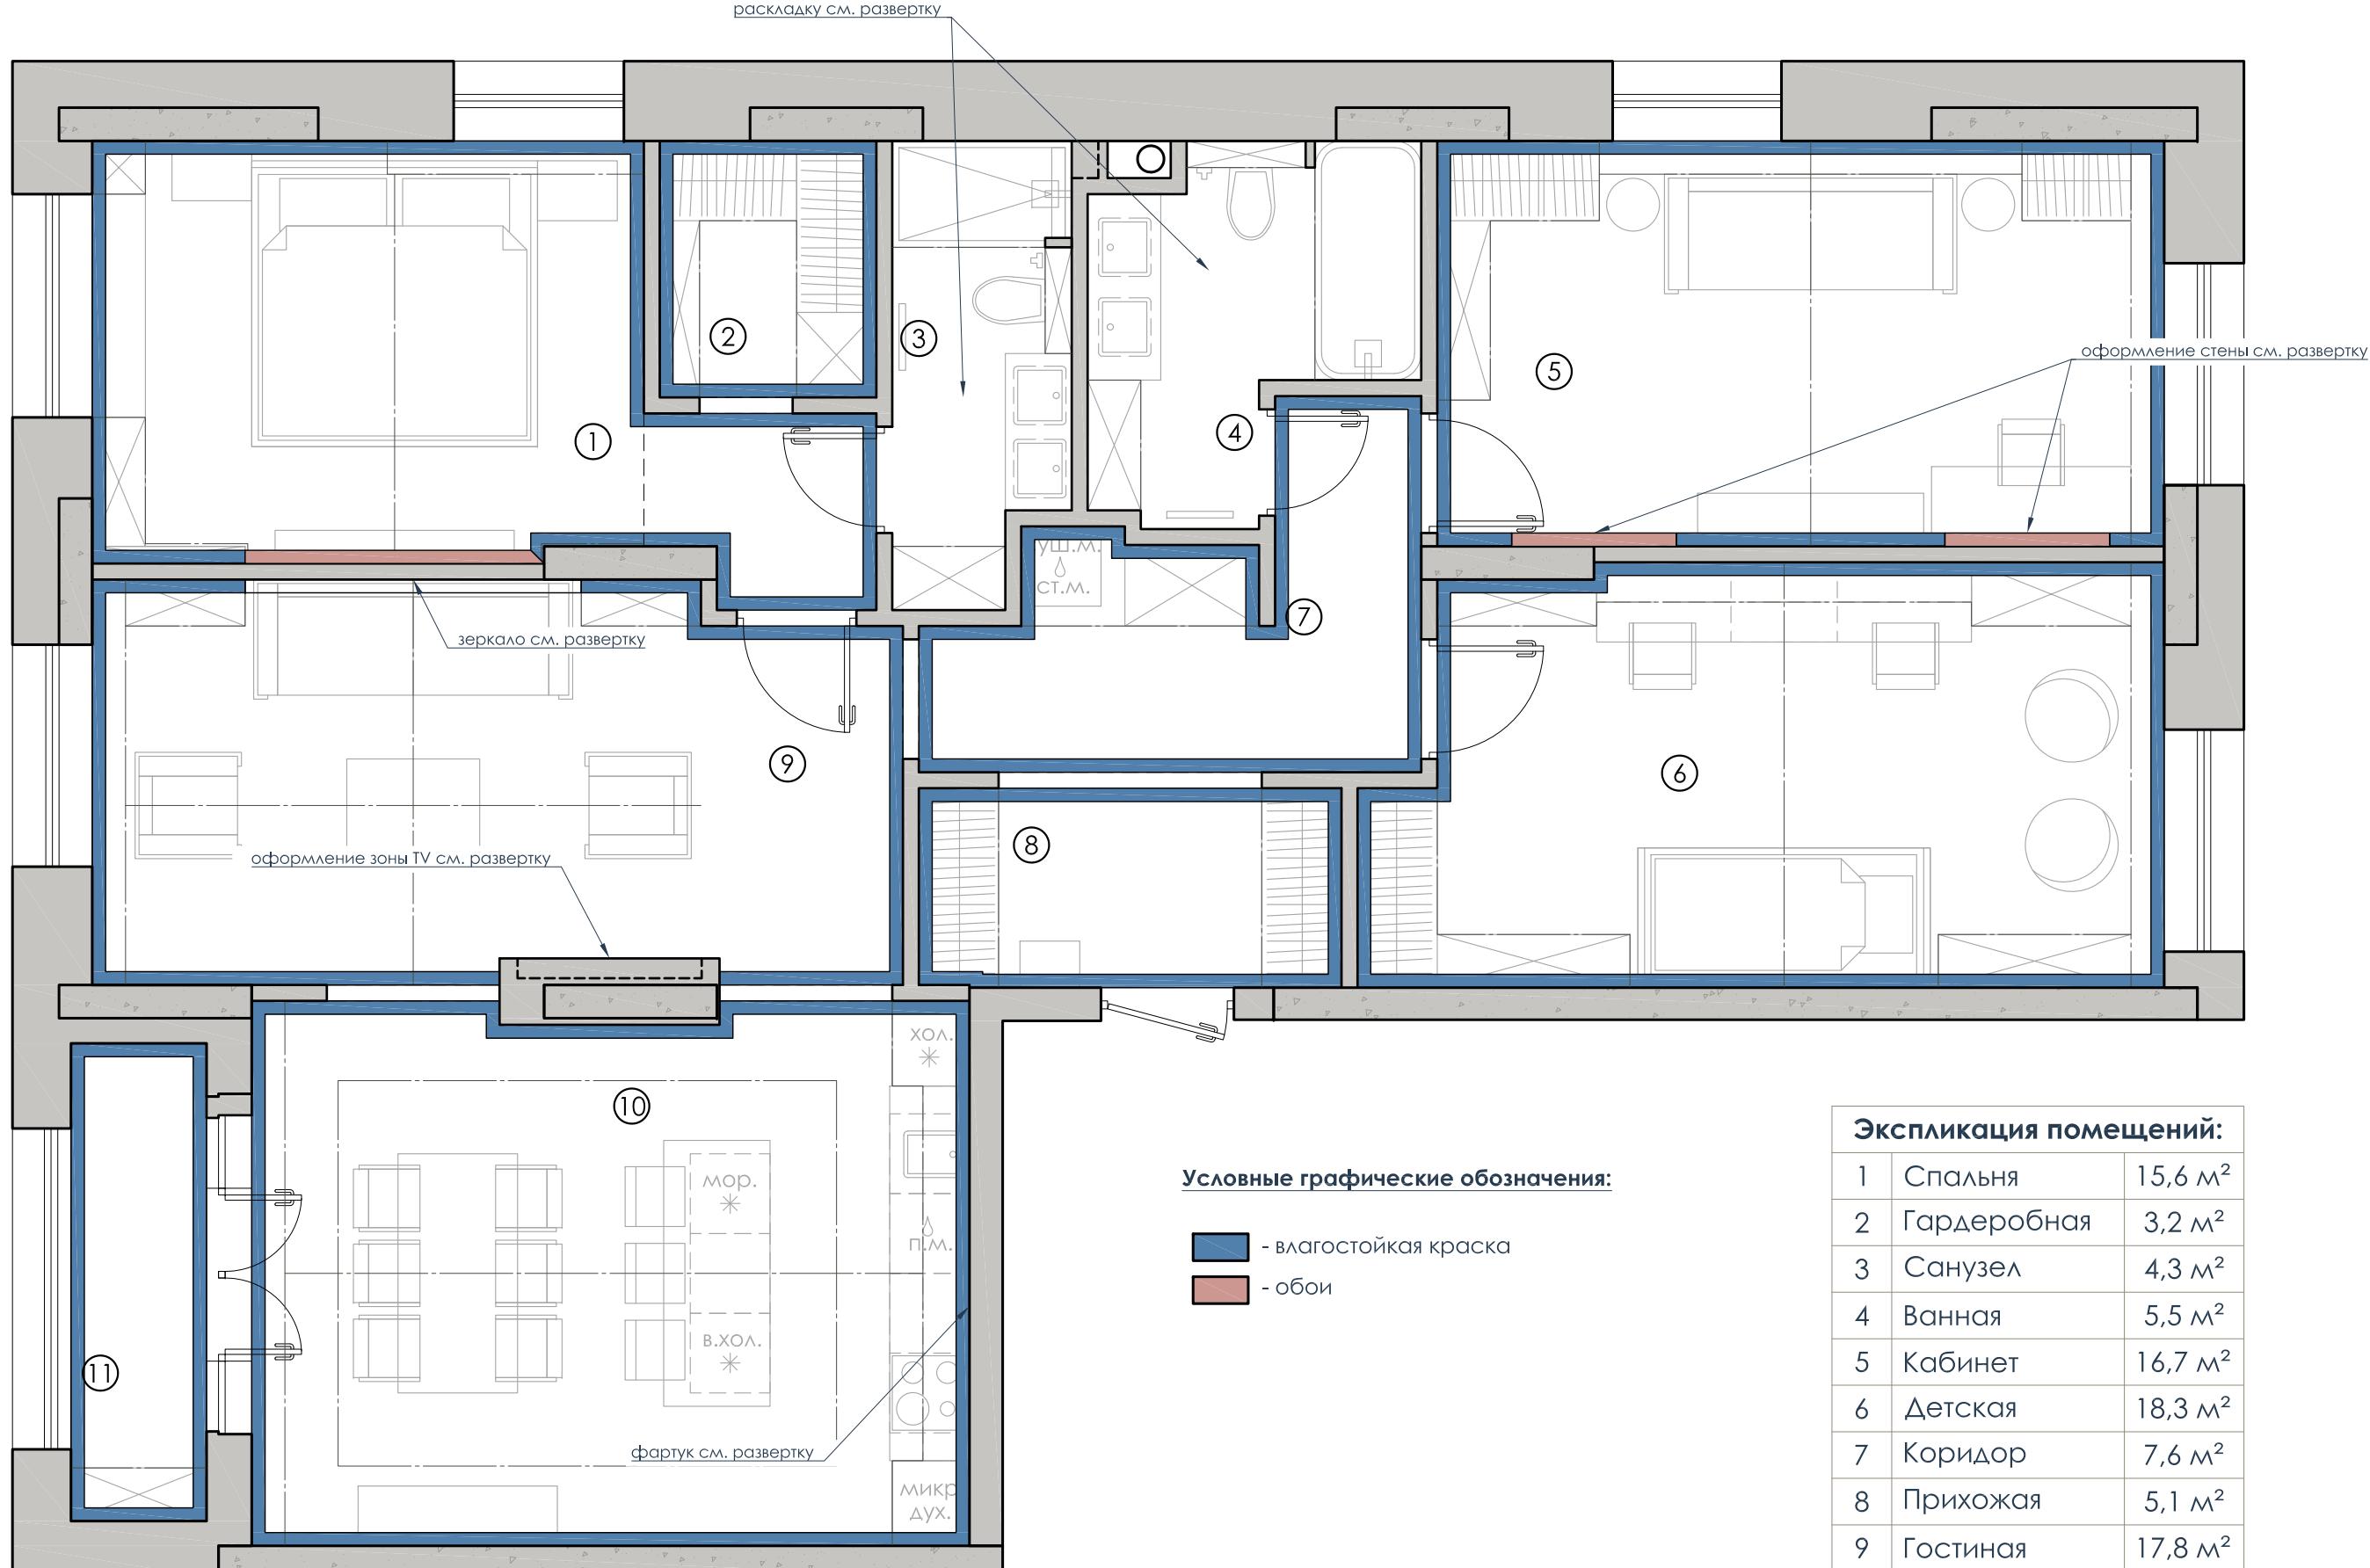


**Условные графические обозначения:**


- - влагостойкая краска
- - обои

**Экспликация помещений:**

1	Спальня	15,6 м <sup>2</sup>
2	Гардеробная	3,2 м <sup>2</sup>
3	Санузел	4,3 м <sup>2</sup>
4	Ванная	5,5 м <sup>2</sup>
5	Кабинет	16,7 м <sup>2</sup>
6	Детская	18,3 м <sup>2</sup>
7	Коридор	7,6 м <sup>2</sup>
8	Прихожая	5,1 м <sup>2</sup>
9	Гостиная	17,8 м <sup>2</sup>
10	Кухня	22,6 м <sup>2</sup>
11	Балкон	3,9 м <sup>2</sup>

**Общая площадь: 120,6 м<sup>2</sup>**

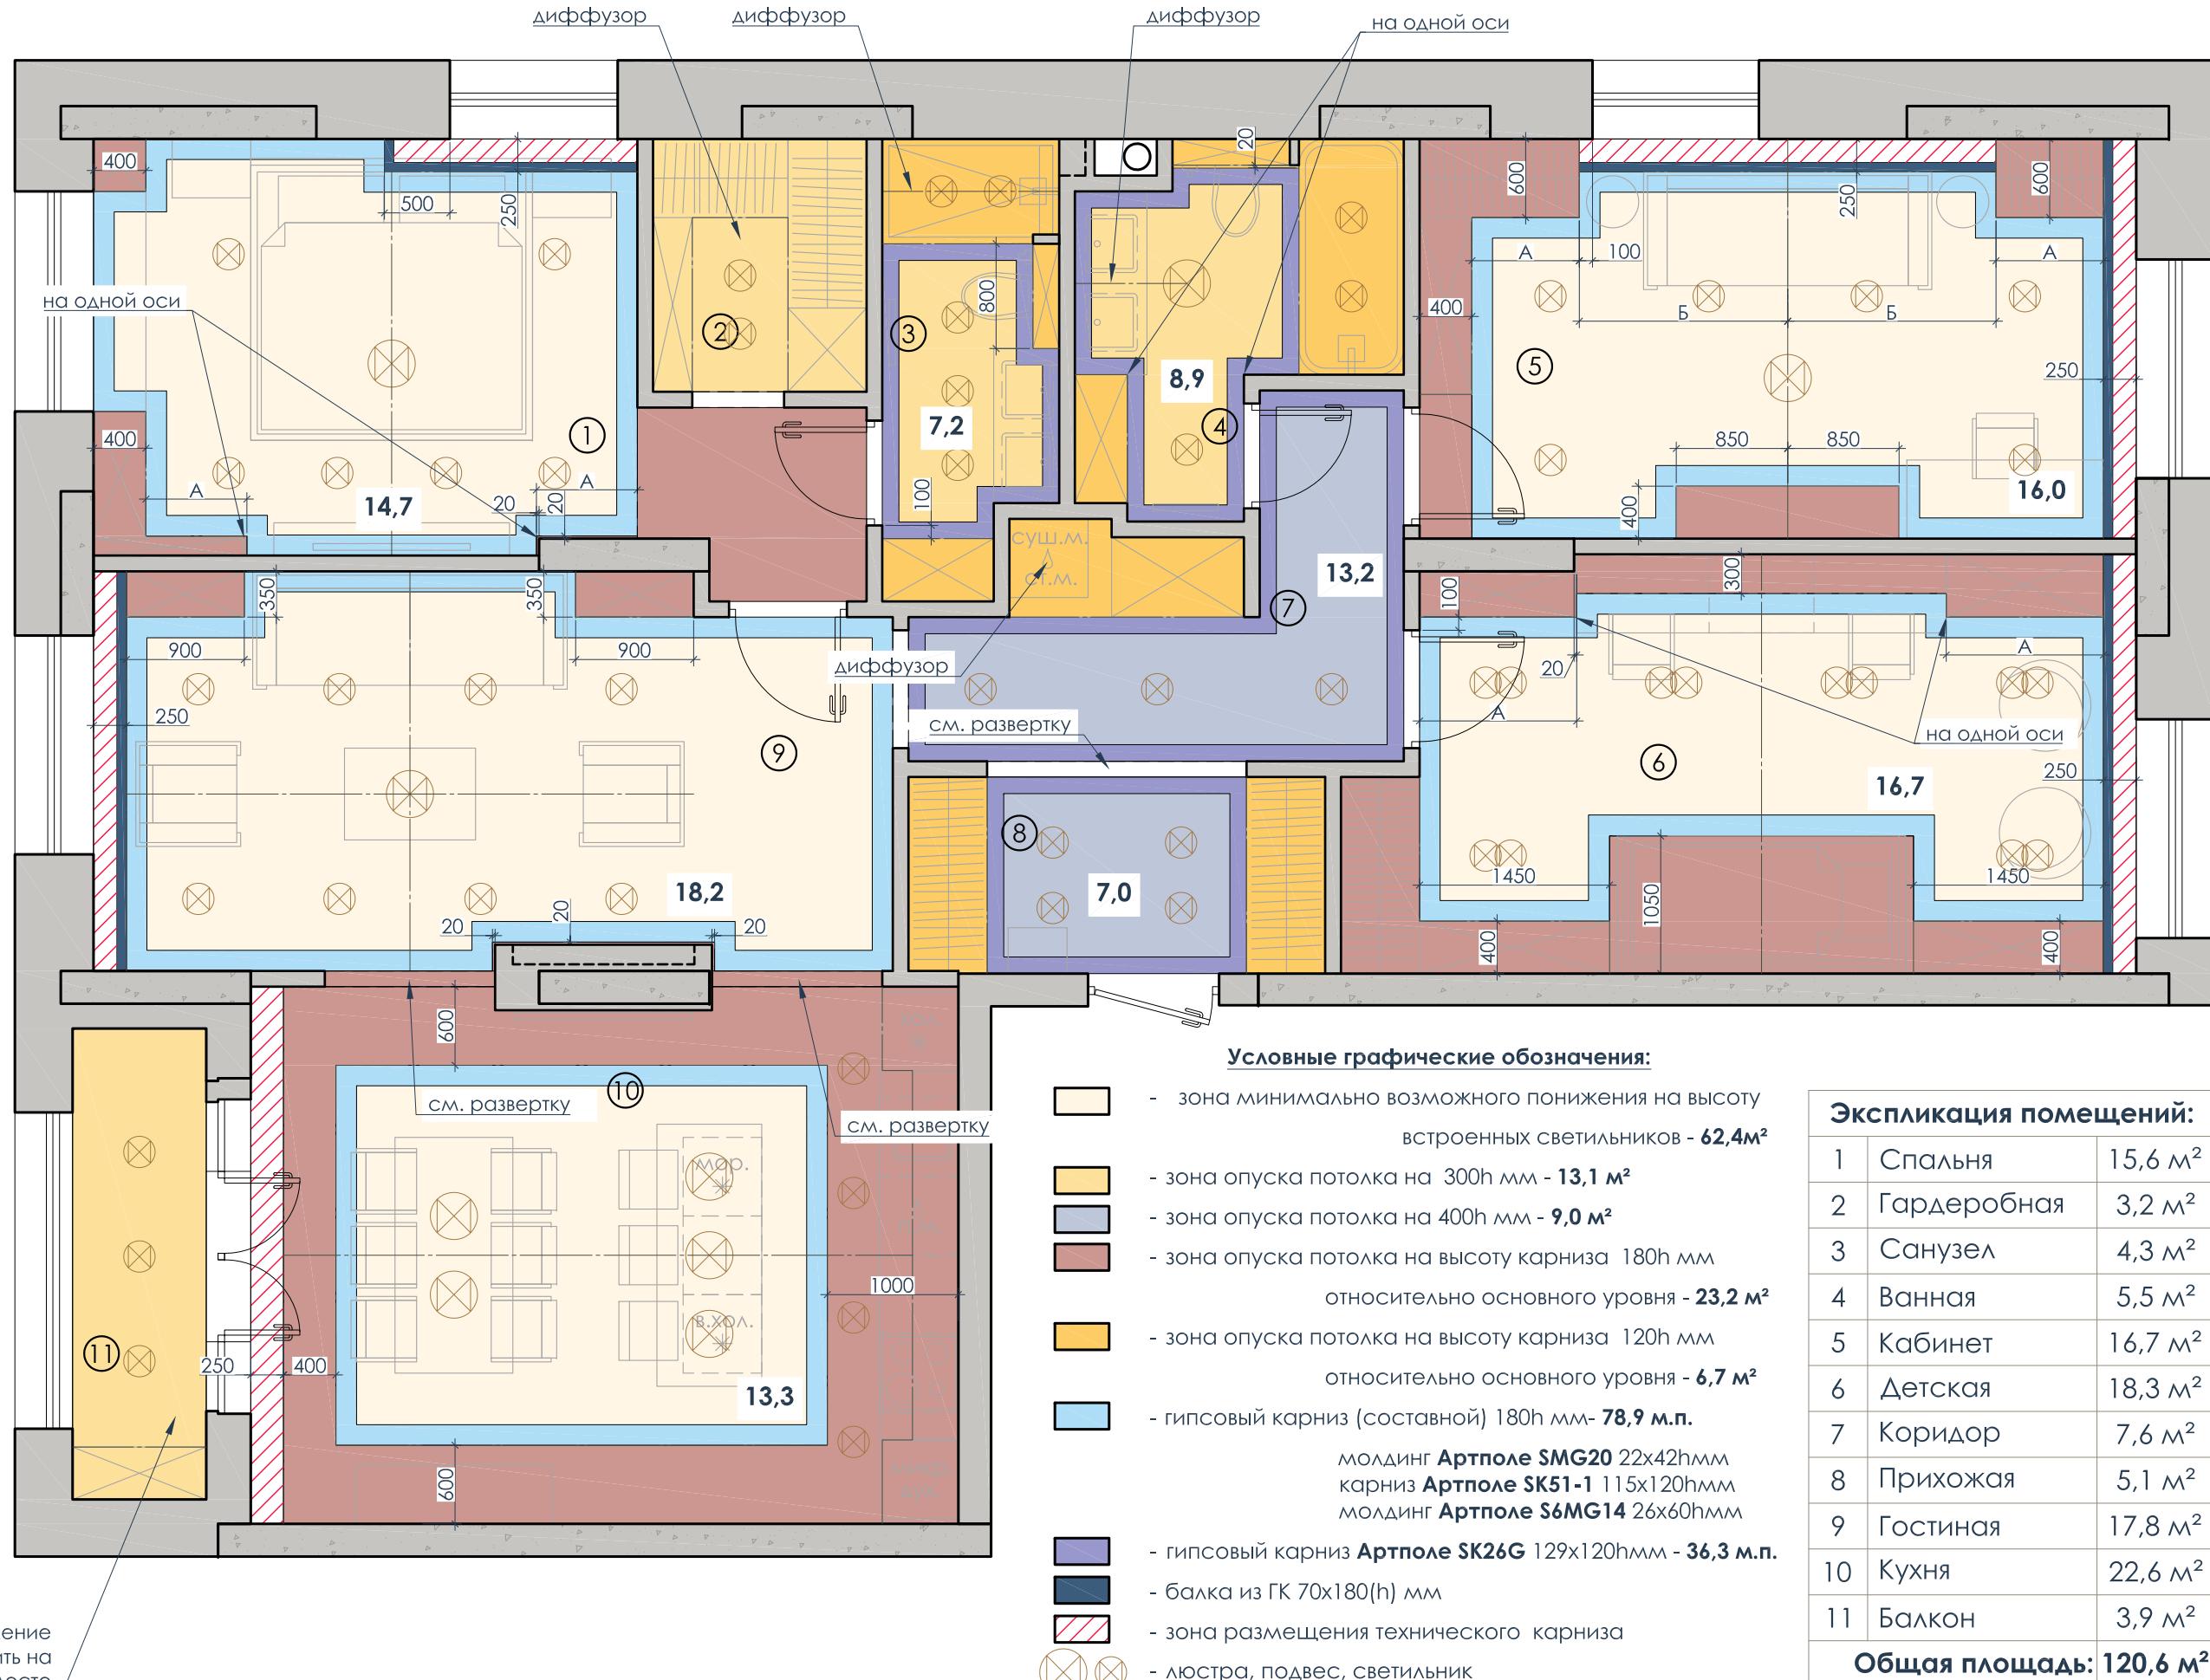


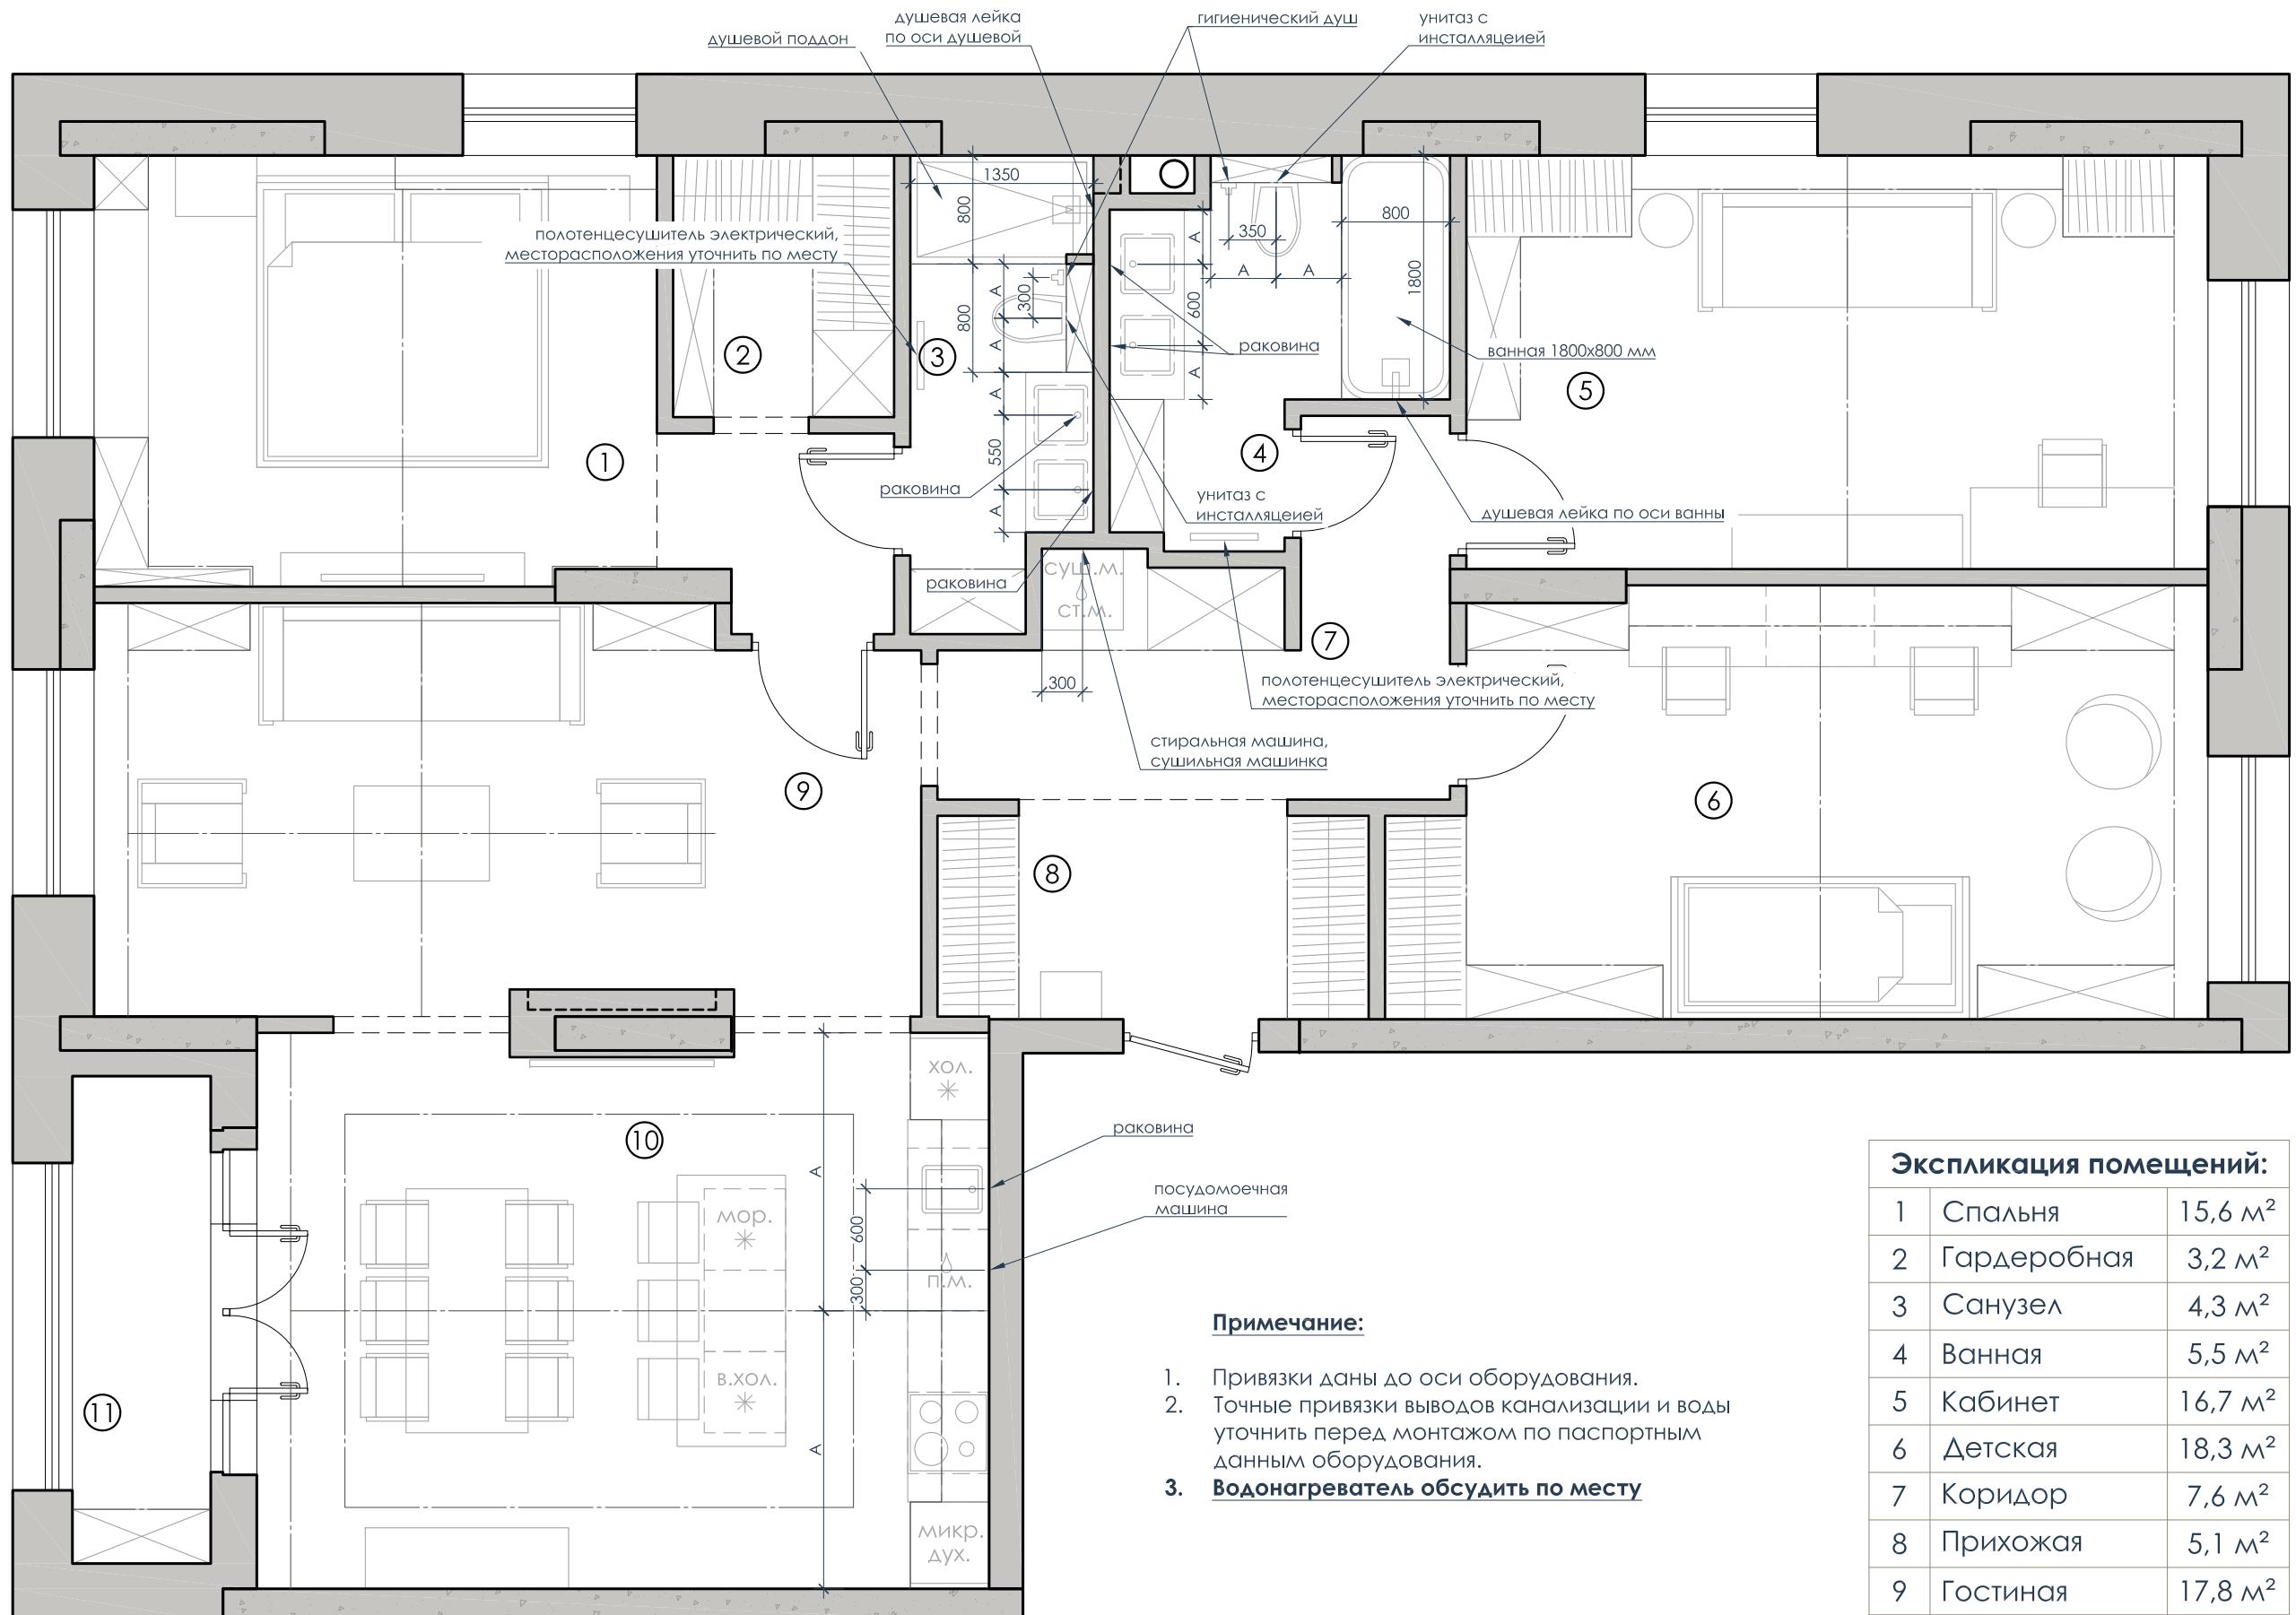


## Экспликация помещений:

1	Спальня	15,6 м <sup>2</sup>
2	Гардеробная	3,2 м <sup>2</sup>
3	Санузел	4,3 м <sup>2</sup>
4	Ванная	5,5 м <sup>2</sup>
5	Кабинет	16,7 м <sup>2</sup>
6	Детская	18,3 м <sup>2</sup>
7	Коридор	7,6 м <sup>2</sup>
8	Прихожая	5,1 м <sup>2</sup>
9	Гостиная	17,8 м <sup>2</sup>
10	Кухня	22,6 м <sup>2</sup>
11	Балкон	3,9 м <sup>2</sup>






Общая площадь: 120,6 м<sup>2</sup>


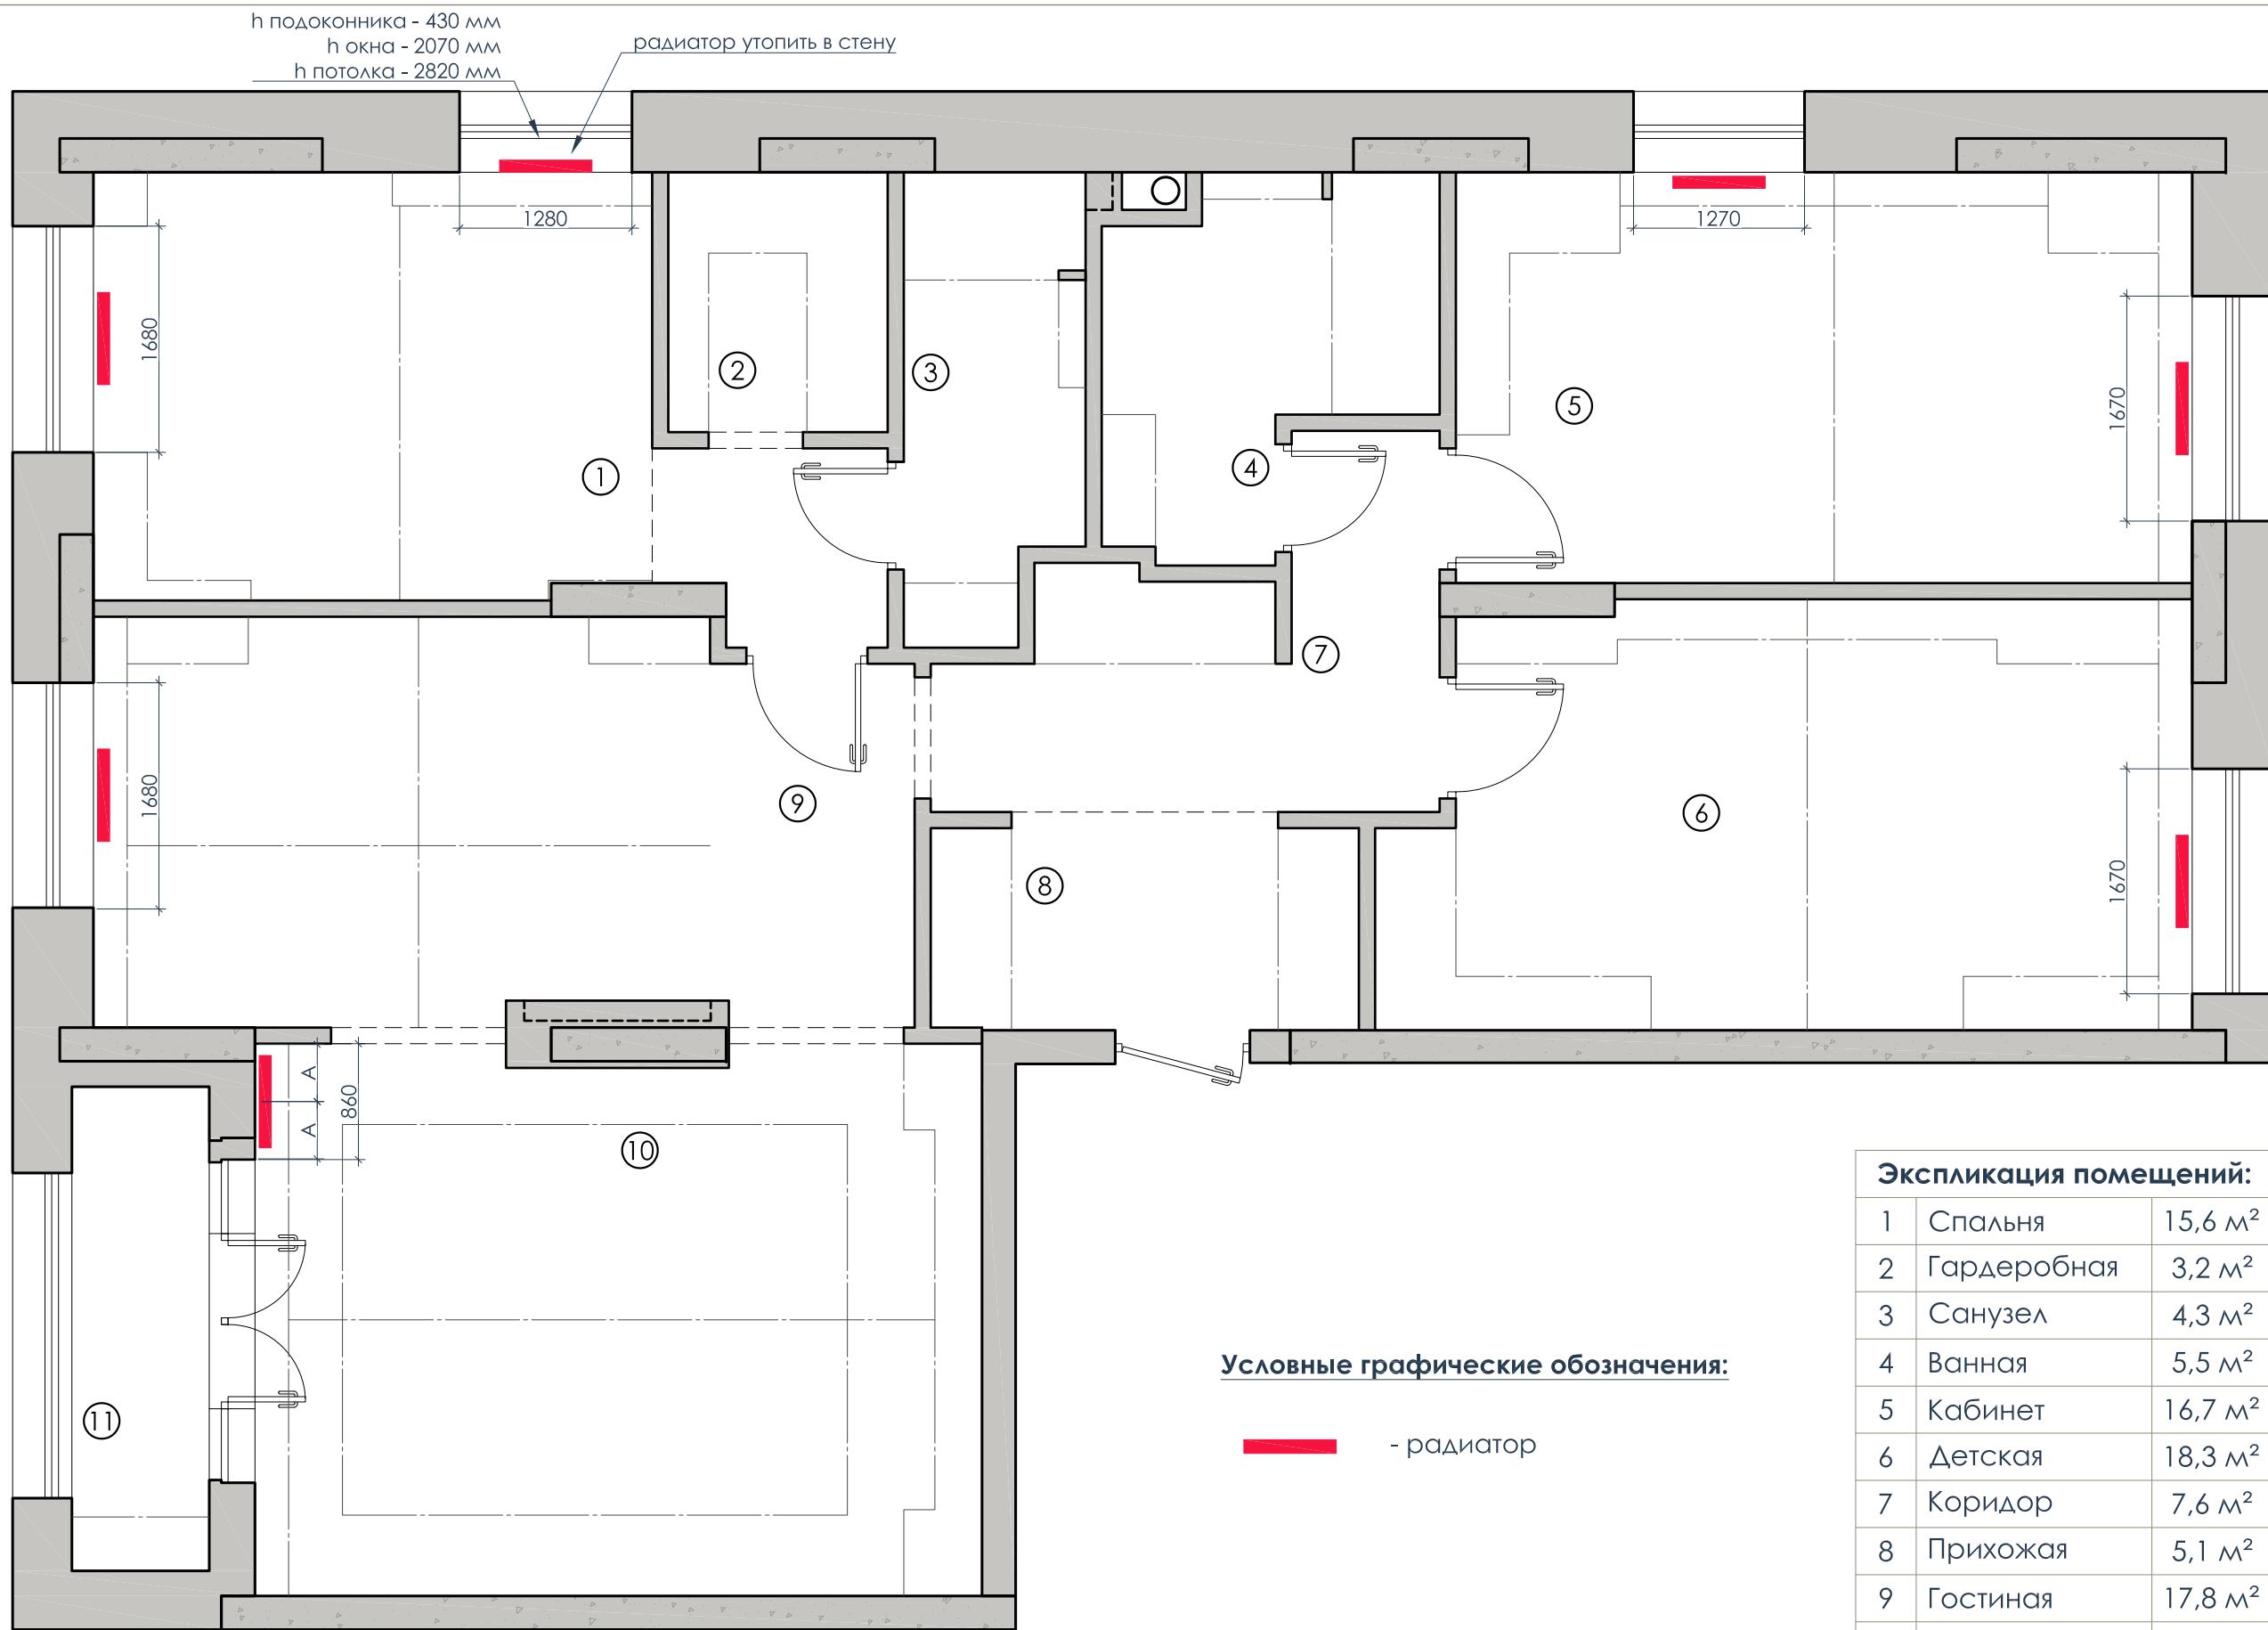


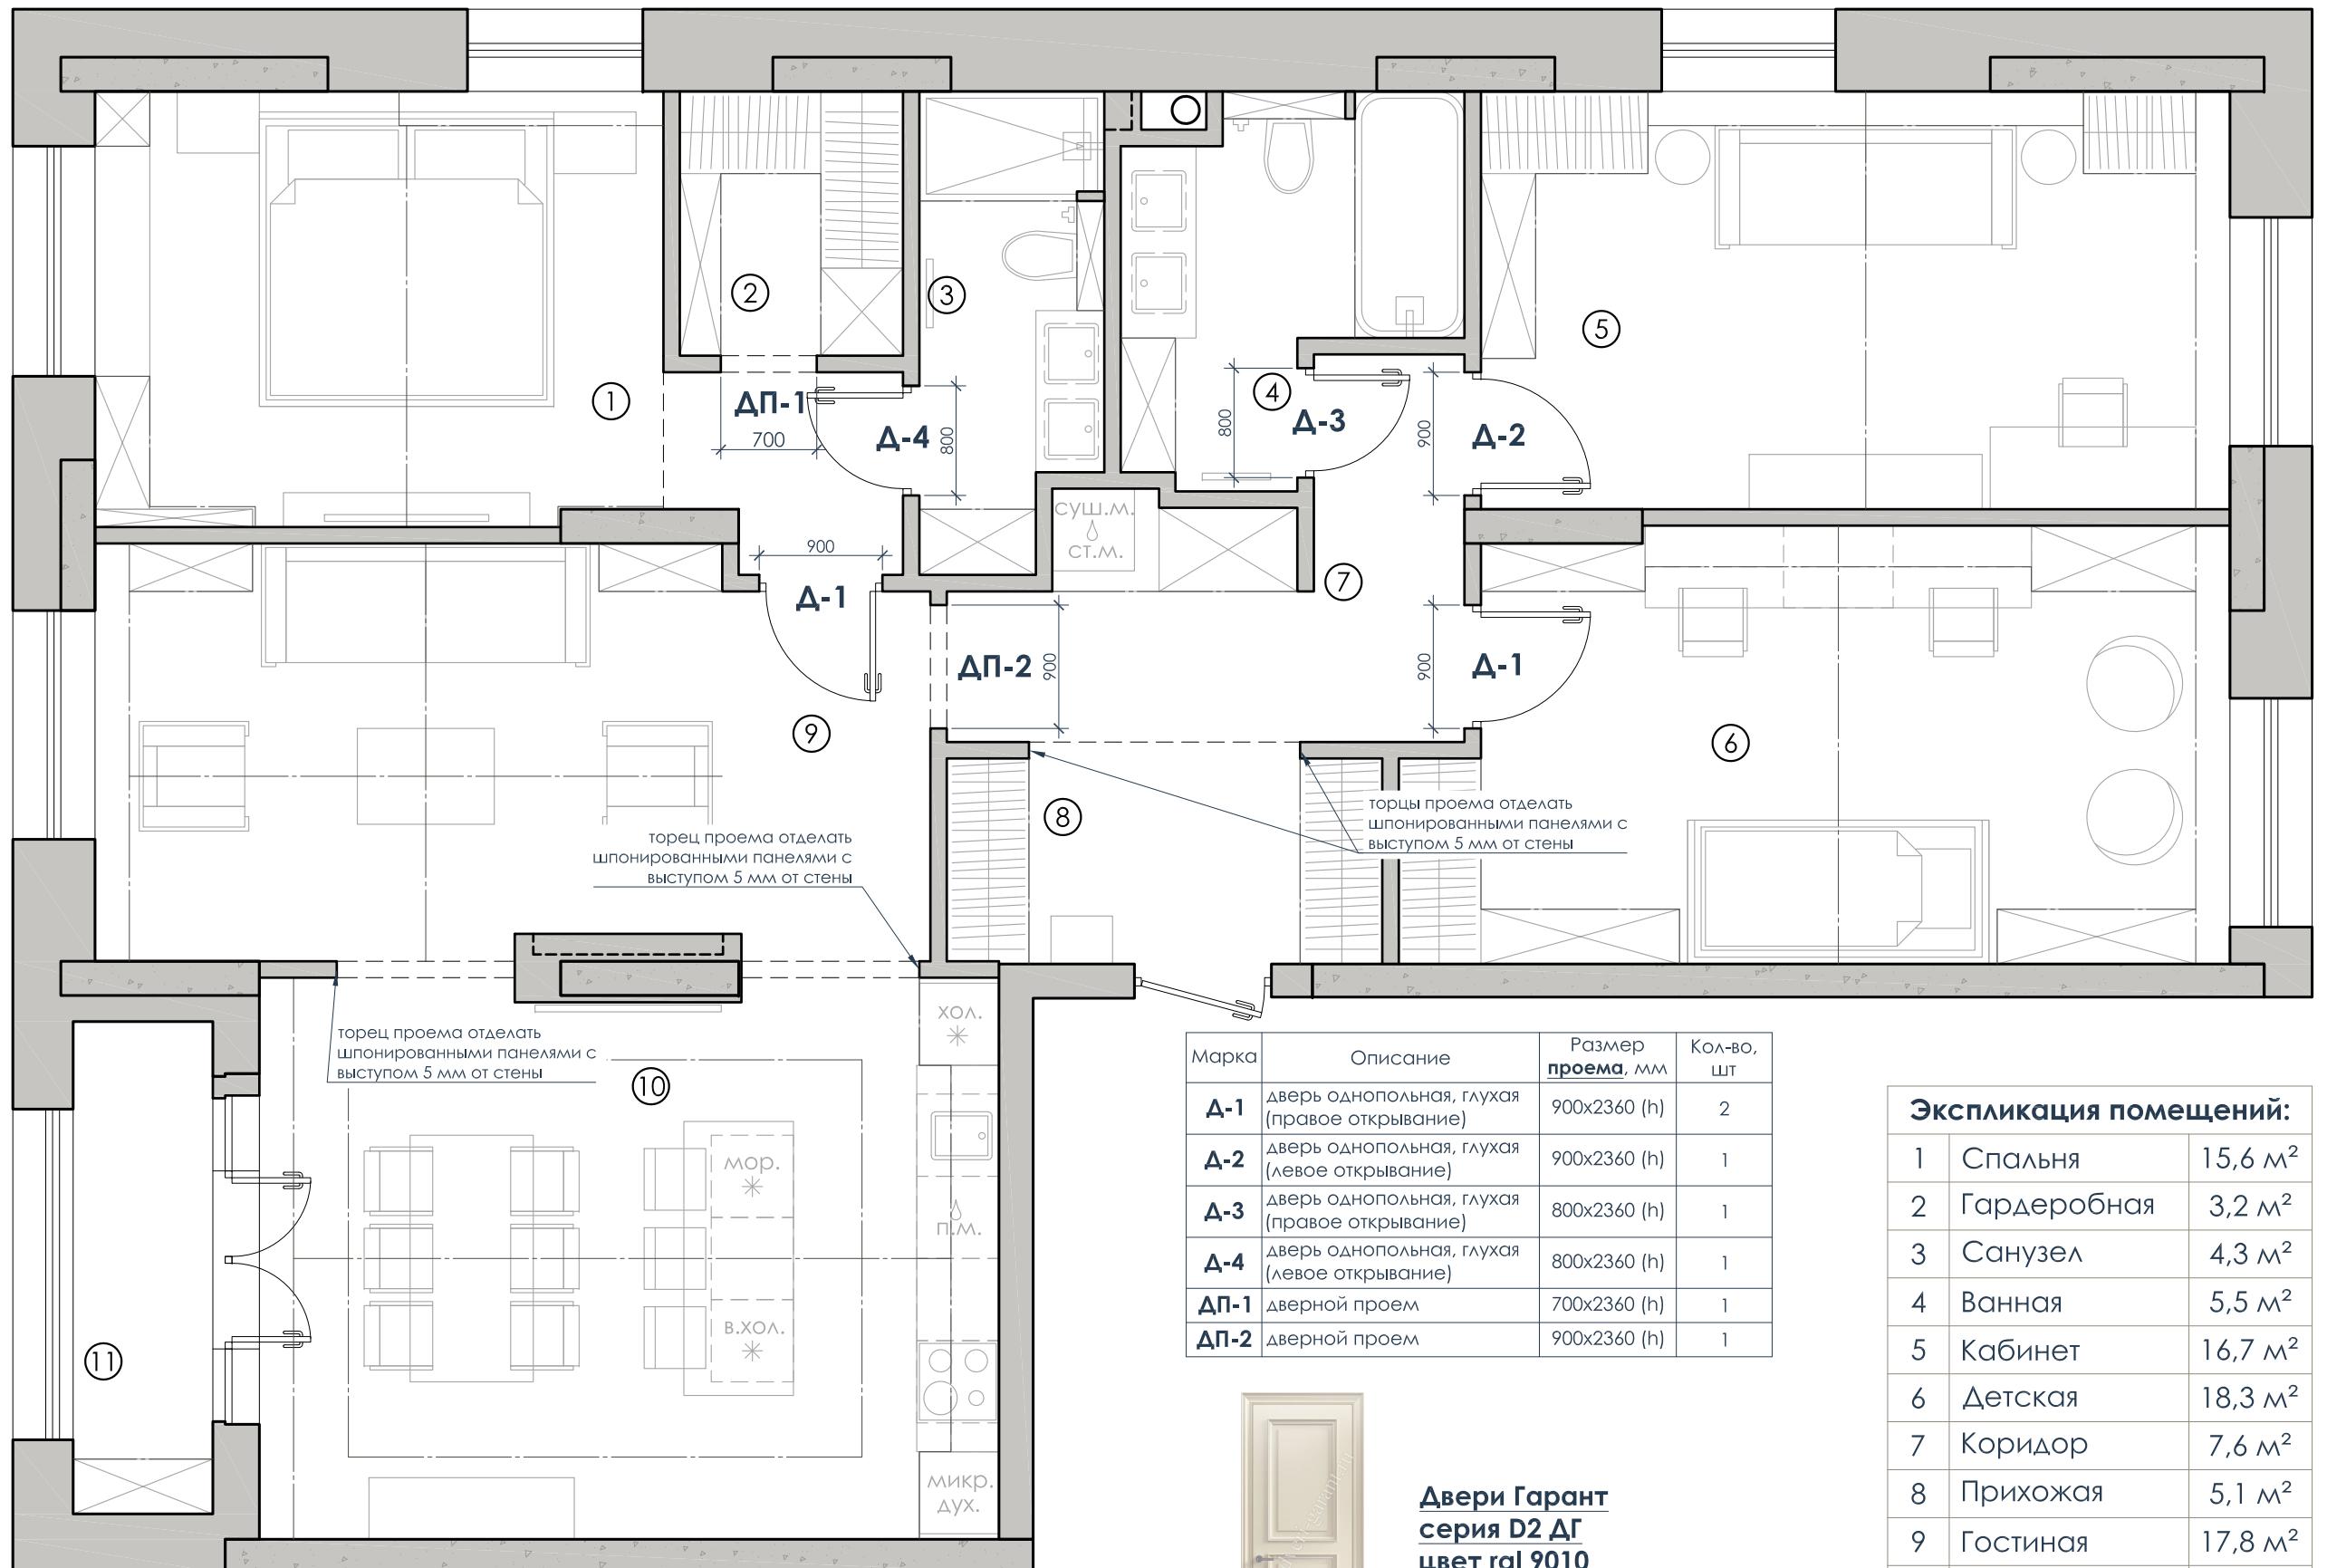


Марка	Описание	Размер проема, мм	Кол-во, шт
Д-1	дверь однопольная, глухая (правое открывание)	900x2360 (h)	2
Д-2	дверь однопольная, глухая (левое открывание)	900x2360 (h)	1
Д-3	дверь однопольная, глухая (правое открывание)	800x2360 (h)	1
Д-4	дверь однопольная, глухая (левое открывание)	800x2360 (h)	1
ДП-1	дверной проем	700x2360 (h)	1
ДП-2	дверной проем	900x2360 (h)	1

Экспликация помещений:		
1	Спальня	15,6 м <sup>2</sup>
2	Гардеробная	3,2 м <sup>2</sup>
3	Санузел	4,3 м <sup>2</sup>
4	Ванная	5,5 м <sup>2</sup>
5	Кабинет	16,7 м <sup>2</sup>
6	Детская	18,3 м <sup>2</sup>
7	Коридор	7,6 м <sup>2</sup>
8	Прихожая	5,1 м <sup>2</sup>
9	Гостиная	17,8 м <sup>2</sup>
10	Кухня	22,6 м <sup>2</sup>
11	Балкон	3,9 м <sup>2</sup>
<b>Общая площадь: 120,6 м<sup>2</sup></b>		

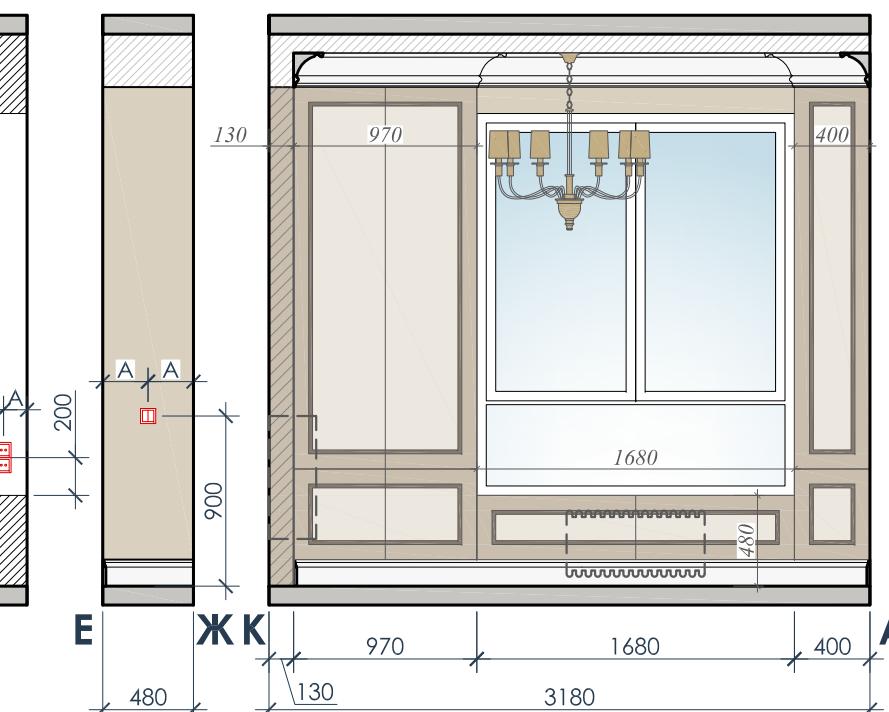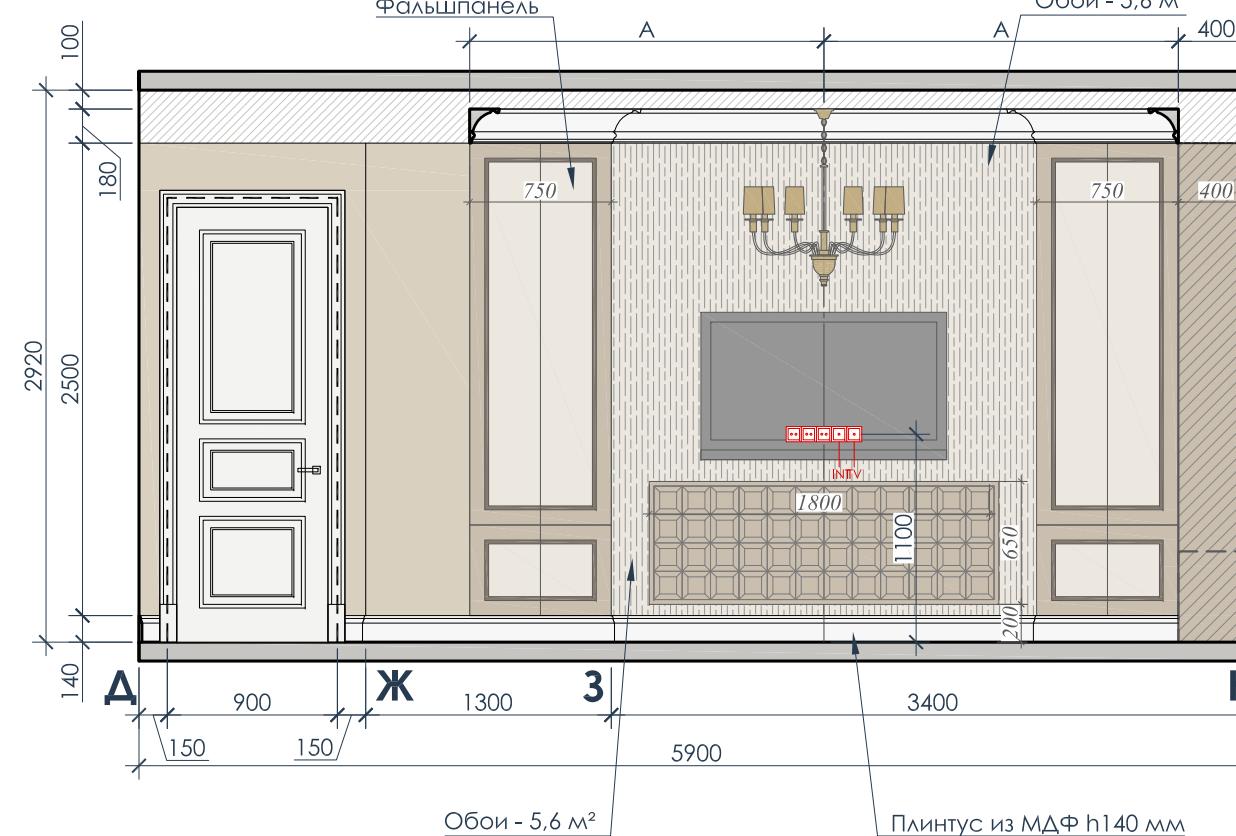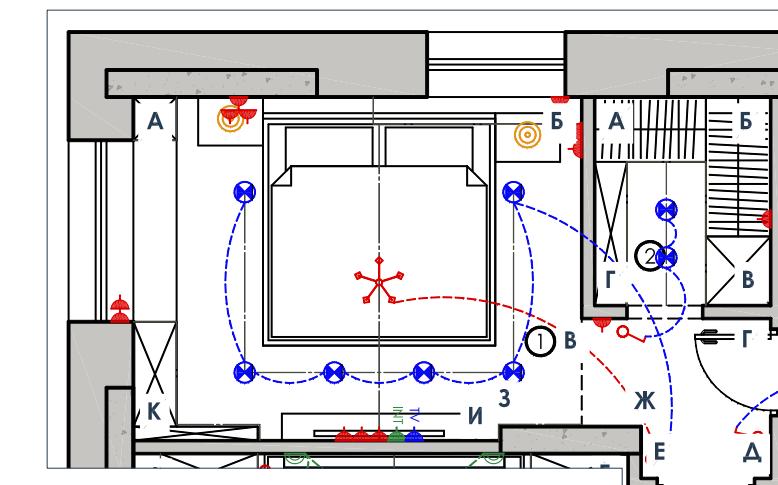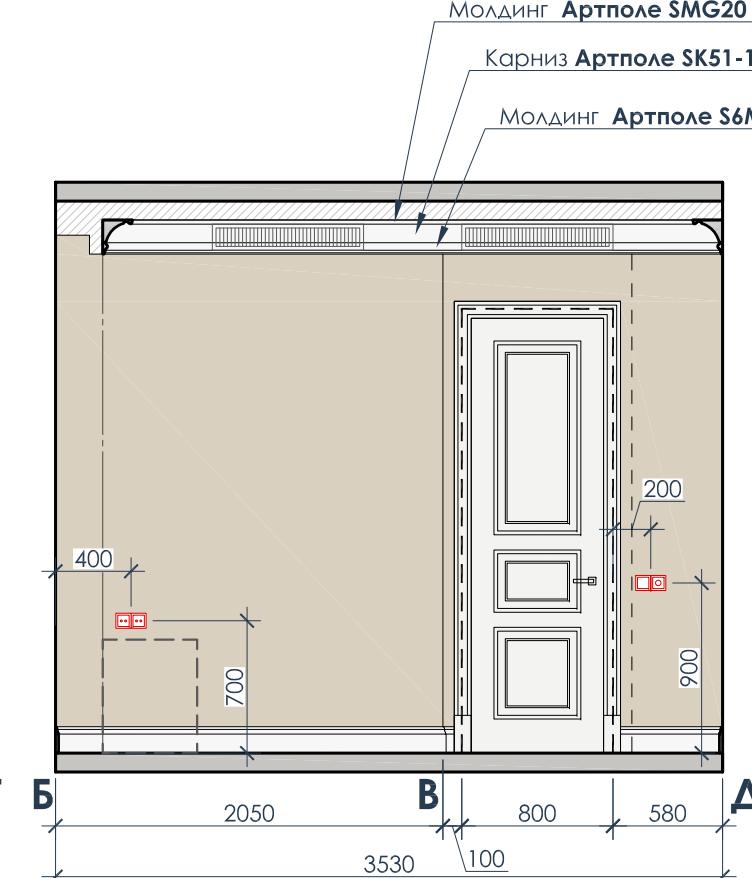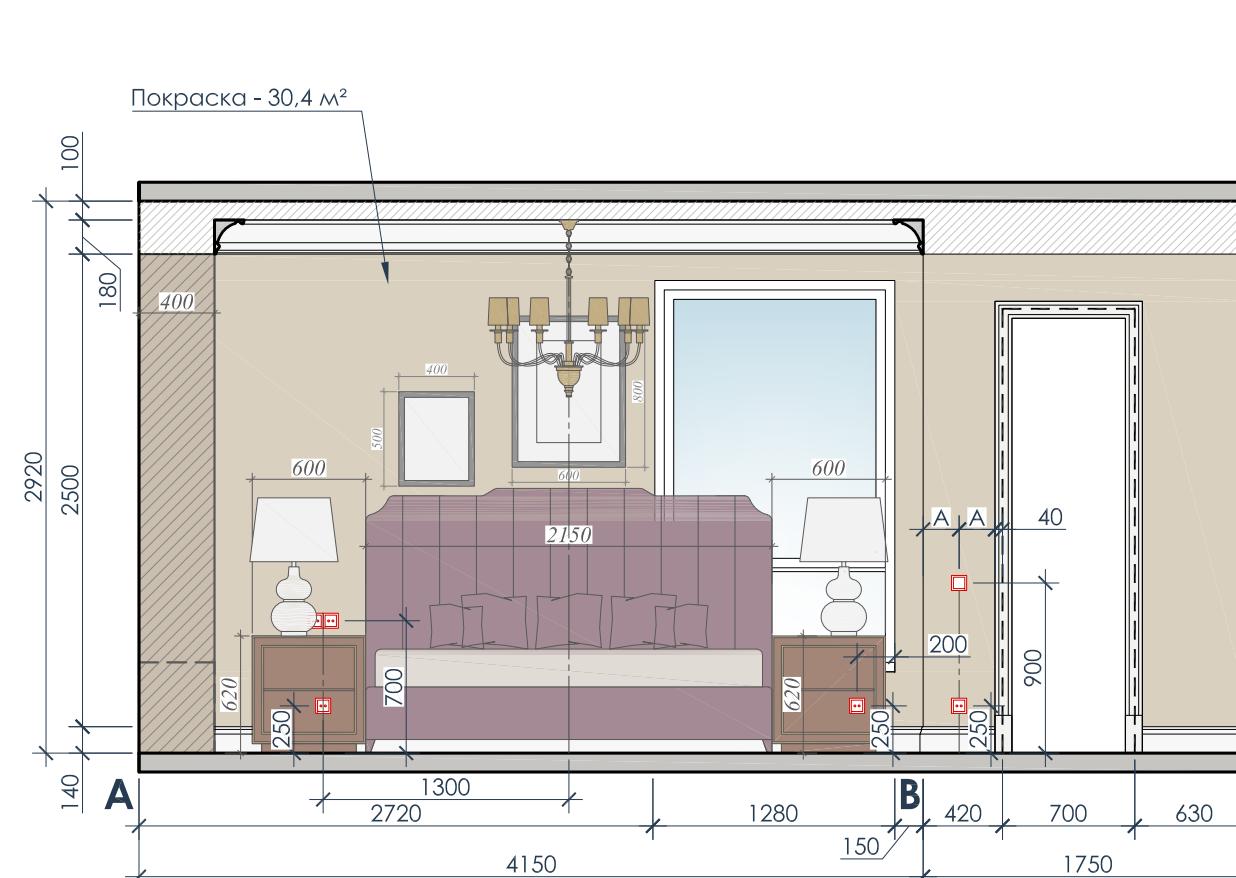

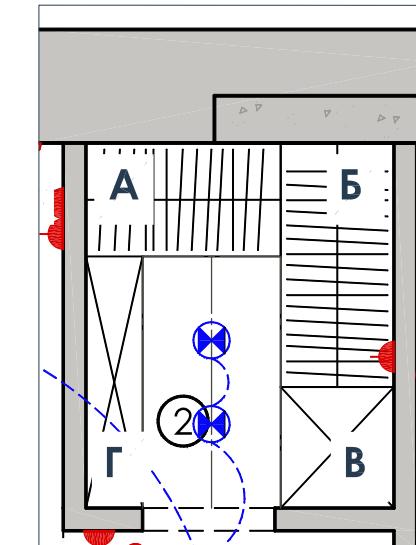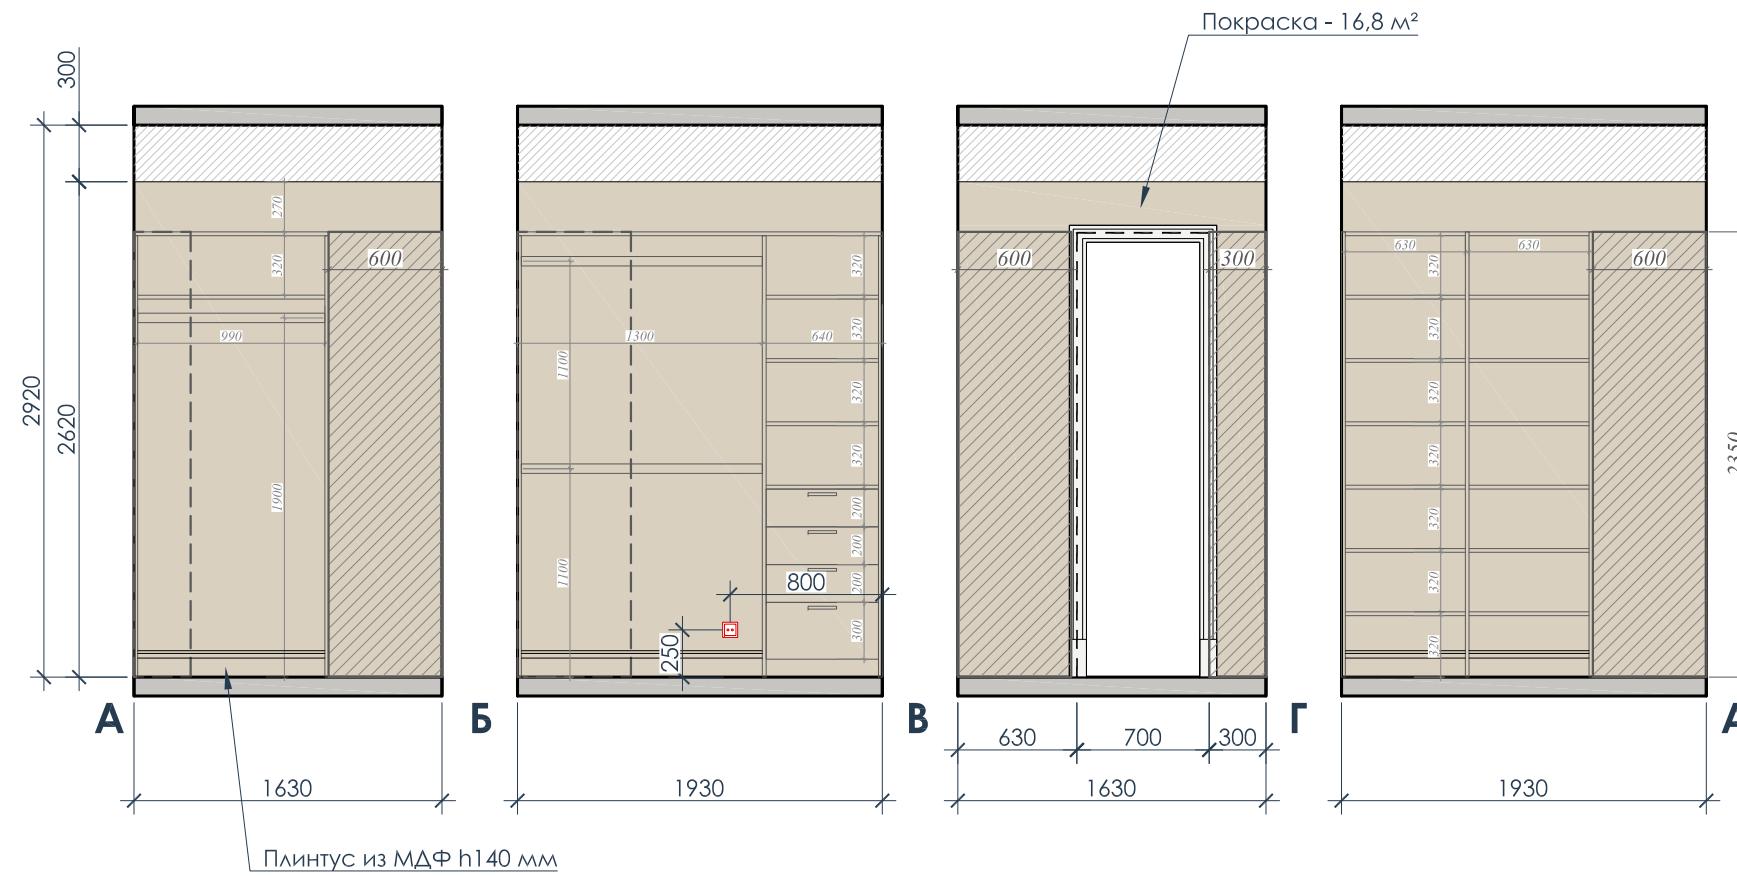

Керамогранит **Atlas Concorde Russia**  
**Empire Intarsi Rett Lapp** 600x1200 мм - 3,2 м<sup>2</sup>

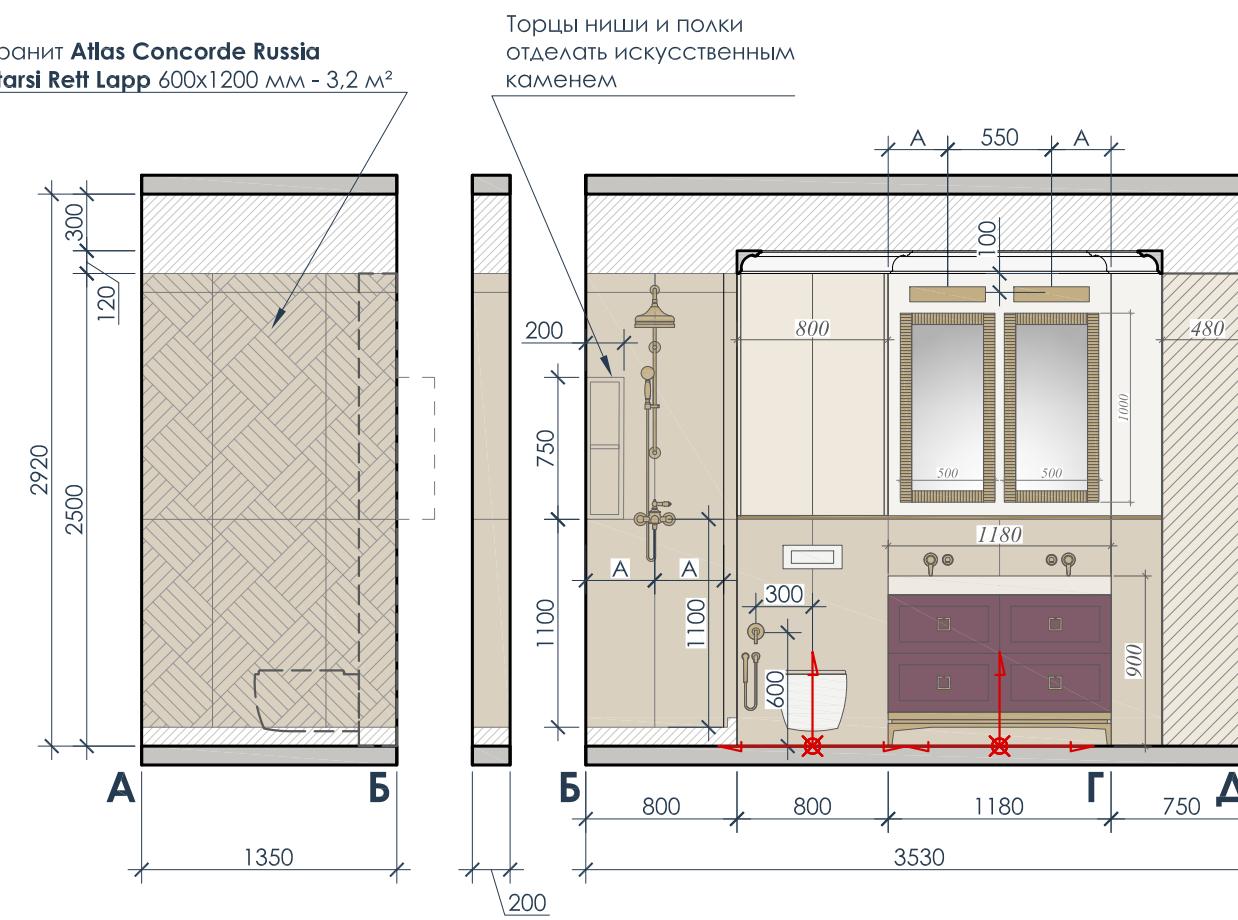


**Empire Intarsi Rett Lapp**




**Empire Tajmahal Rett Lapp**








Карниз Артполе SK26G 129x120мм



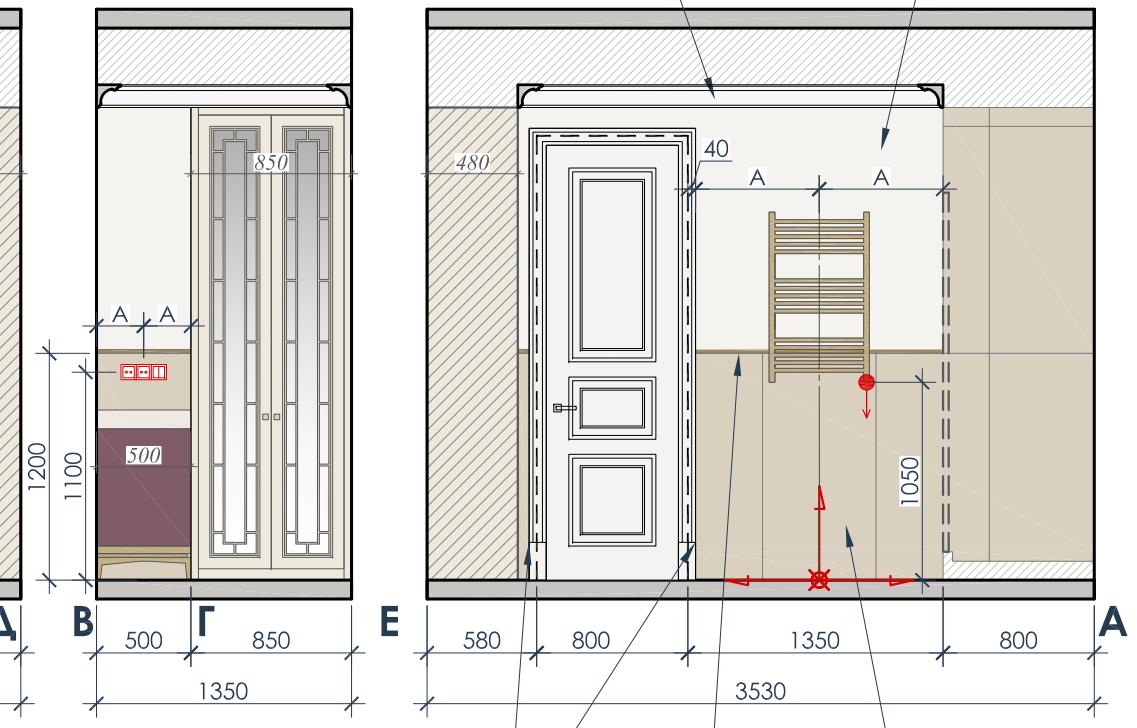




Керамогранит **Atlas Concorde Russia**  
**Empire Tajmahal Rett Lapp** 600x1200 мм - 9,5 м<sup>2</sup>

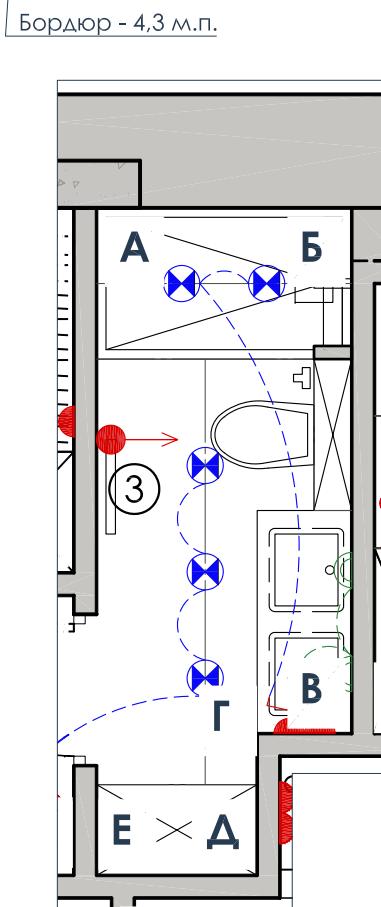

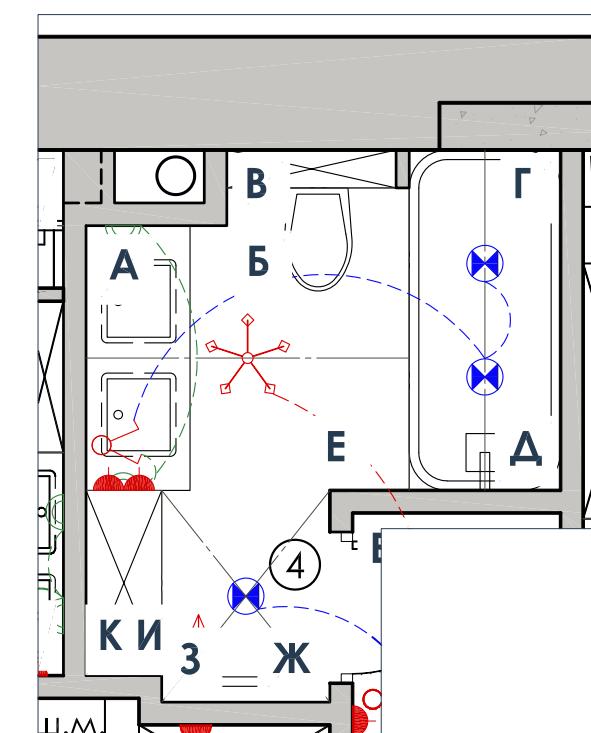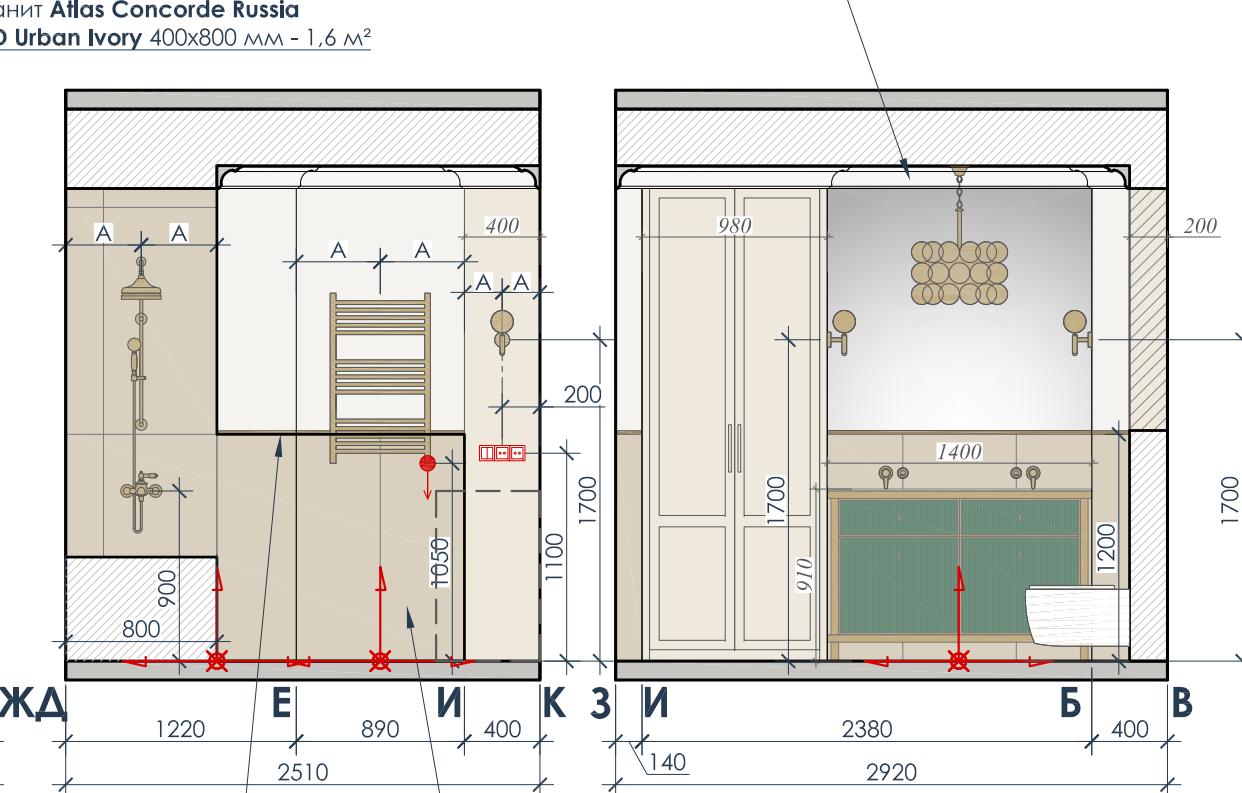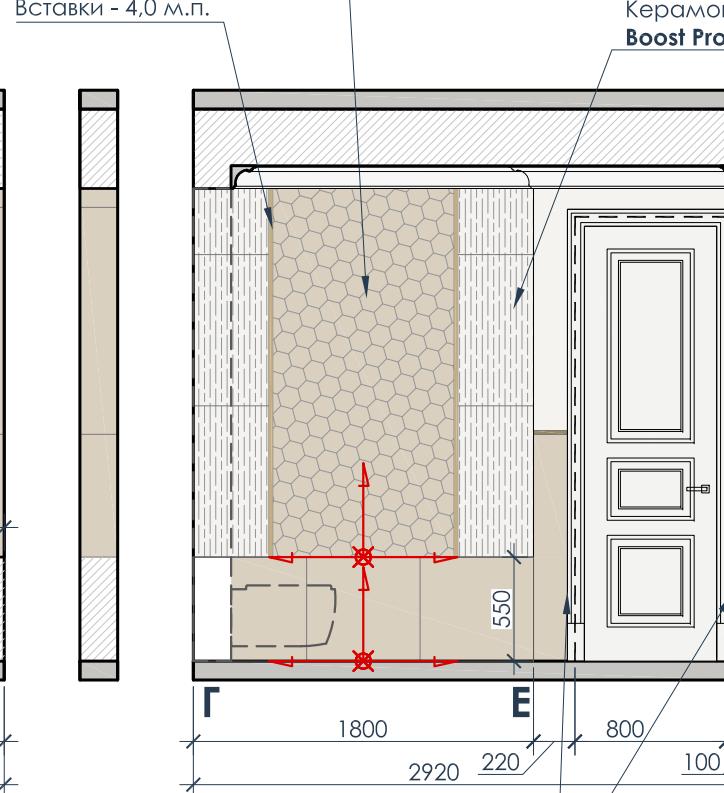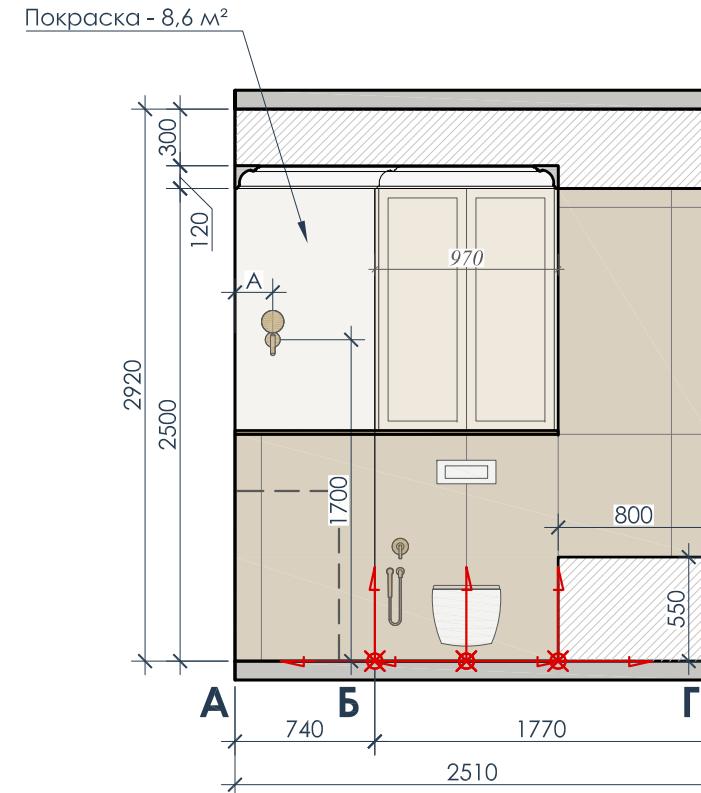


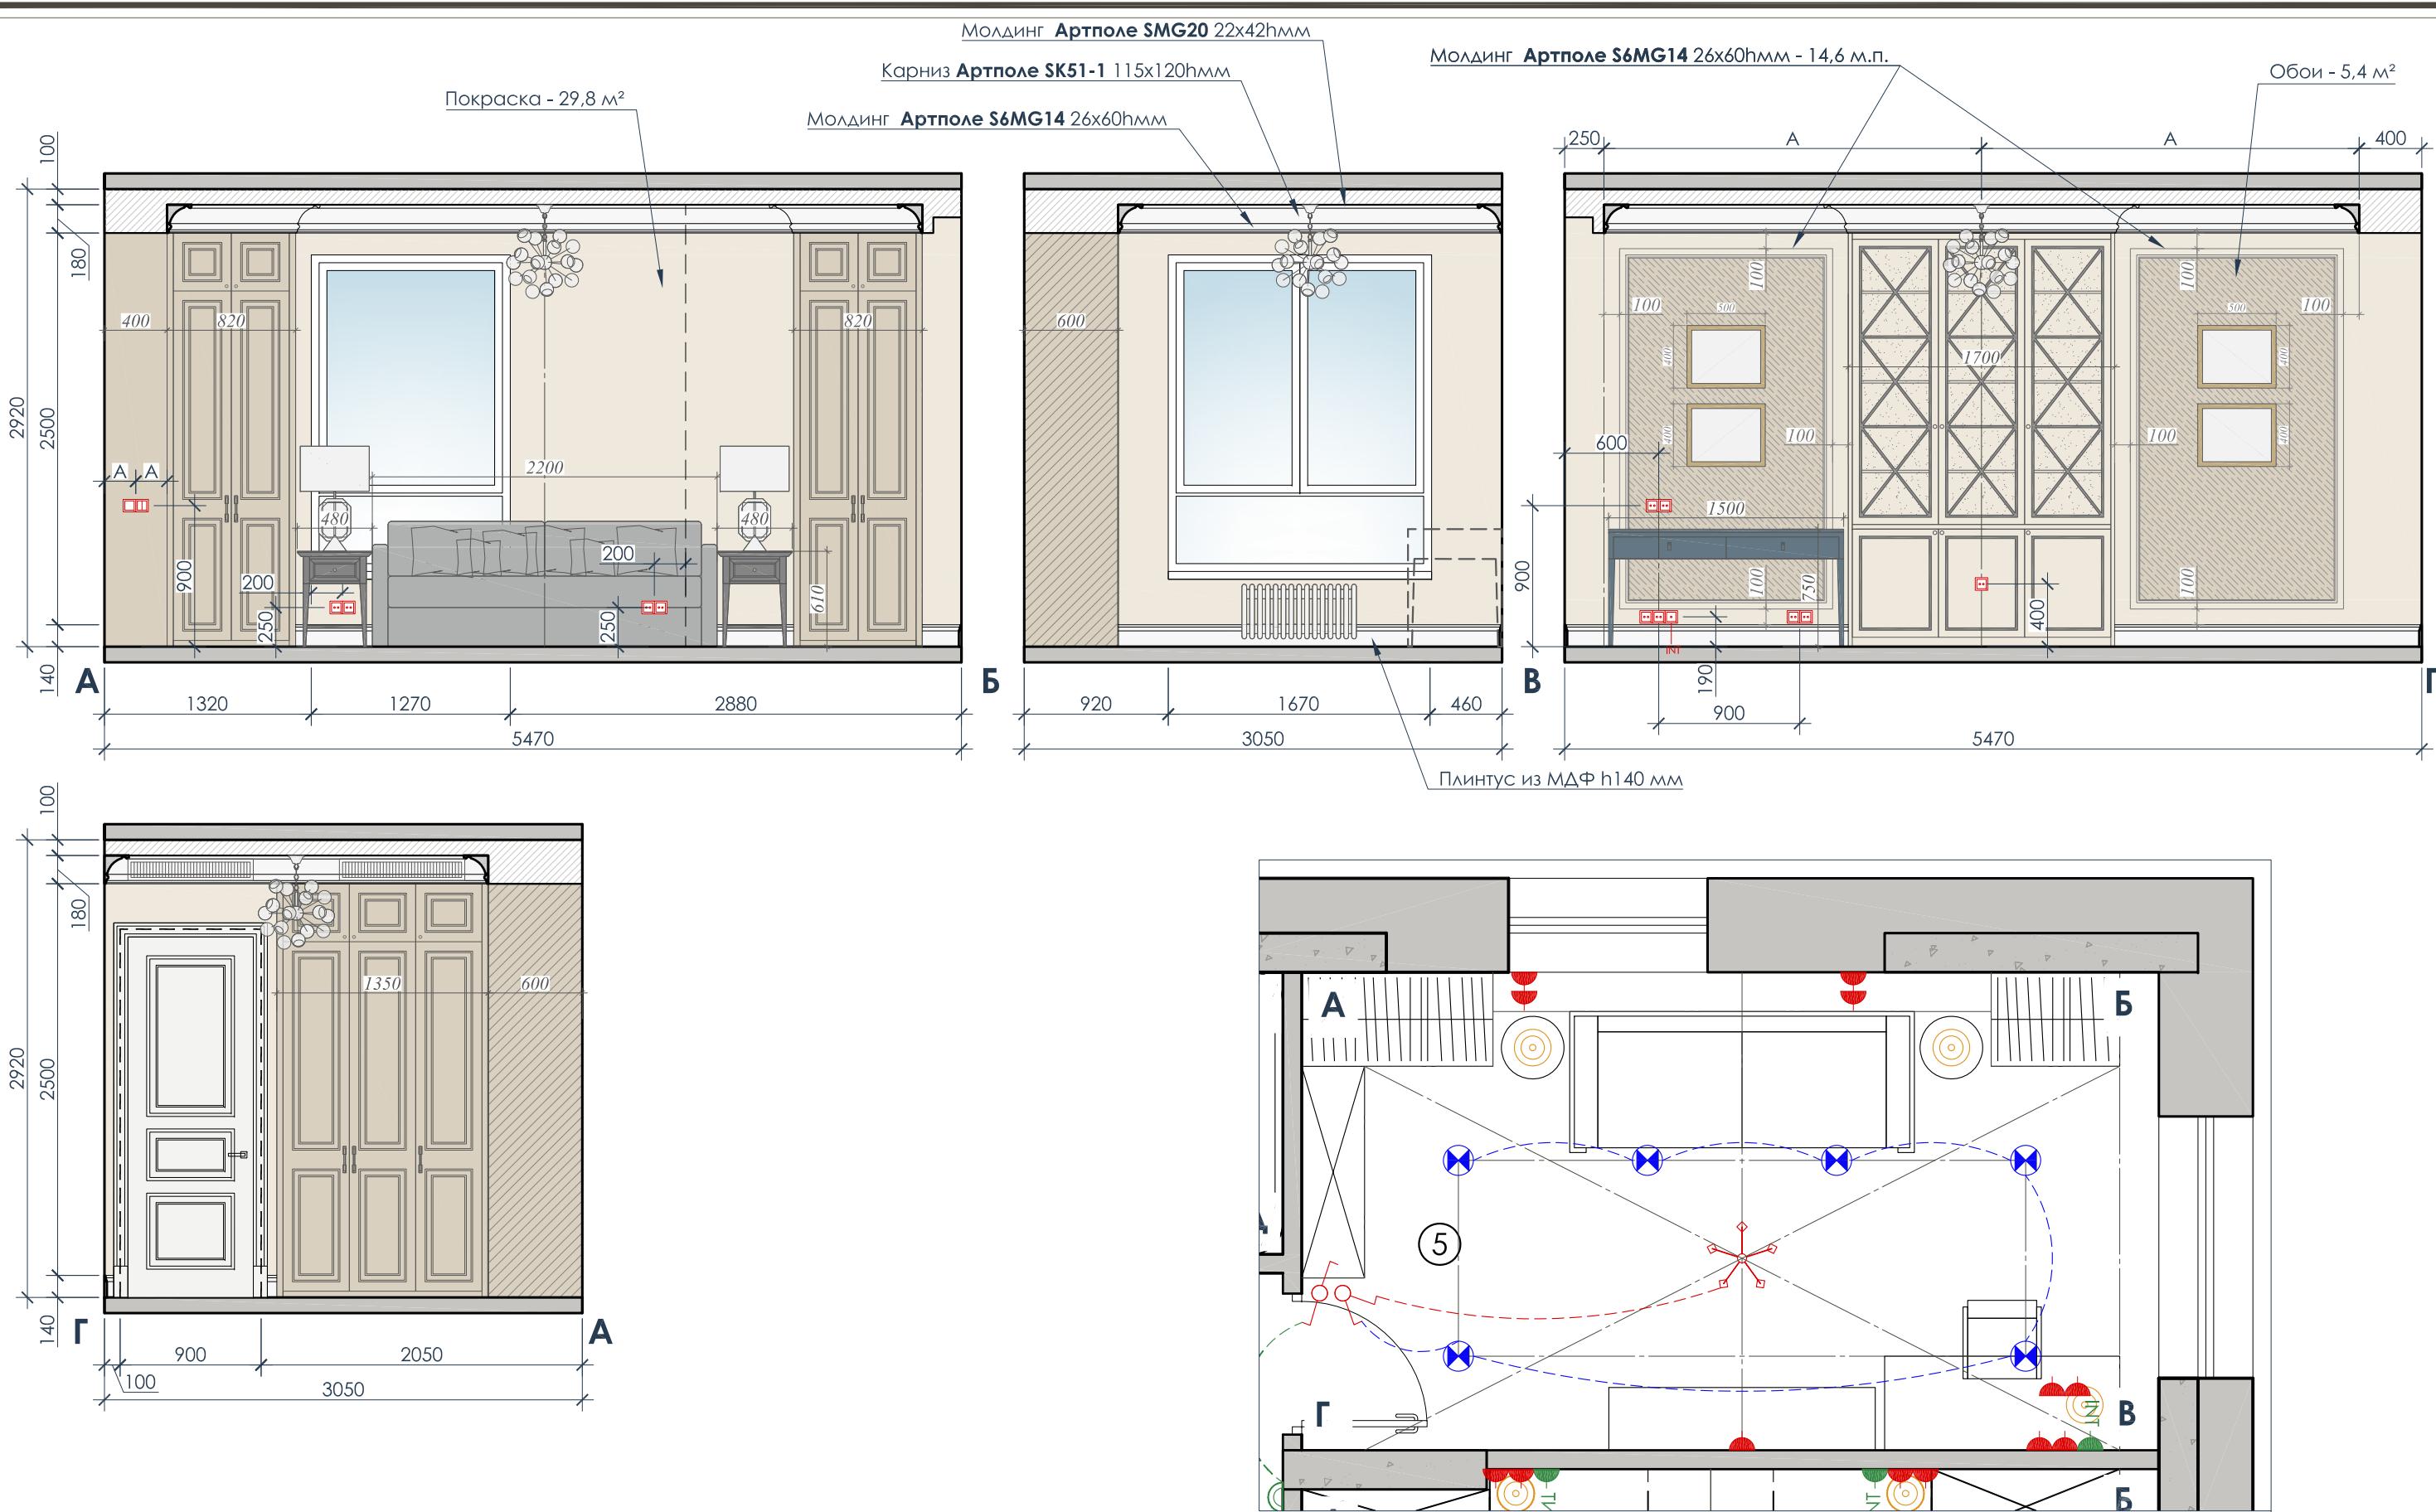



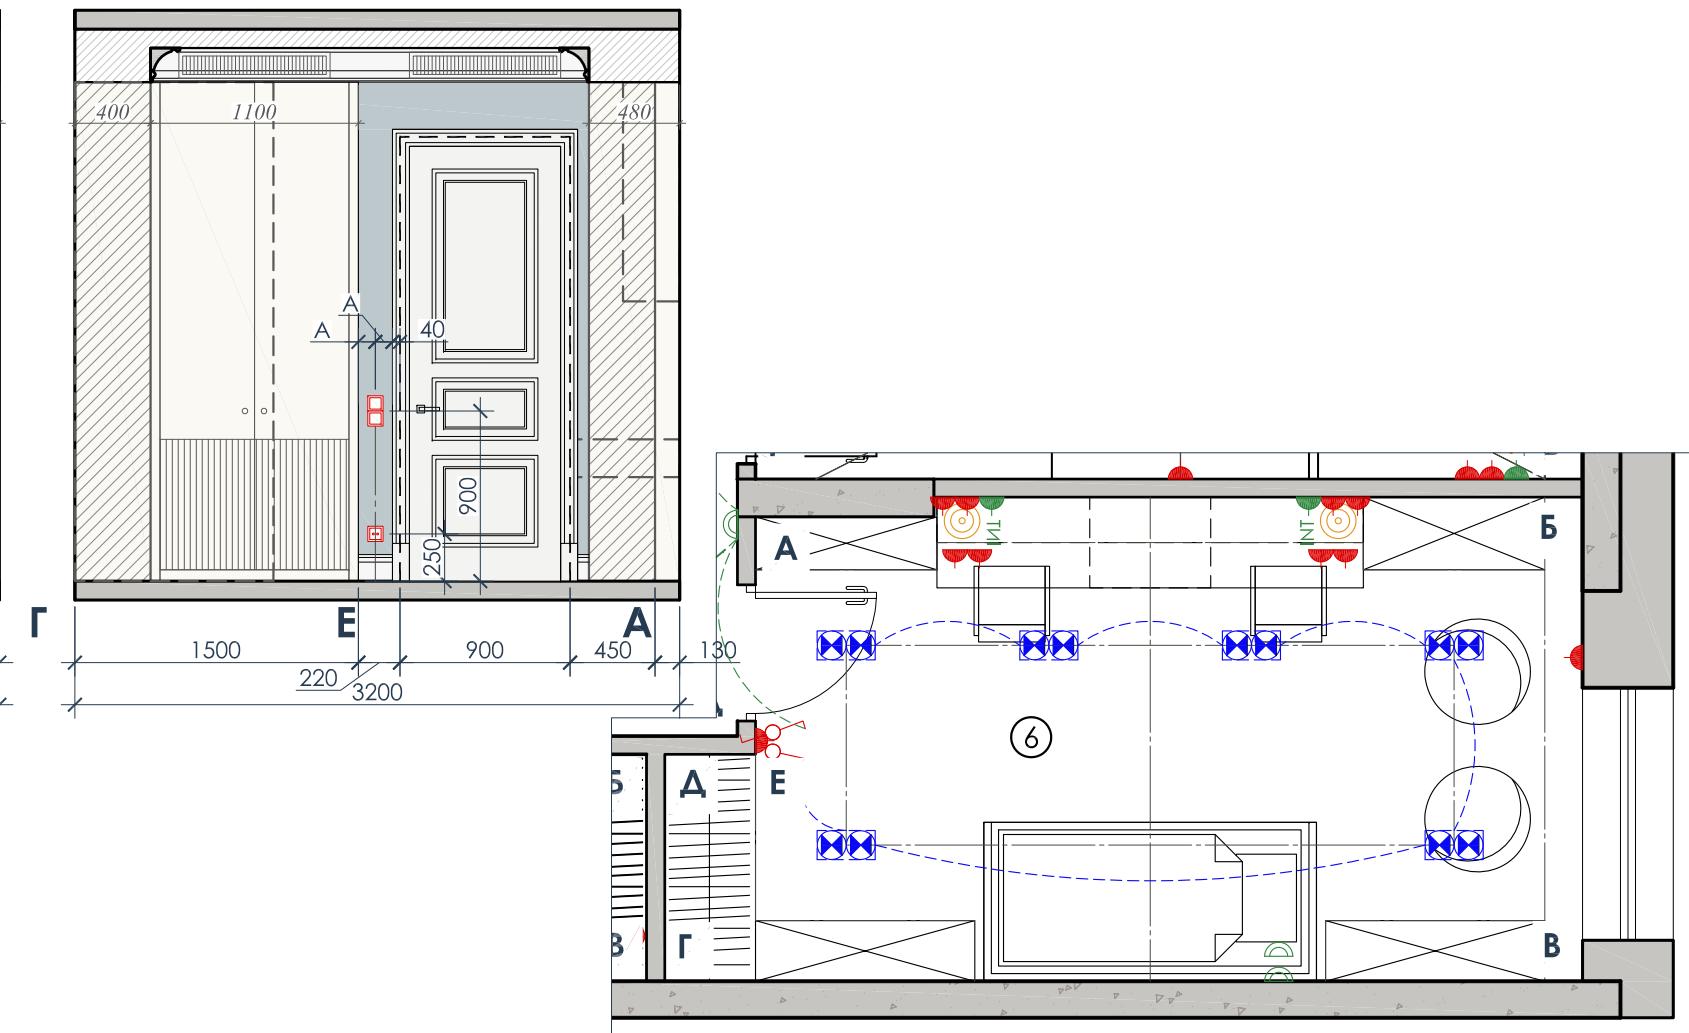
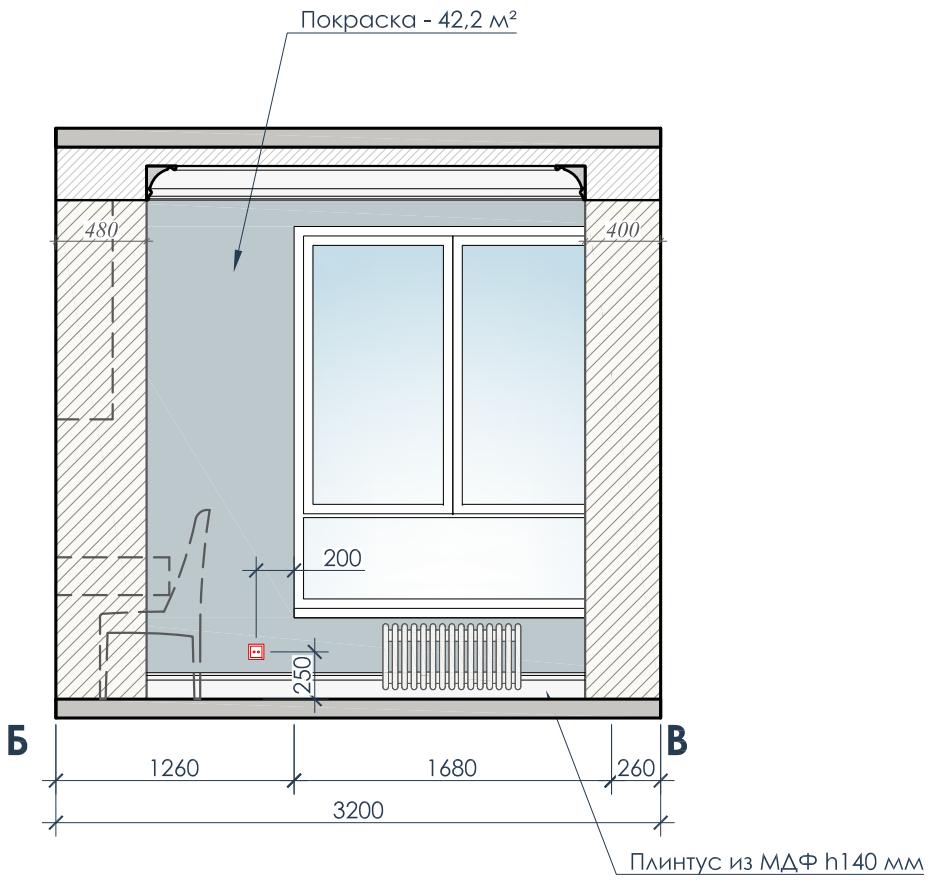
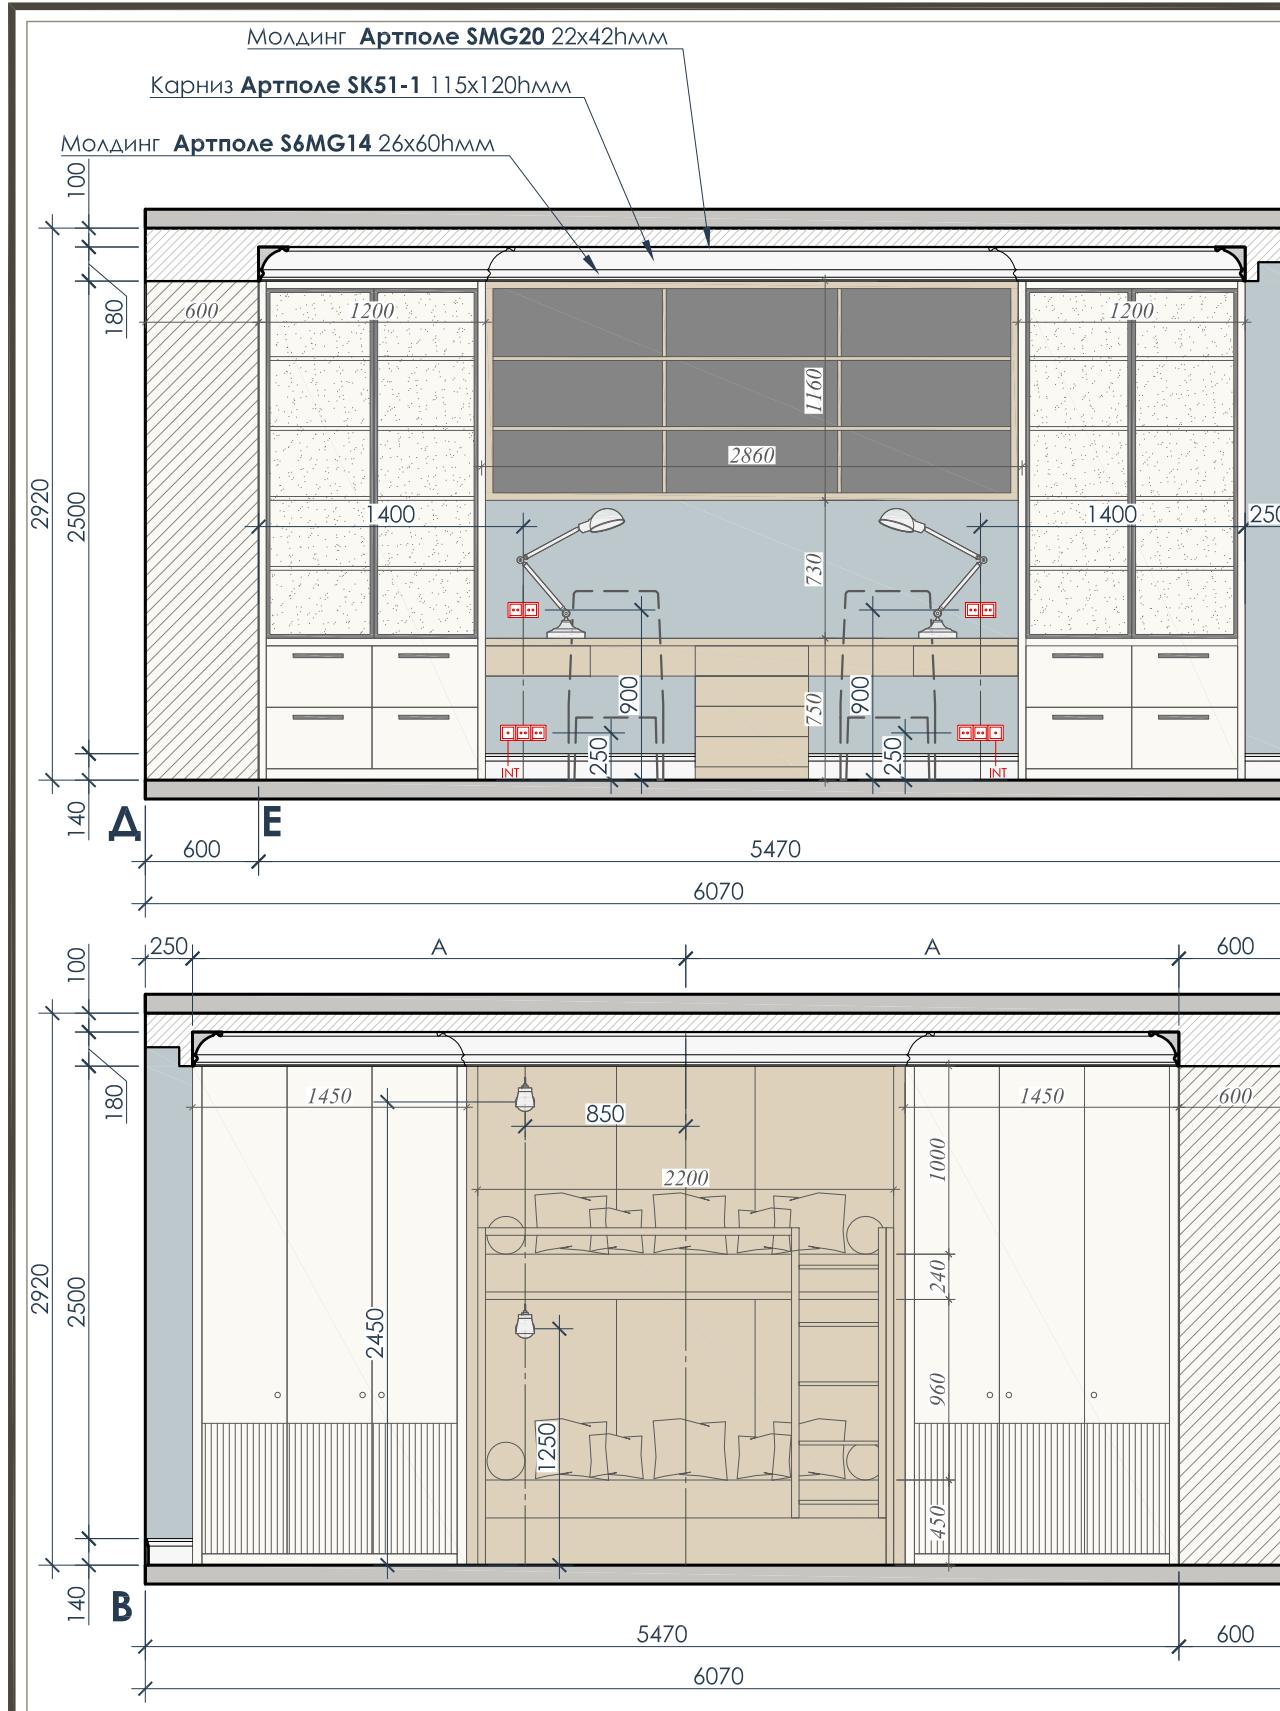


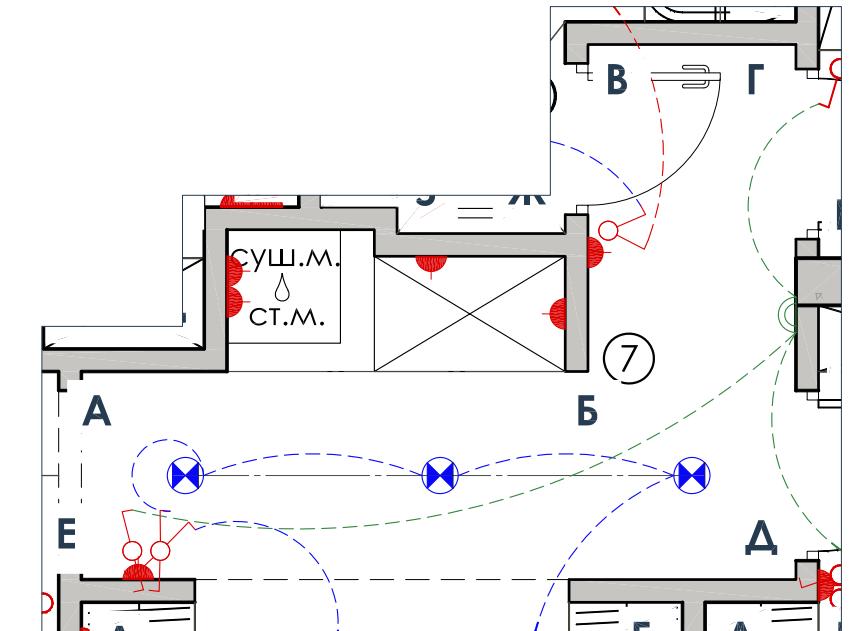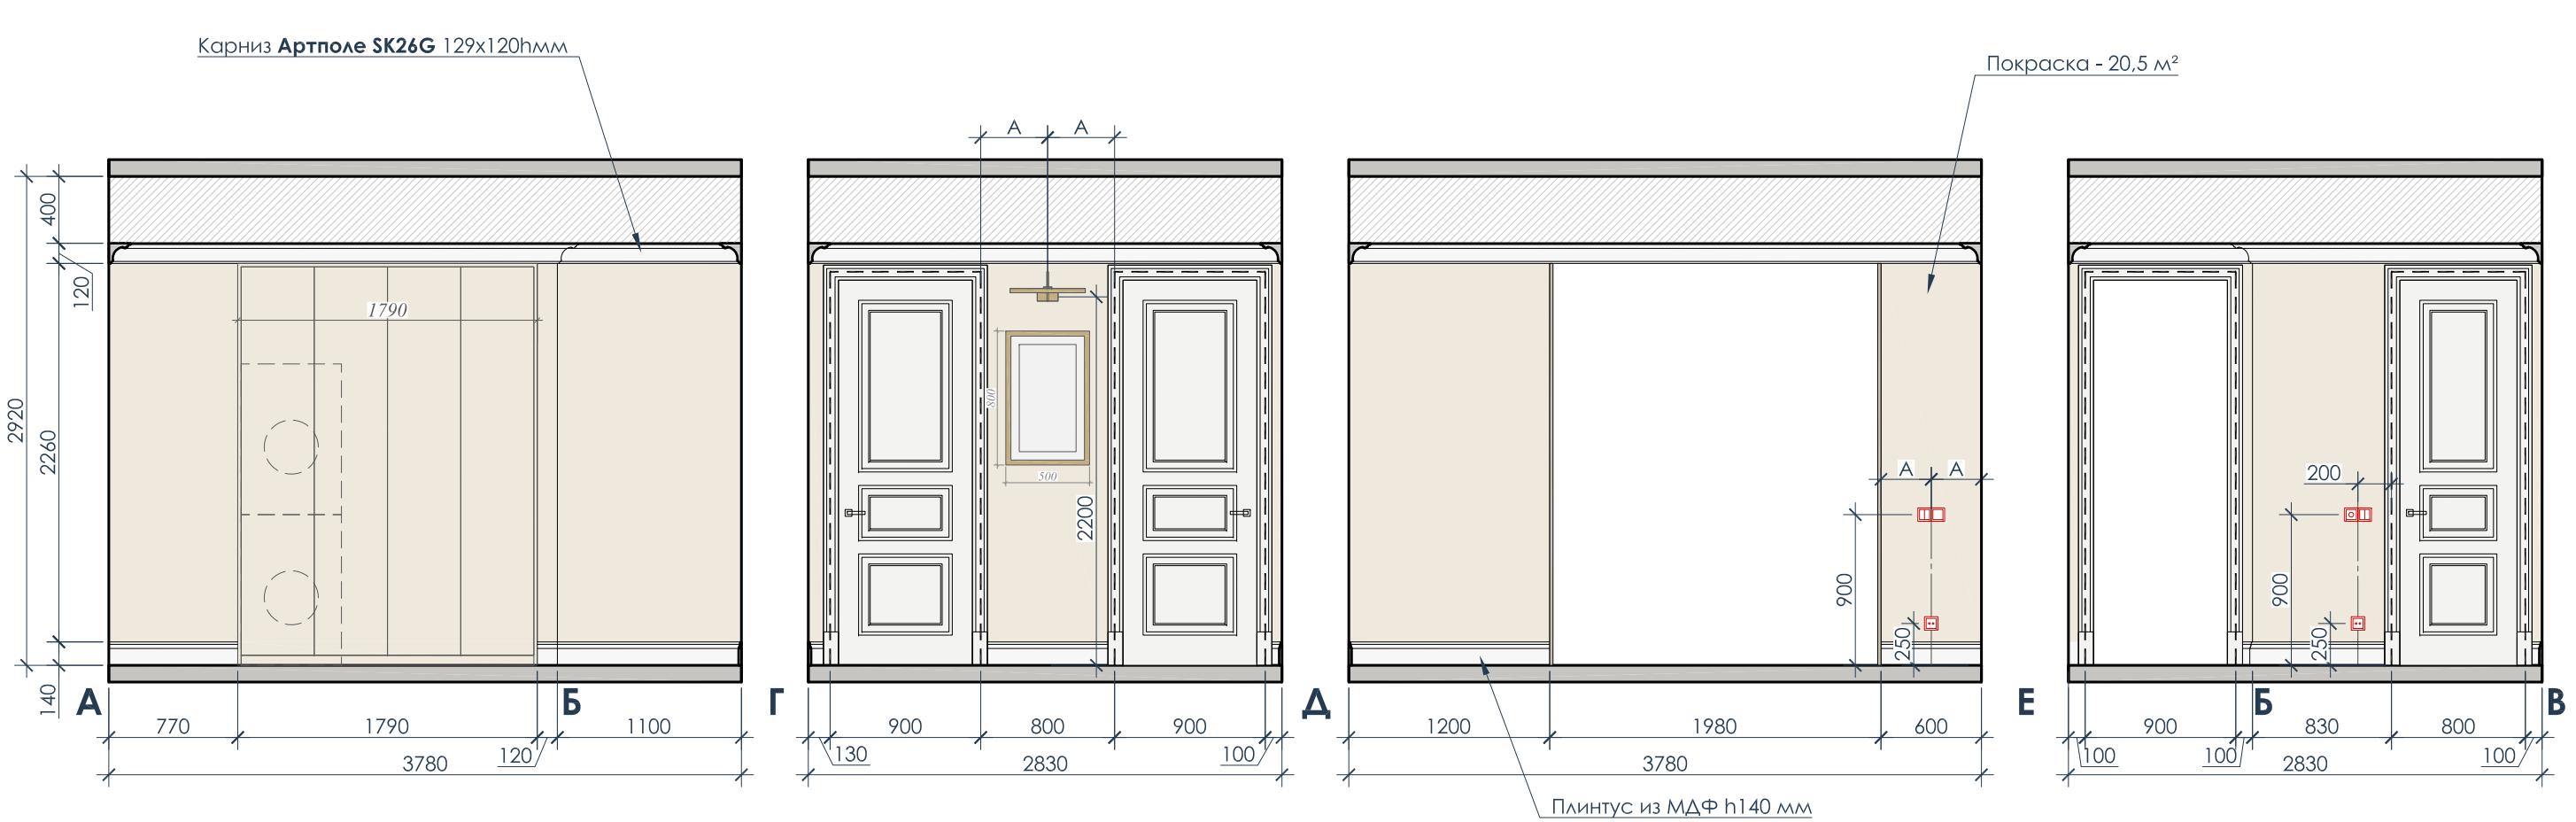


Карниз Артполе SK26G 129x120мм

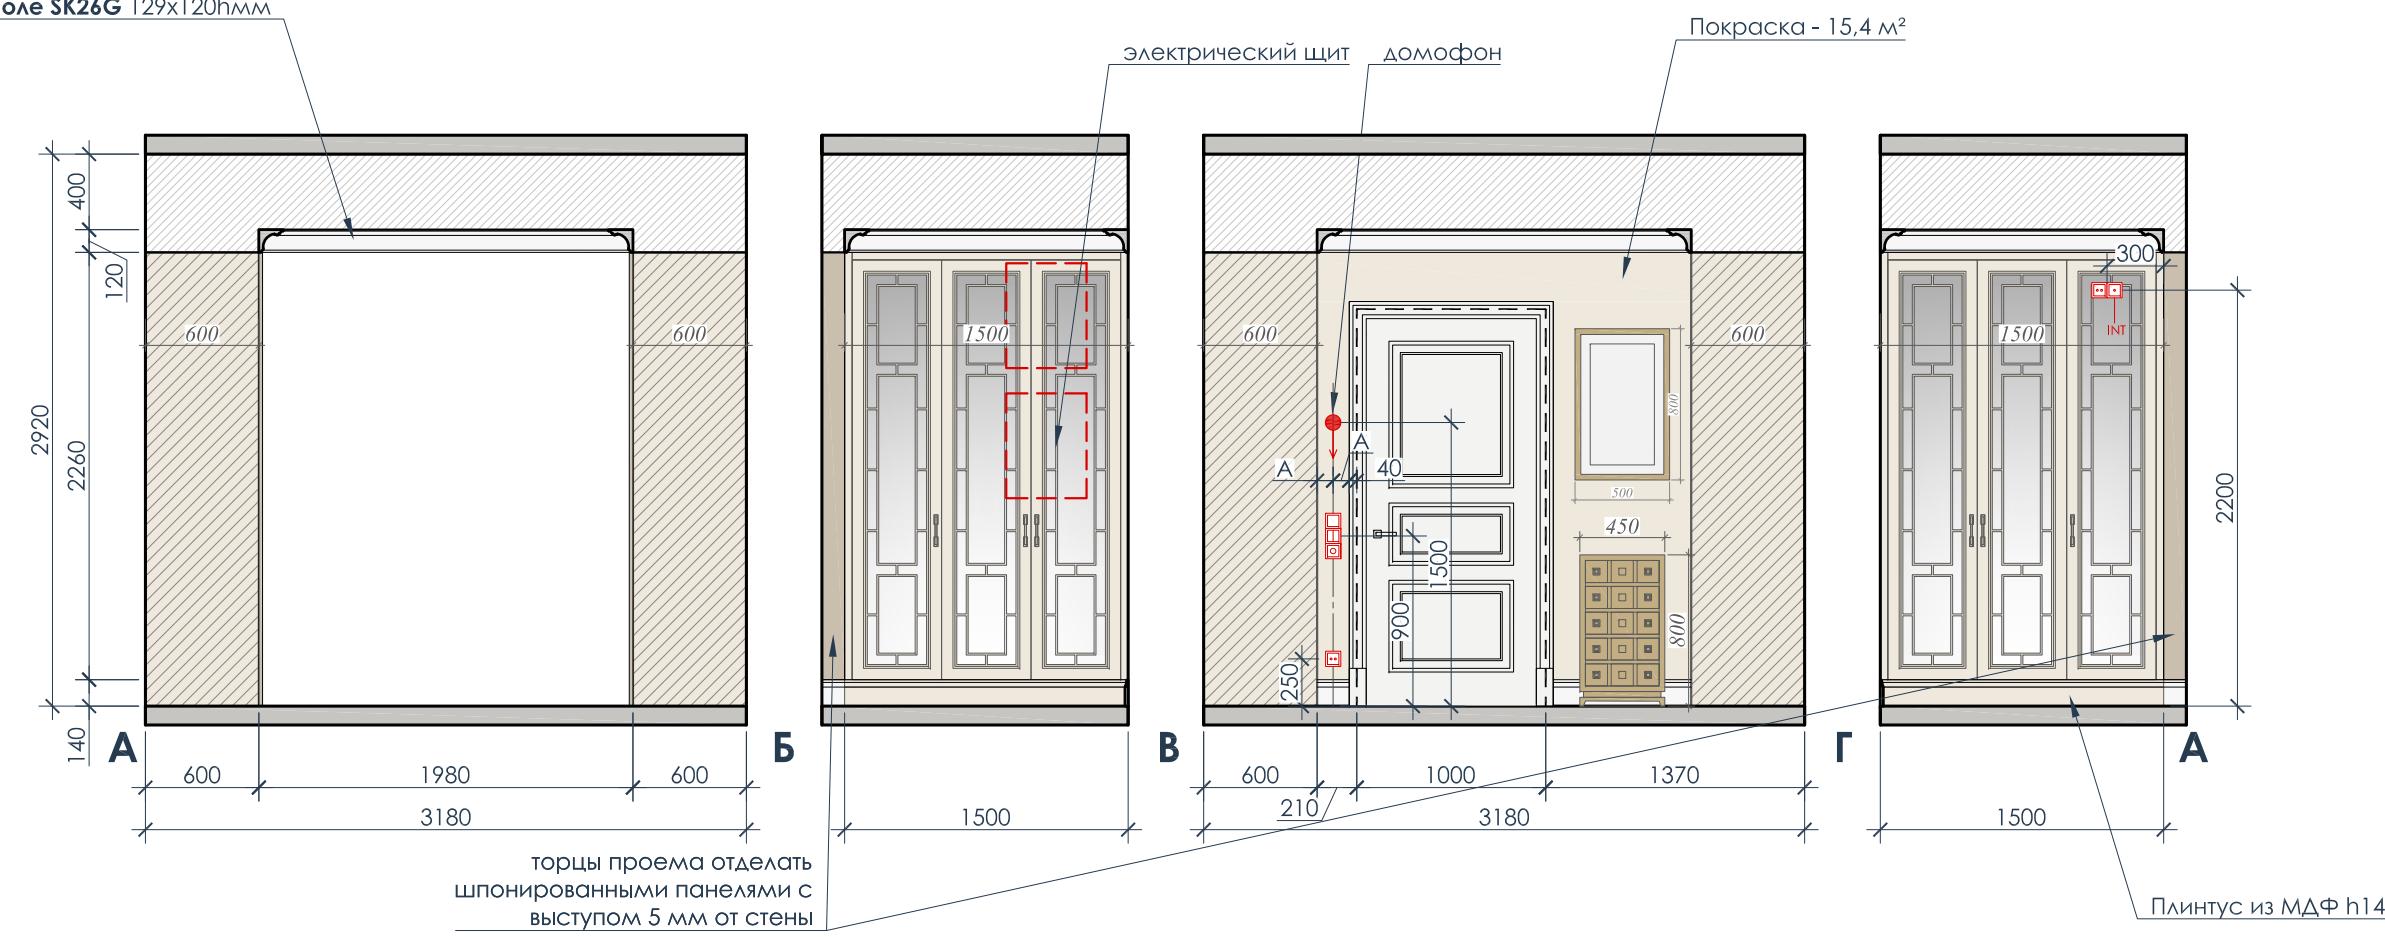

## Развертки прихожей №8

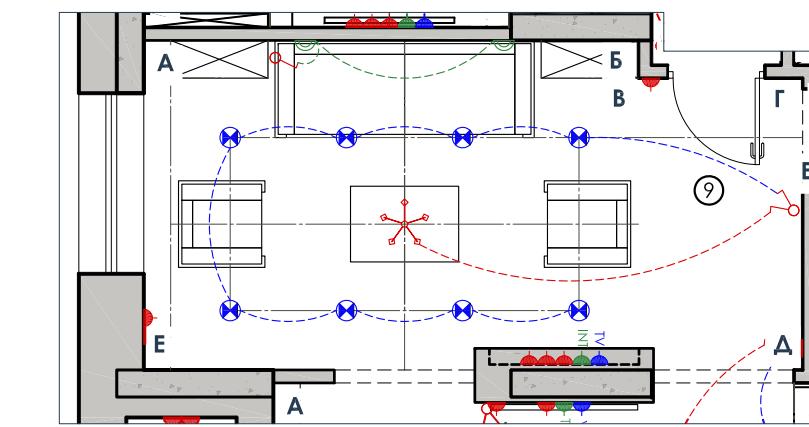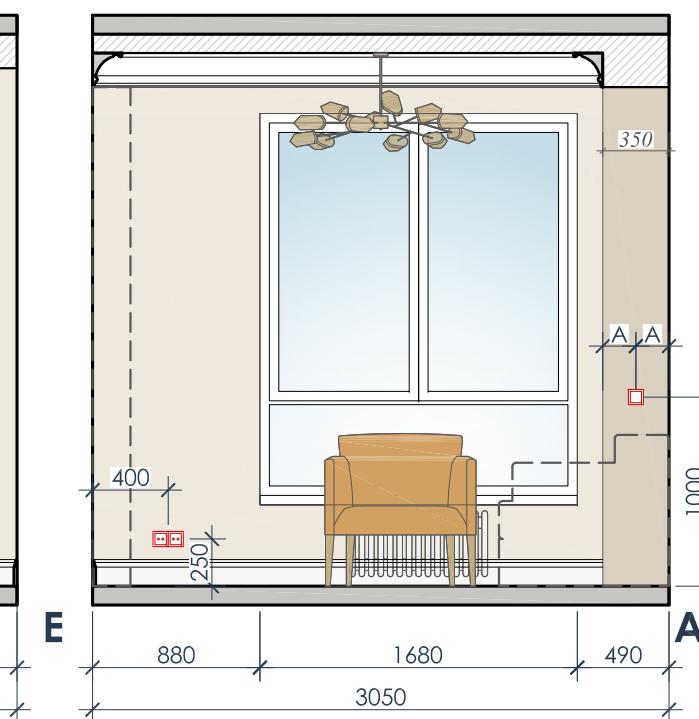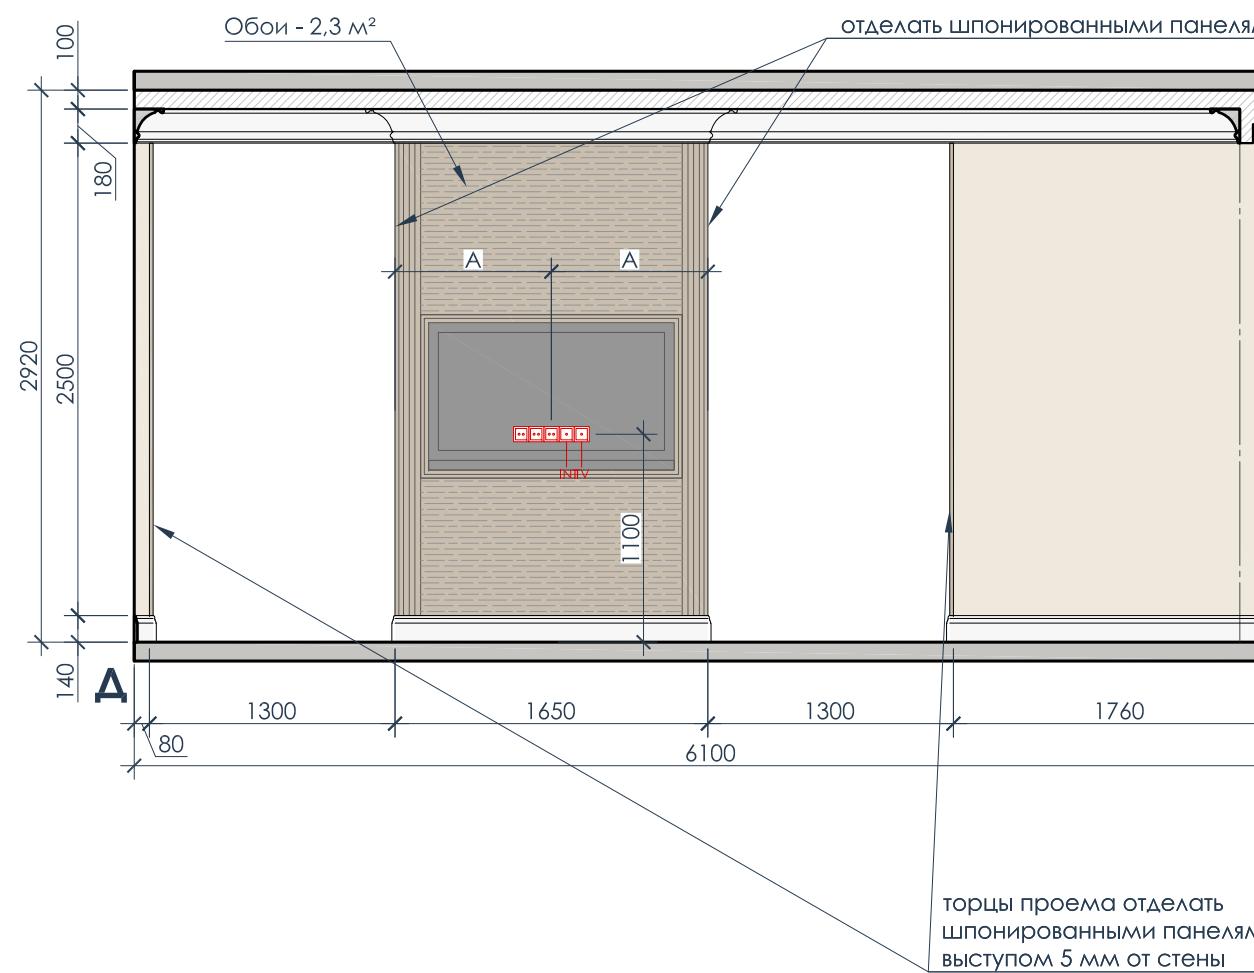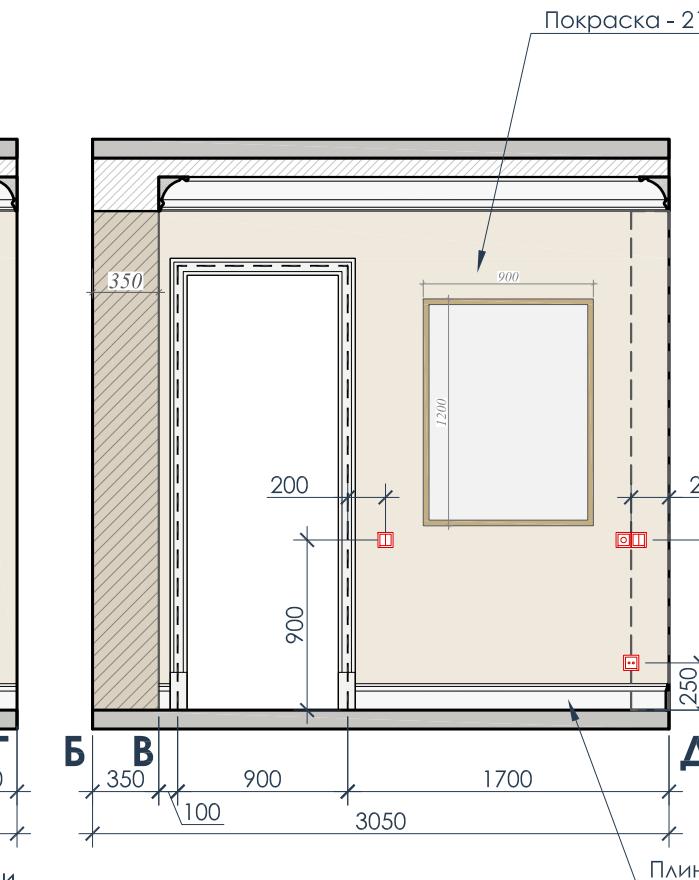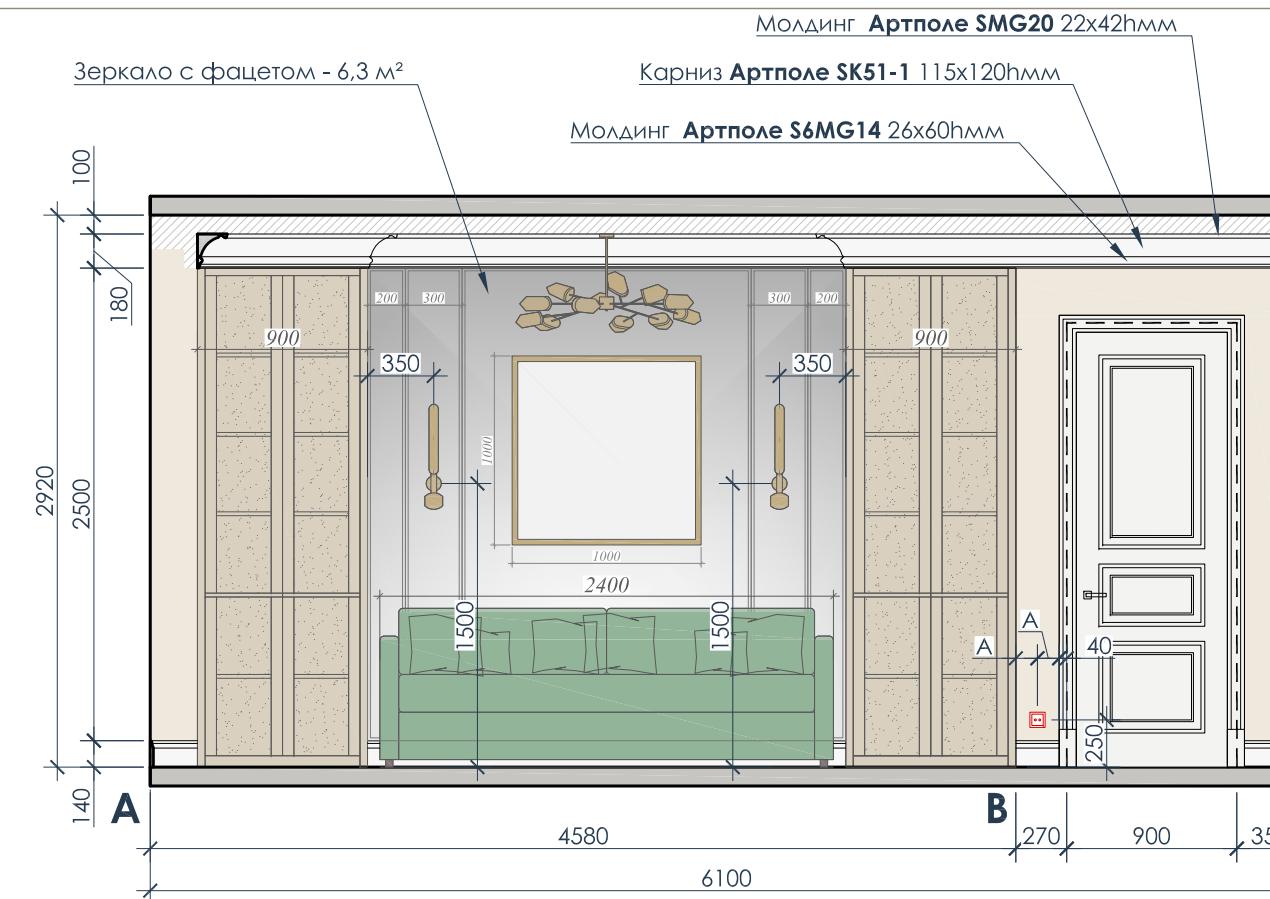

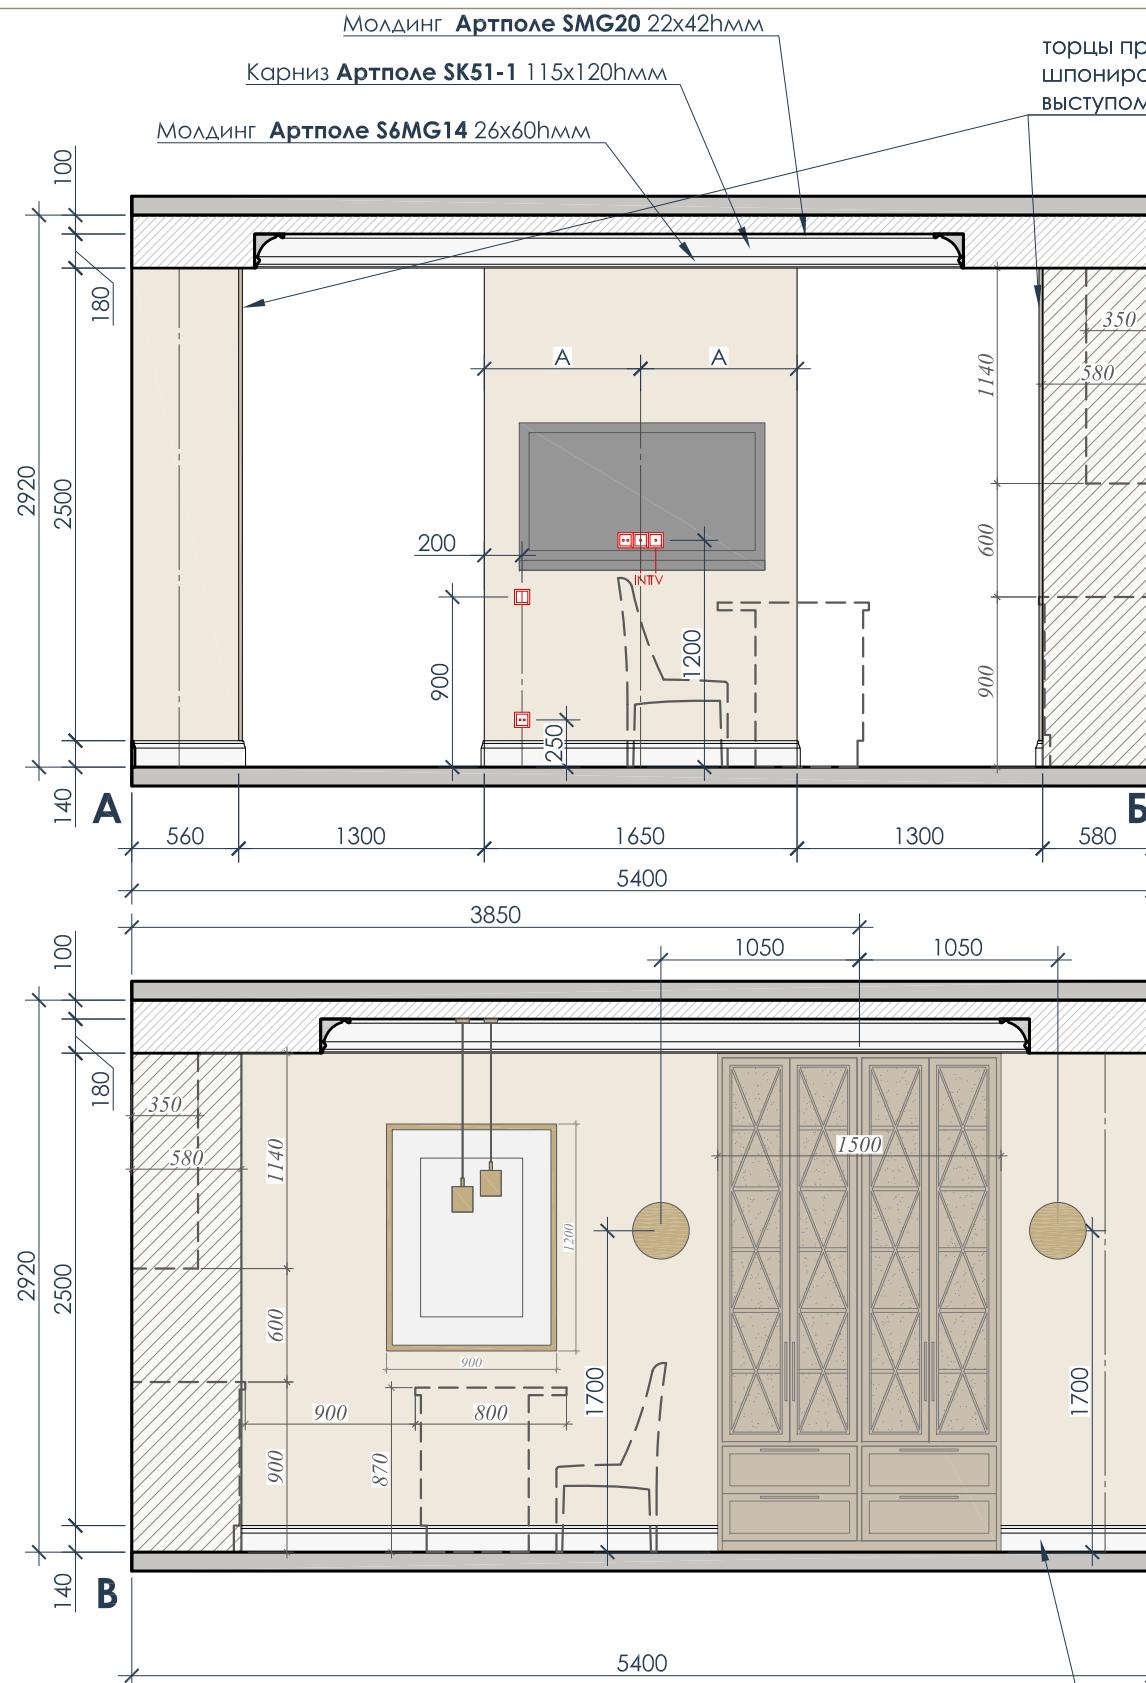


Наталья Широкорад  
8 926 394 10 04

Объект:  
Черняховского 19

## Развертки кухни №10

Лист	Листов
31	37

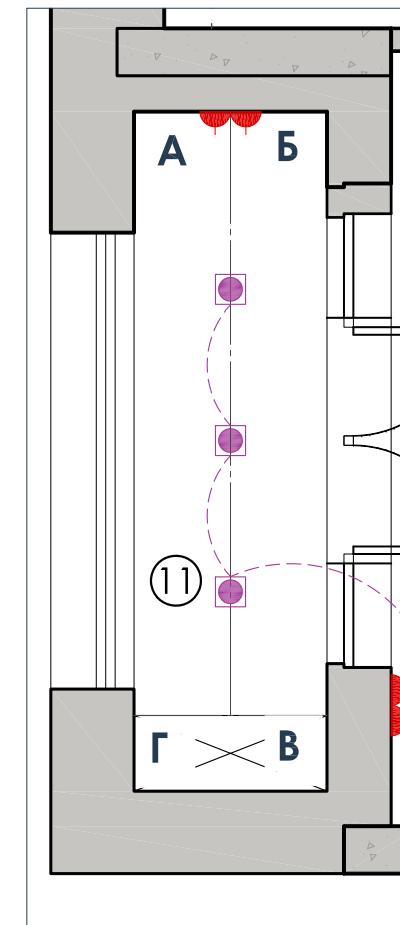

Марка по проекту	Фирма-производитель	Наименование	Эскиз	Кол-во, м <sup>2</sup>
<b>Полы</b>				
1		Паркет на фанере, цвет Стоунхедж с брашировкой		85,0
2	Atlas Concorde Russia	Керамогранит Empire Tajmahal Rett Lapp 600x600 мм		3,5
3	Atlas Concorde Russia	Керамогранит Volcano Grigio Rett 600x600 мм		4,0

Марка по проекту	Фирма-производитель	Наименование	Эскиз	Кол-во, м <sup>2</sup>
<b>Полы</b>				
4	Atlas Concorde Russia	Керамогранит Victory White Lapp 600x600 мм		25,7

**Примечание:** Все площади и длины даны без учета запаса

Марка по проекту	Фирма-производитель	Наименование	Эскиз	Кол-во, м <sup>2</sup>
<b>Стены</b>				
1	<u>Благостойкая краска</u>	<u>комнаты санузлы</u>		<b>224,2 18,6</b>
2	<u>Обои</u>	Тип 1		<b>5,6</b>
		Тип 2		<b>5,4</b>
		Тип 3		<b>2,3</b>
3	<u>Atlas Concorde Russia</u>	Керамогранит <b>Empire Tajmahal Rett Lapp</b> 600x1200 мм		<b>9,5</b>
4	<u>Atlas Concorde Russia</u>	Керамогранит <b>Empire Intarsi Rett Lapp</b> 600x1200 мм		<b>3,2</b>
5		<u>Бордюр</u>		<b>4,3 м.п.</b>
6	<u>Atlas Concorde Russia</u>	Керамогранит <b>Volcano Bianco Rett</b> 600x1200 мм		<b>10,4</b>
7	<u>Atlas Concorde Russia</u>	Керамогранит <b>Boost Pro 3D Urban Ivory</b> 400x800 мм		<b>1,6</b>
8	<u>Atlas Concorde Russia</u>	Керамогранит <b>Boost Pro Cream Mosaico Hex Blue</b> 250x285 мм		<b>1,9</b>
9		<u>Бордюр</u>		<b>5,0 м.п.</b>
10		<u>Вставки</u>		<b>4,0 м.п.</b>

Марка по проекту	Фирма-производитель	Наименование	Эскиз	Кол-во, п.м.
<b>Лепнина, плинтуса</b>				
1	<u>Артполе</u>	Молдинг <b>SMG20</b> 22x42hмм		<b>78,9</b>
2	<u>Артполе</u>	Карниз <b>SK51-1</b> 115x120hмм		<b>78,9</b>
3	<u>Артполе</u>	Молдинг <b>S6MG14</b> 26x60hмм		<b>78,9 14,6</b>
4	<u>Артполе</u>	Карниз <b>SK26G</b> 129x120hмм		<b>36,3</b>
5		Плинтус МДФ <b>140h</b> мм		<b>73,9</b>

**Примечание:** Все площади и длины даны без учета запаса

Марка по проекту	Фирма-производитель	Наименование	Эскиз	Кол-во, м <sup>2</sup>	Размеры, мм
1	-	Люстра Винтаж		1	-
2	Eichholtz	Настольная лампа <b>Cavo</b>		2	Ø 140 x h 730
3	-	Бра Ручная работа		2	-
4	Vitaluce	Подвесная люстра <b>V5347-7/6</b>		1	Ø 510 x h 510

Марка по проекту	Фирма-производитель	Наименование	Эскиз	Кол-во, м <sup>2</sup>	Размеры, мм
5	Favourite	Бра <b>2723-1W</b>		2	120x150x240h
6		Люстра Винтаж		1	
7	Eichholtz	Настольная лампа <b>Emerald</b>		2	Ø 430x h 670
8	Arte Lamp	Спот <b>A1677AP-1WH</b>		2	90x150x190h

Марка по проекту	Фирма-производитель	Наименование	Эскиз	Кол-во, м <sup>2</sup>	Размеры, мм
9	Crystal Lux	Подсветка для картин <b>CLT 123W450 BS</b>		1	170x170 x450h
10	lampatron	Потолочная люстра <b>Aleksandra</b>		1	Ø 980 x h 450
11	lampatron	Бра <b>Frigg</b>		2	h560
12		Подвес Винтаж		2	

Марка по проекту	Фирма-производитель	Наименование	Эскиз	Кол-во, м <sup>2</sup>	Размеры, мм
13	lampatron	Подвесные светильники <b>Robin</b>		7	Ø 110 x 135
14		Бра Ручная работа		2	
15	Roden	Гипсовый светильник <b>RD 052</b>		3	Ø81 h70
16	Roden	Встроенный гипсовый светильник <b>RD 113</b>		33	Ø98 h21

Марка по проекту	Фирма-производитель	Наименование	Эскиз	Кол-во, м <sup>2</sup>	Размеры, мм
17	-	Встраиваемый влагостойкий светильник под лампочку		<b>8</b>	Ø97
18	Roden	Светильник <b>RD 212</b>		<b>6</b>	120x230 x75h
19		Светодиодная подсветка		<b>2,9</b> п.м.	

Наталья Широкорад

8 926 394 10 04